




Plan 1 · cota 2700.00 m · MODO INSTALACIONES (puntos de insercion, sin geometria solida) · 8764 elementos

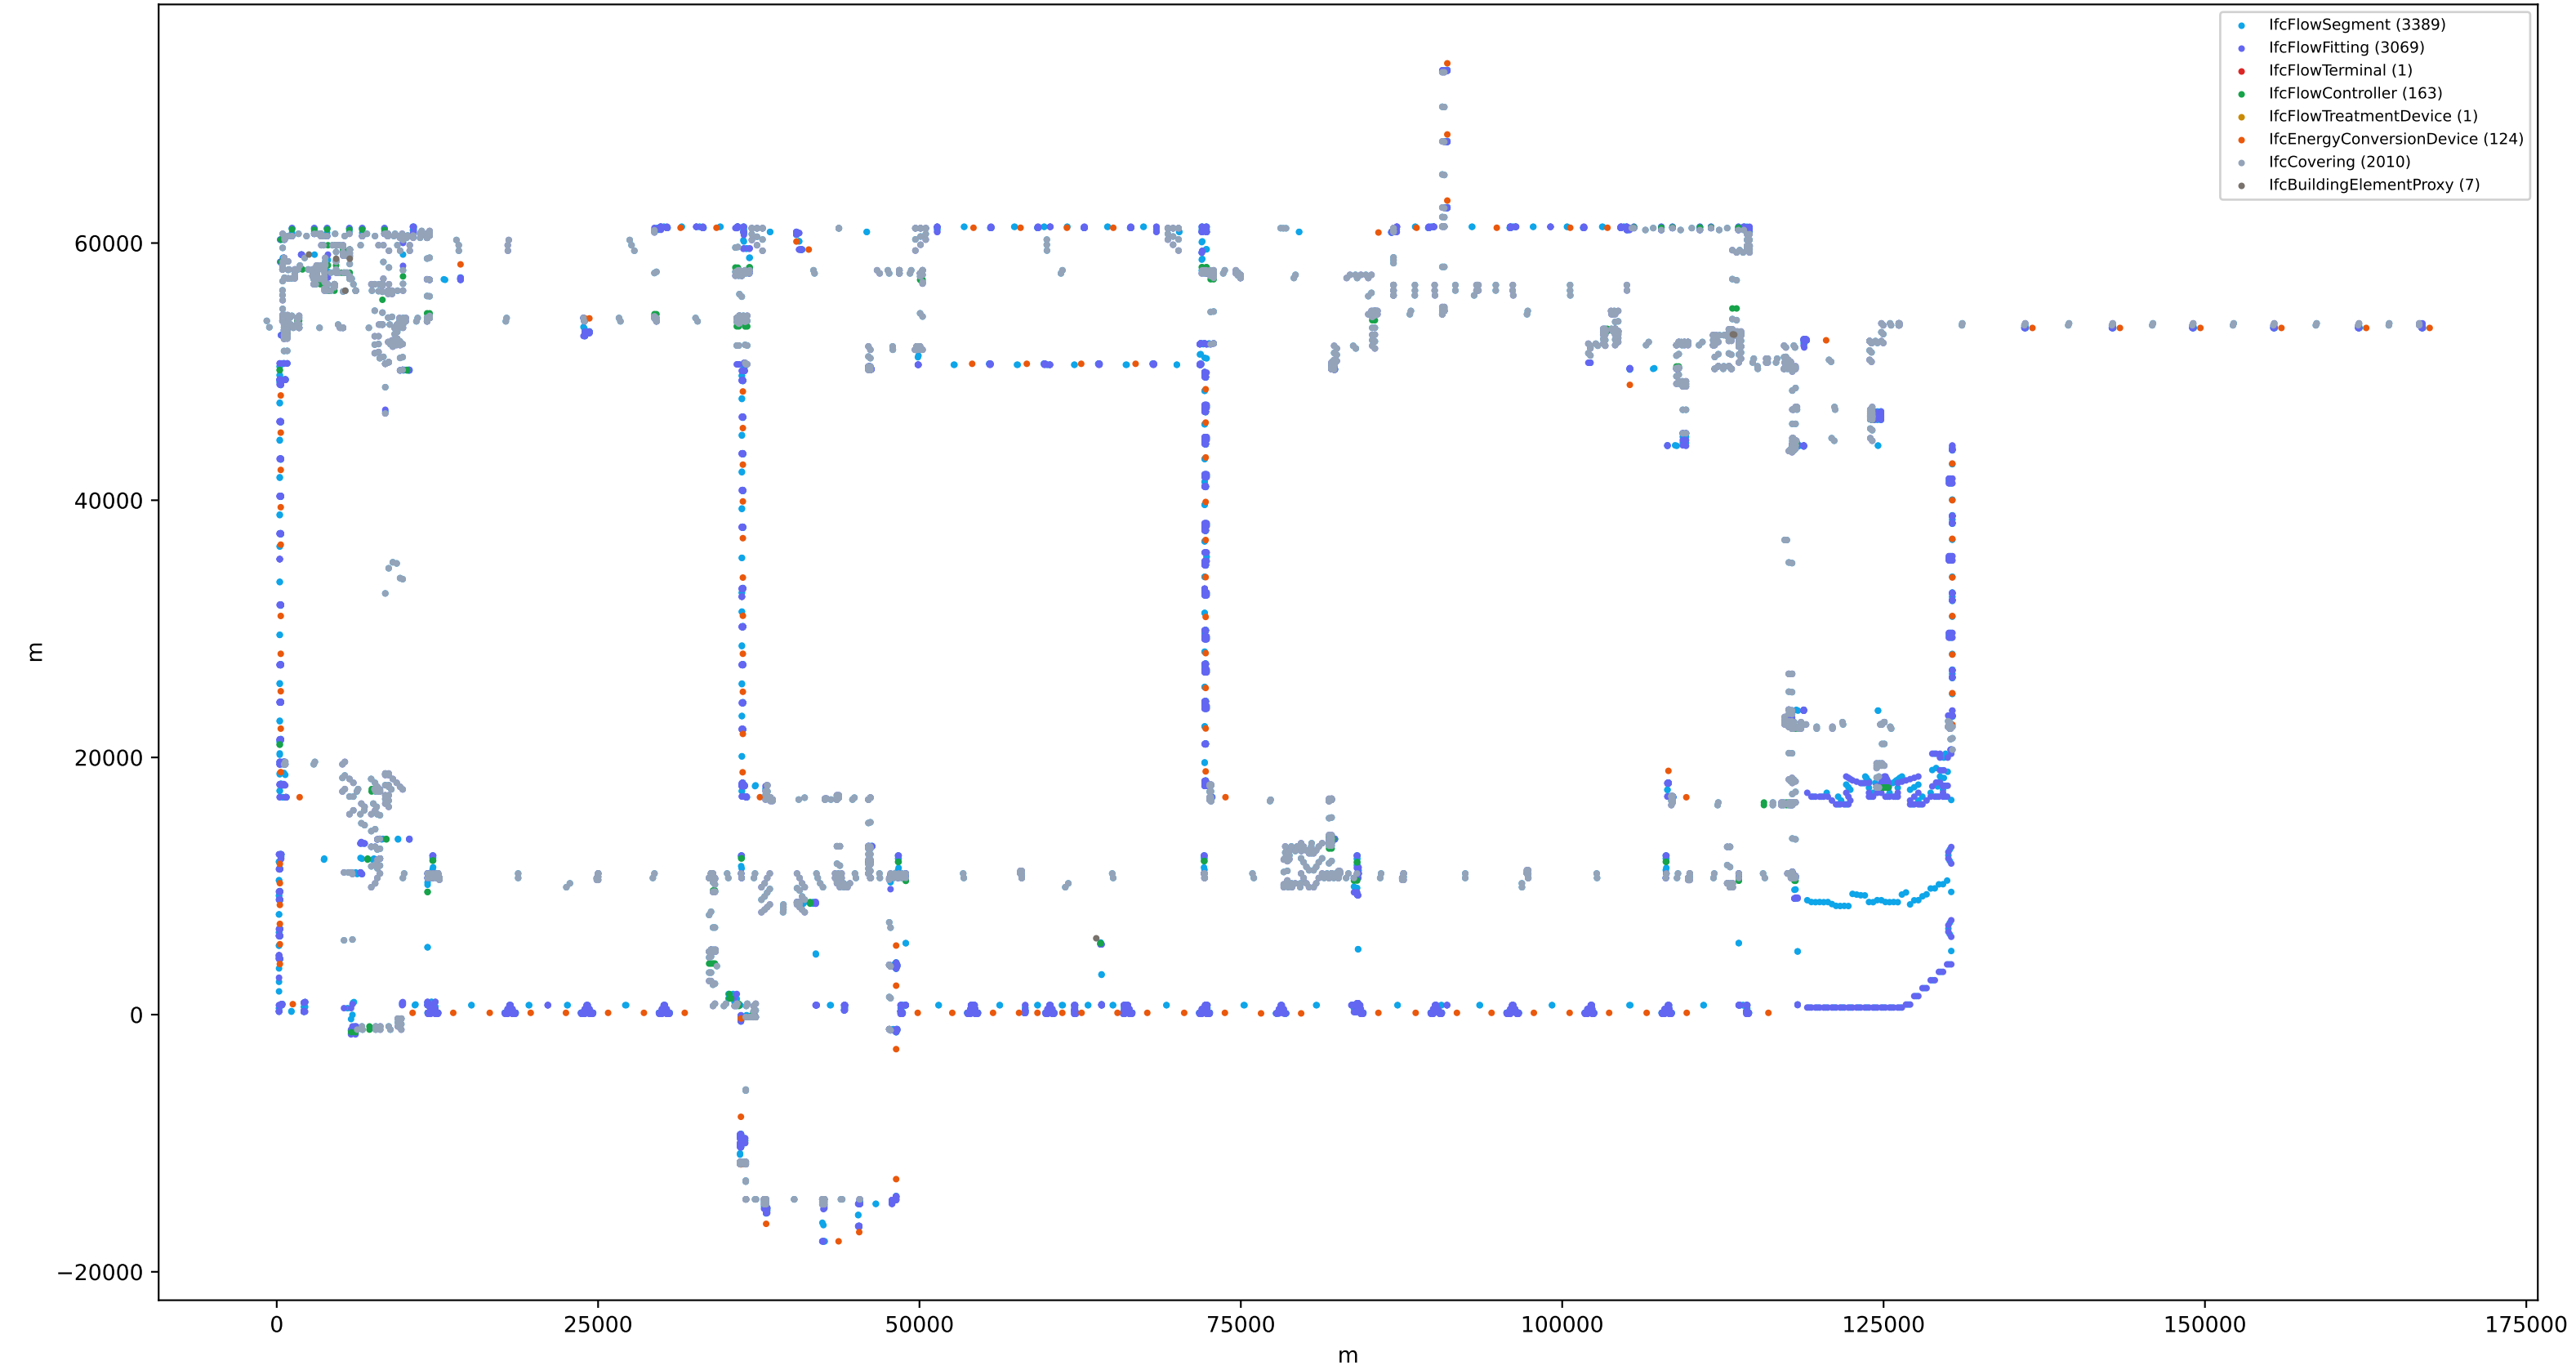

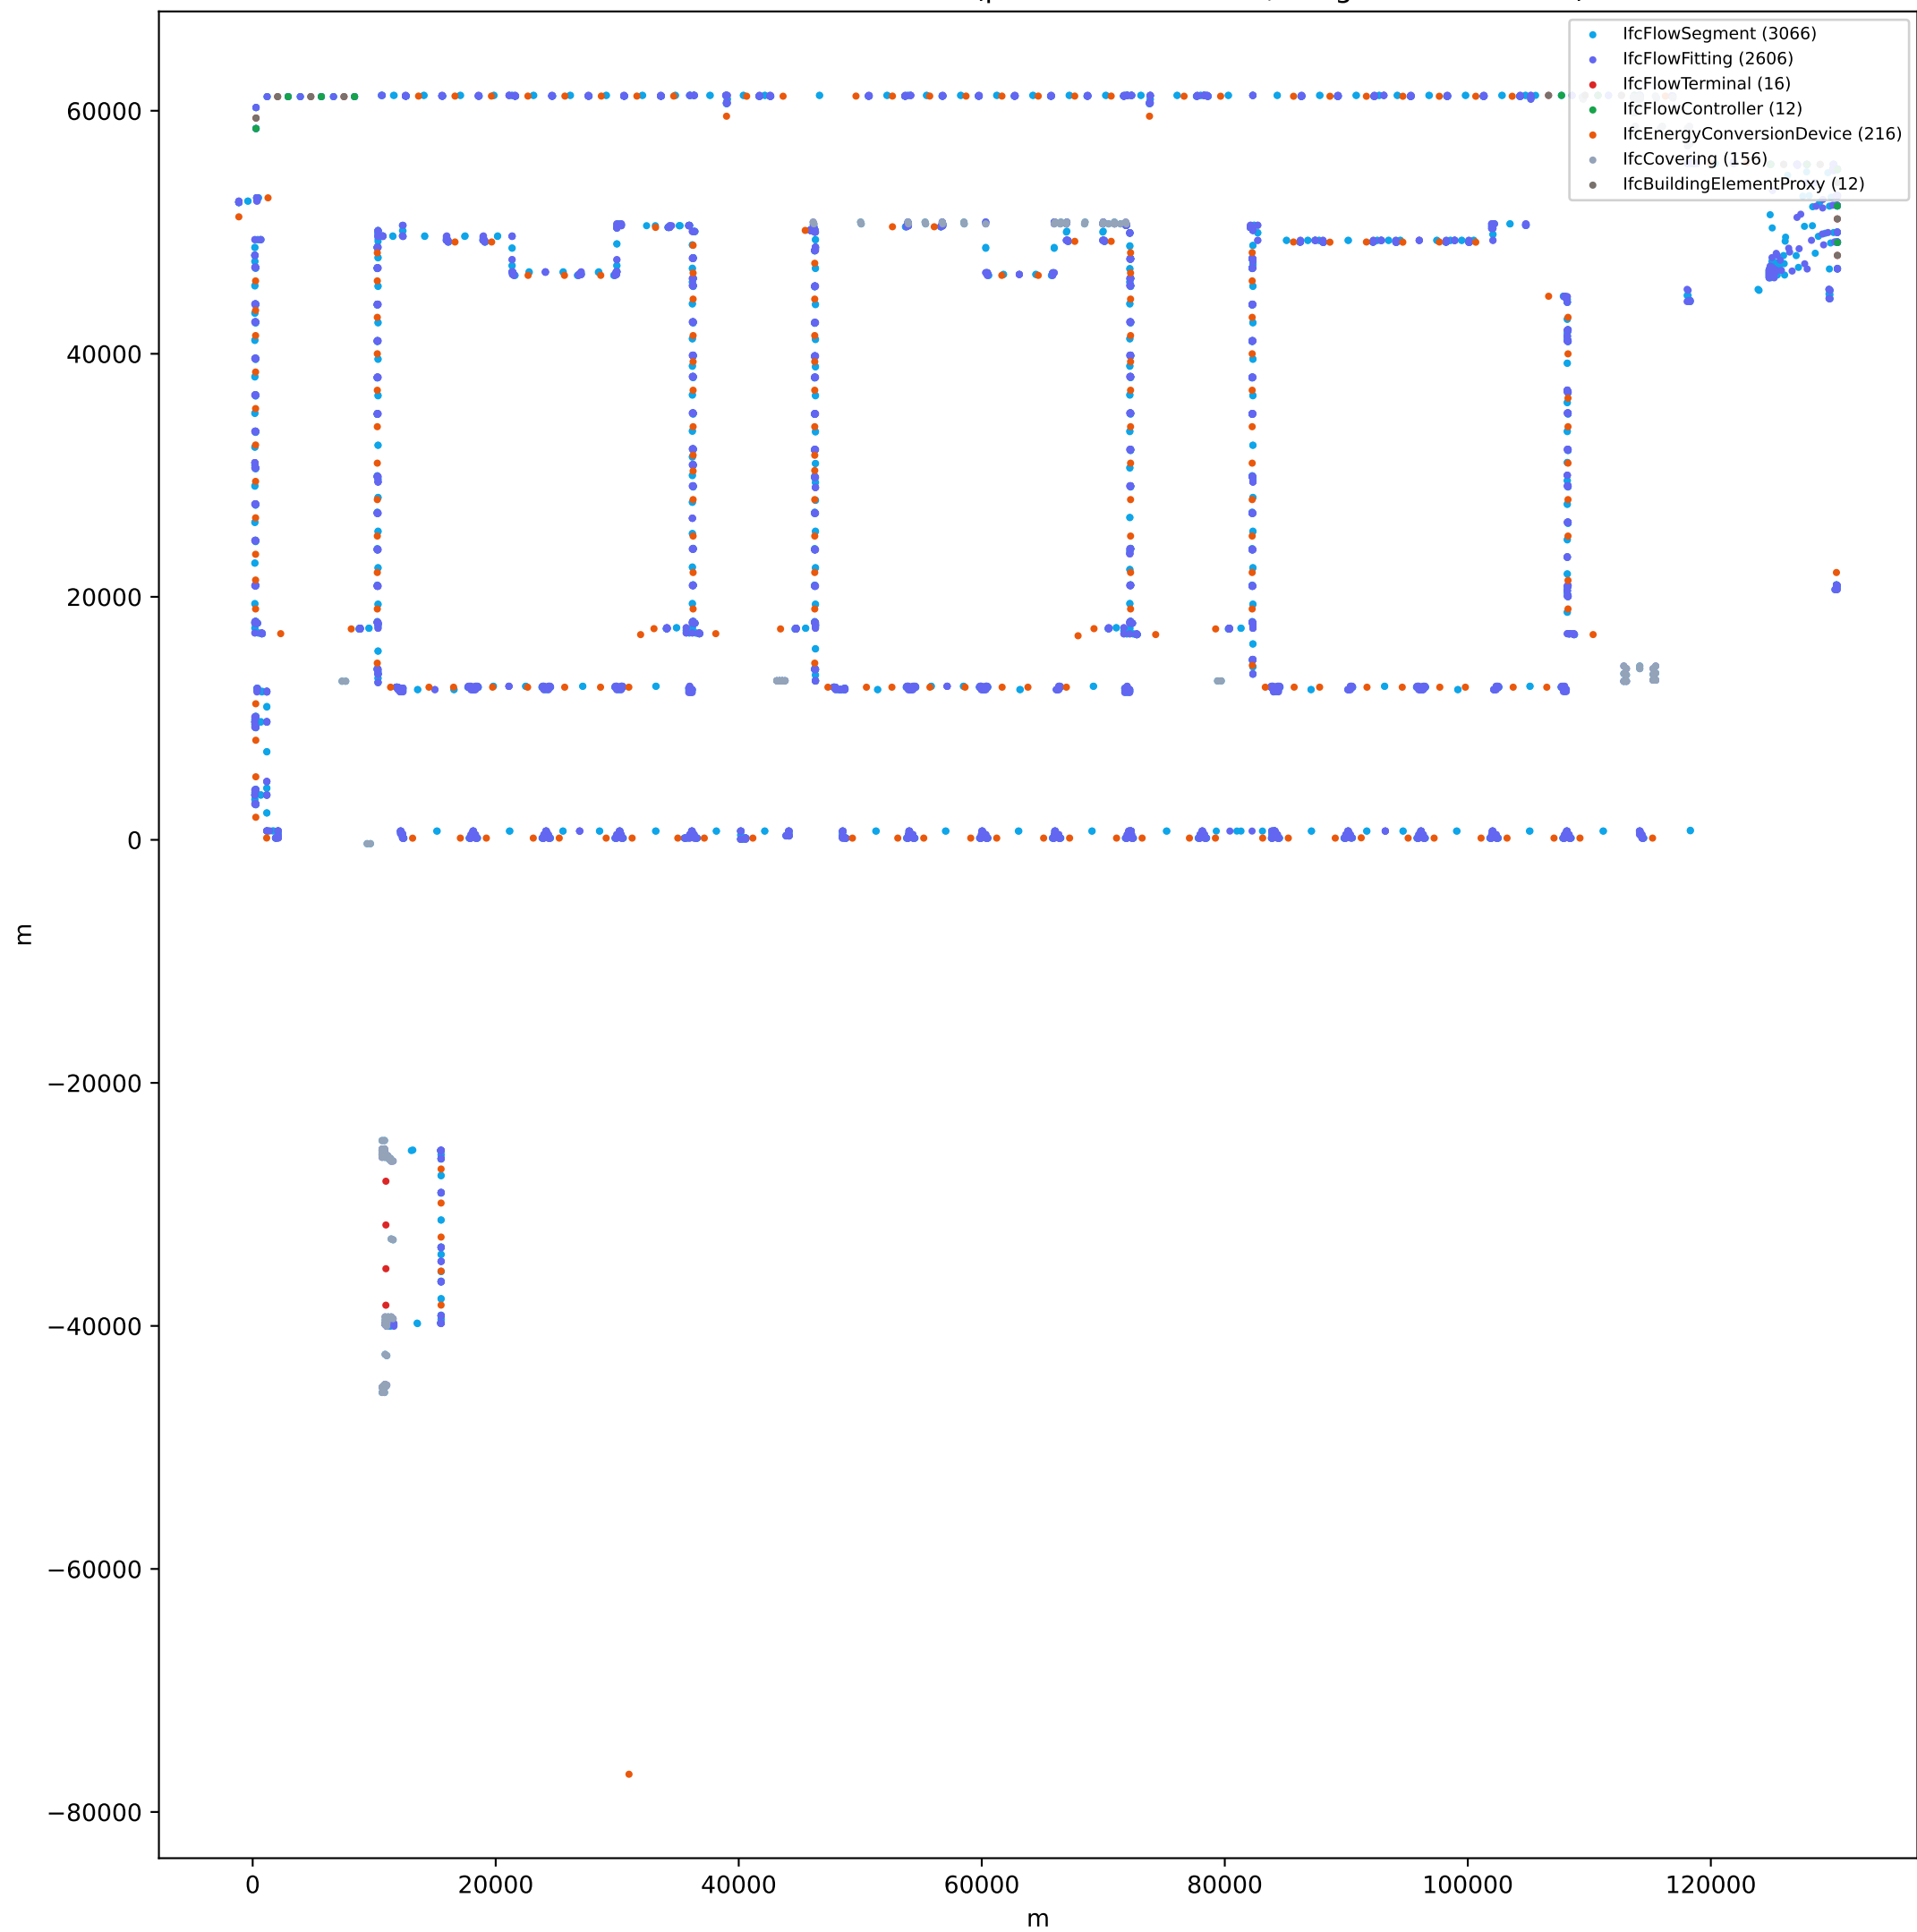

Plan 3 · cota 9300.00 m · MODO INSTALACIONES (puntos de insercion, sin geometria solida) · 6206 elementos

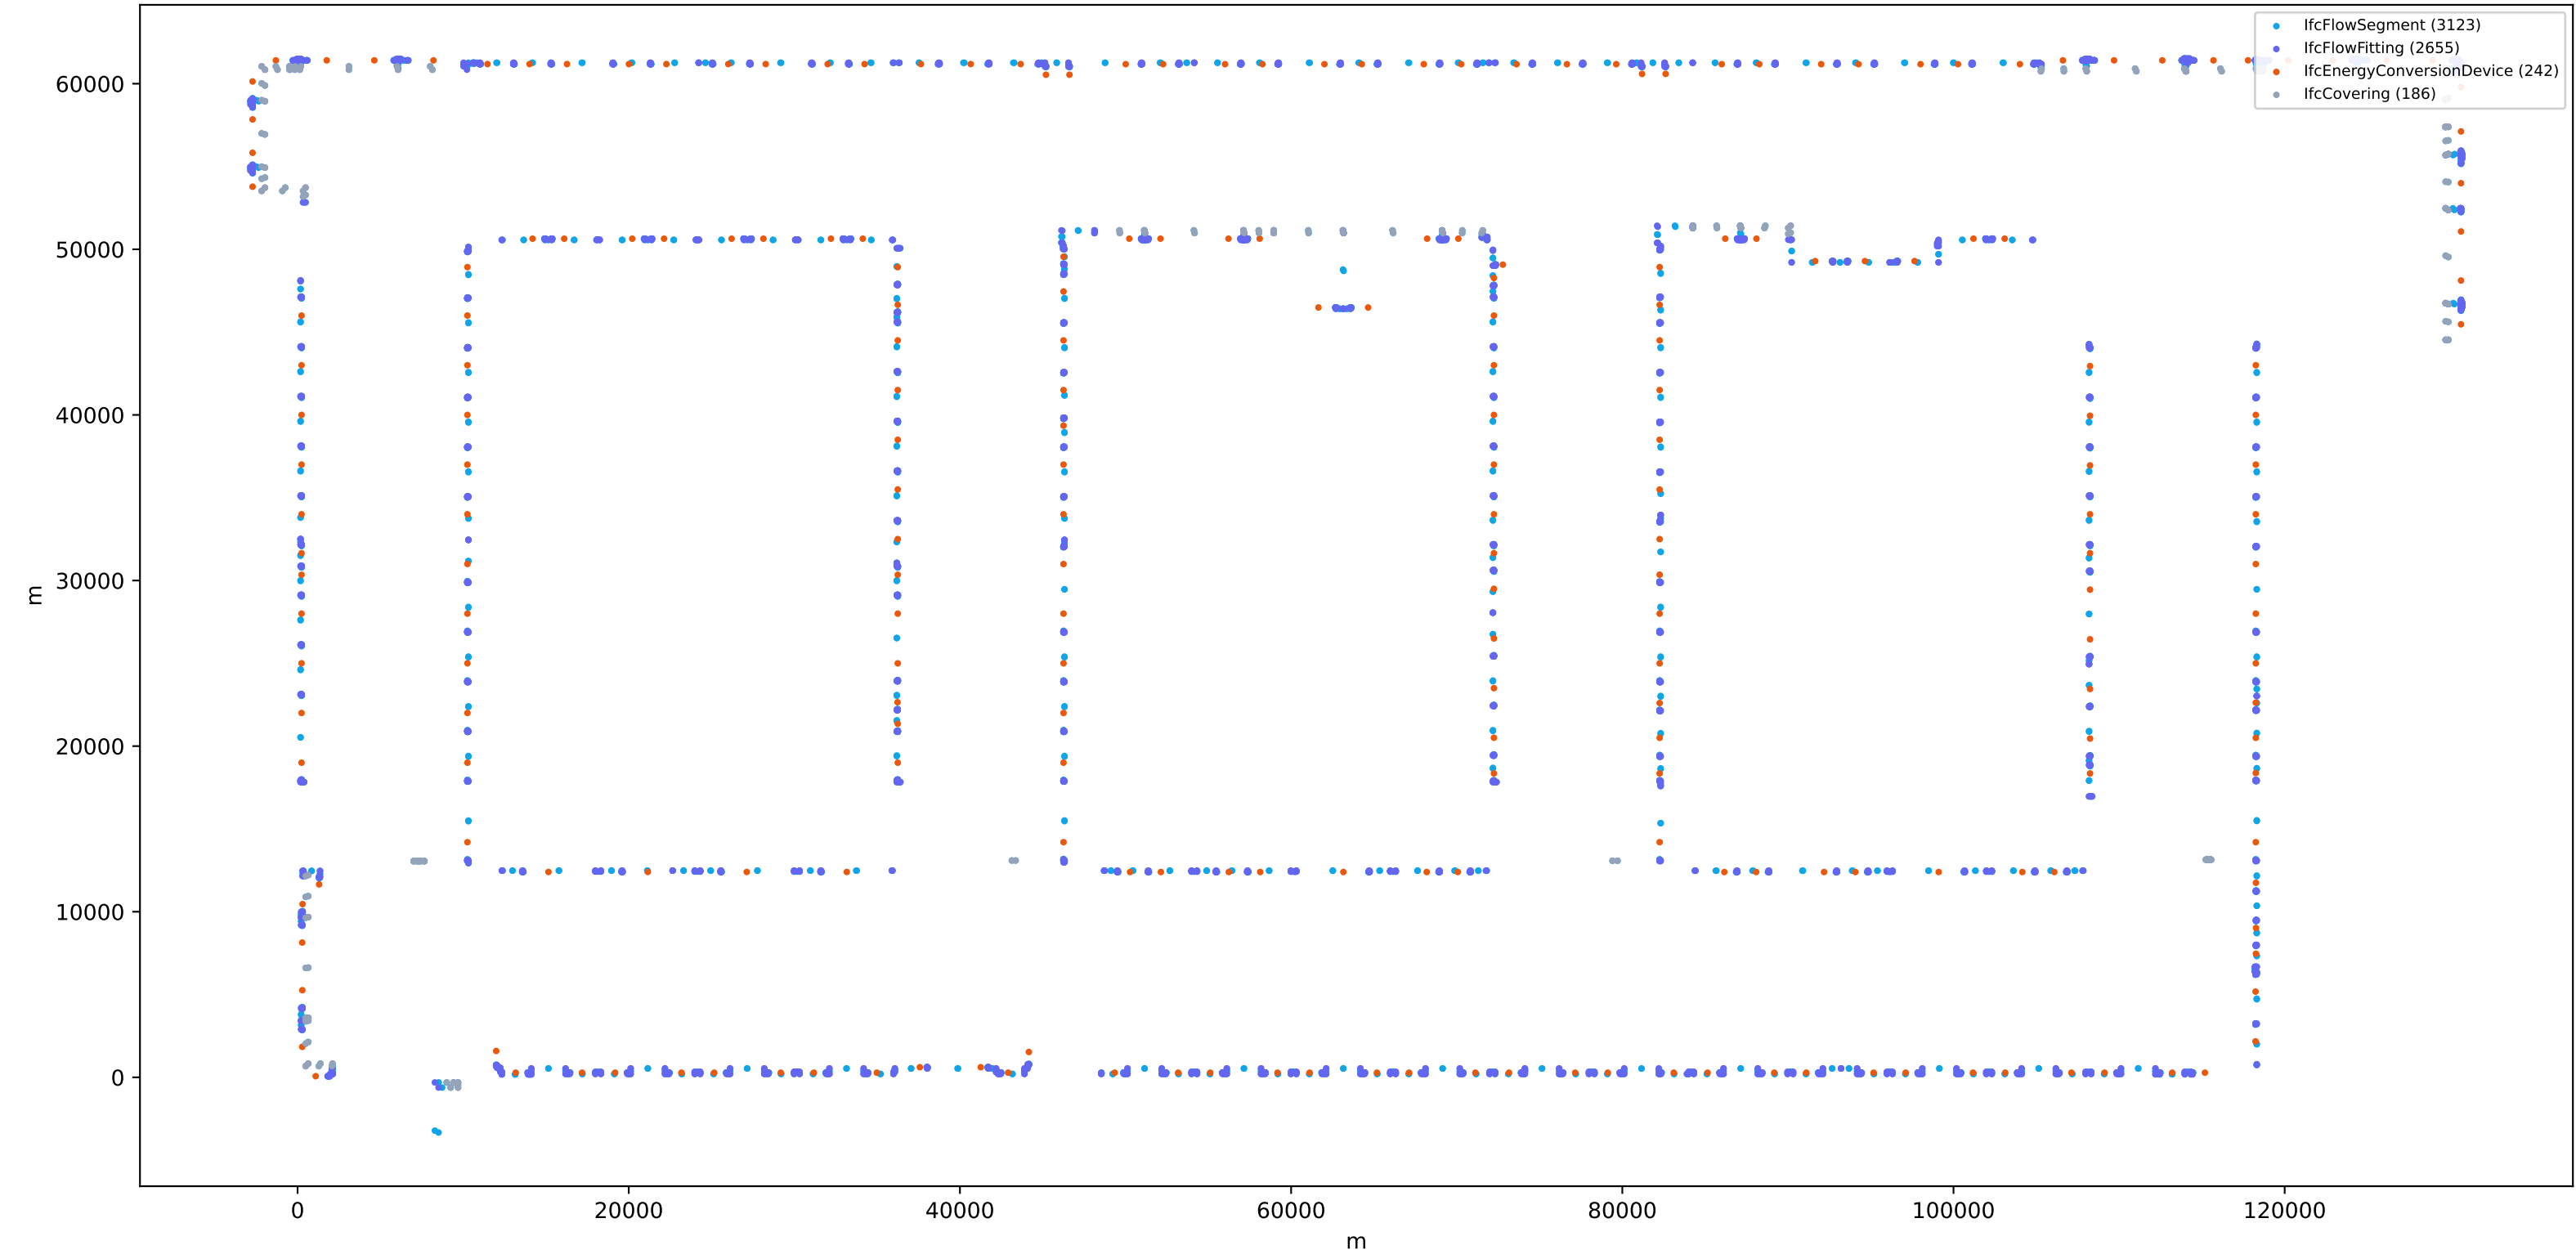

Plan 4 · cota 12300.00 m · MODO INSTALACIONES (puntos de insercion, sin geometria solida) · 1447 elementos

