




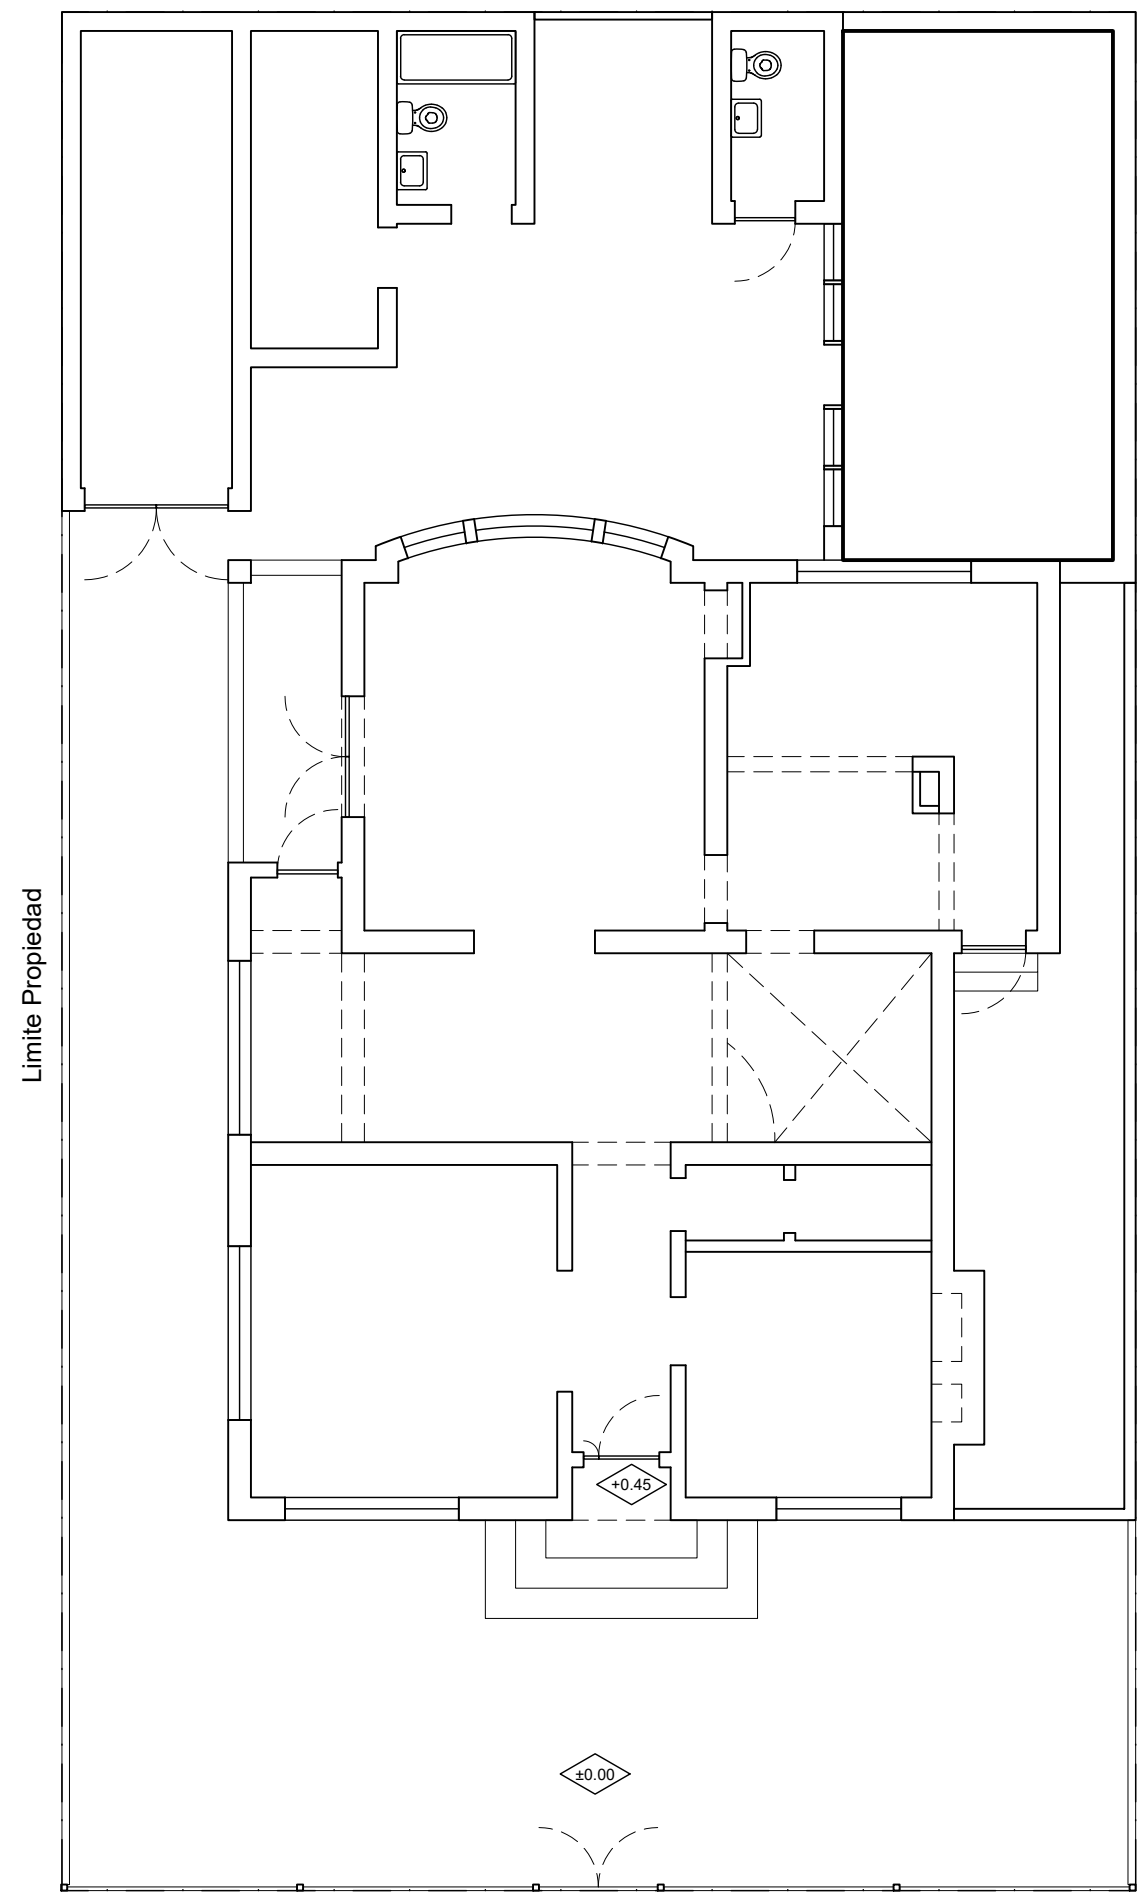


Situacion Existente Nivel 1
Esc. 1:100

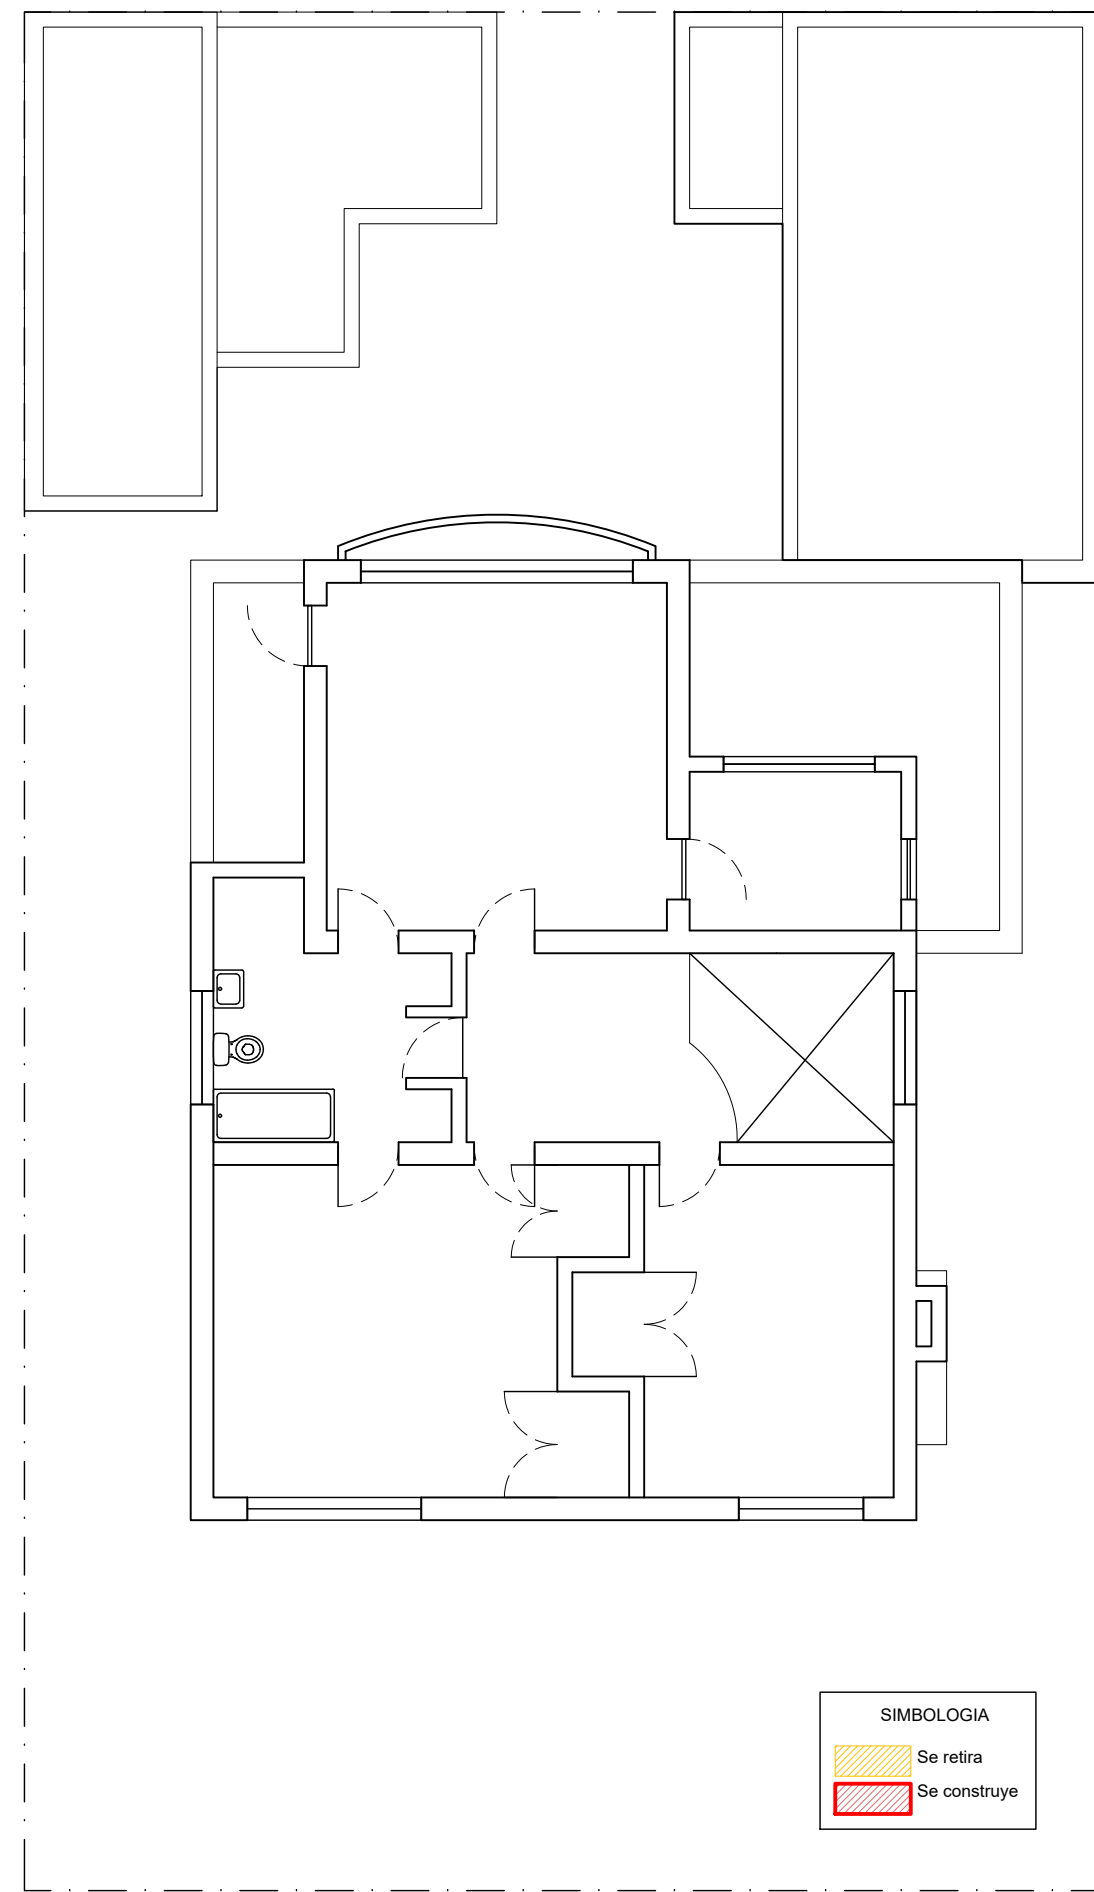

Situacion Existente Nivel 2
Esc. 1:100

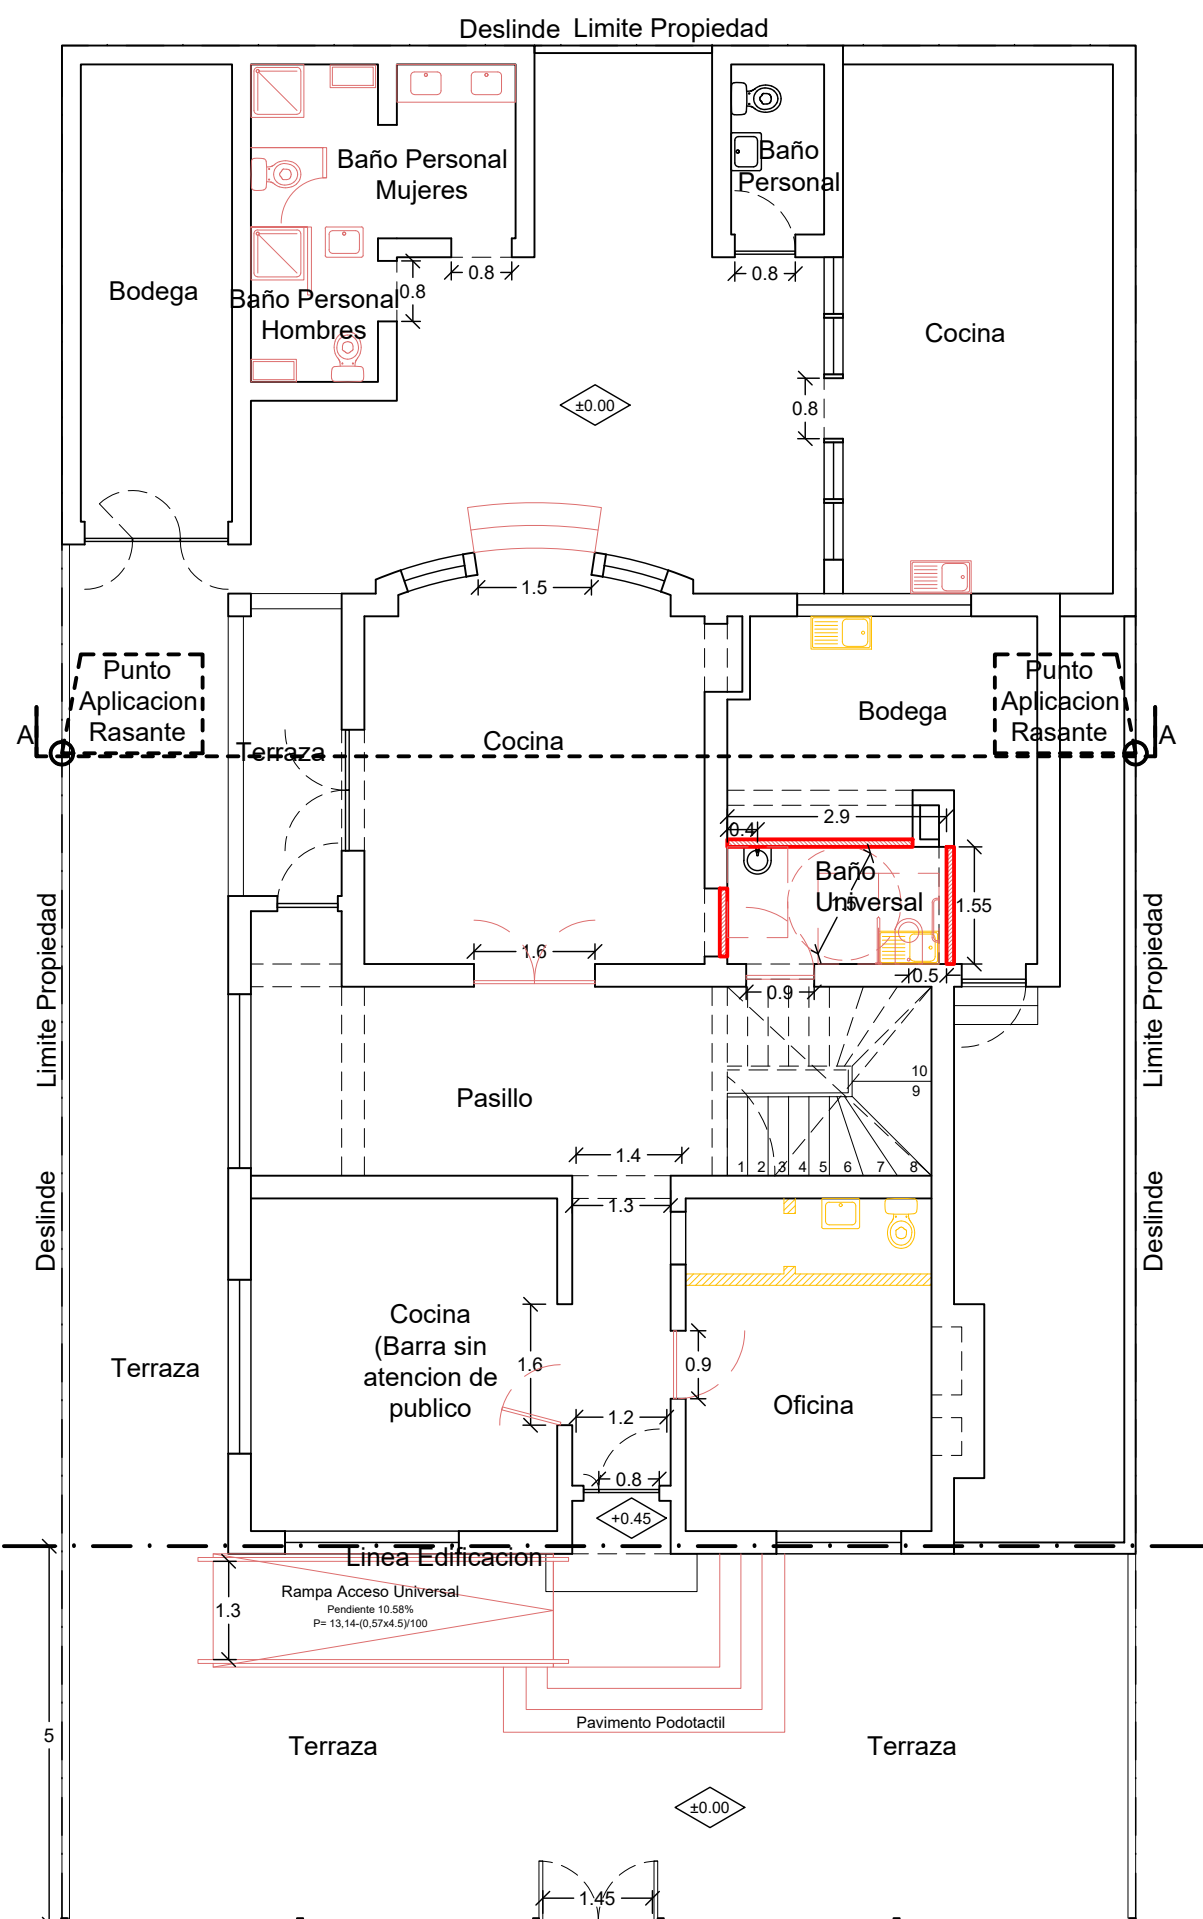


Situacion Propuesta Nivel 1
Esc. 1:100

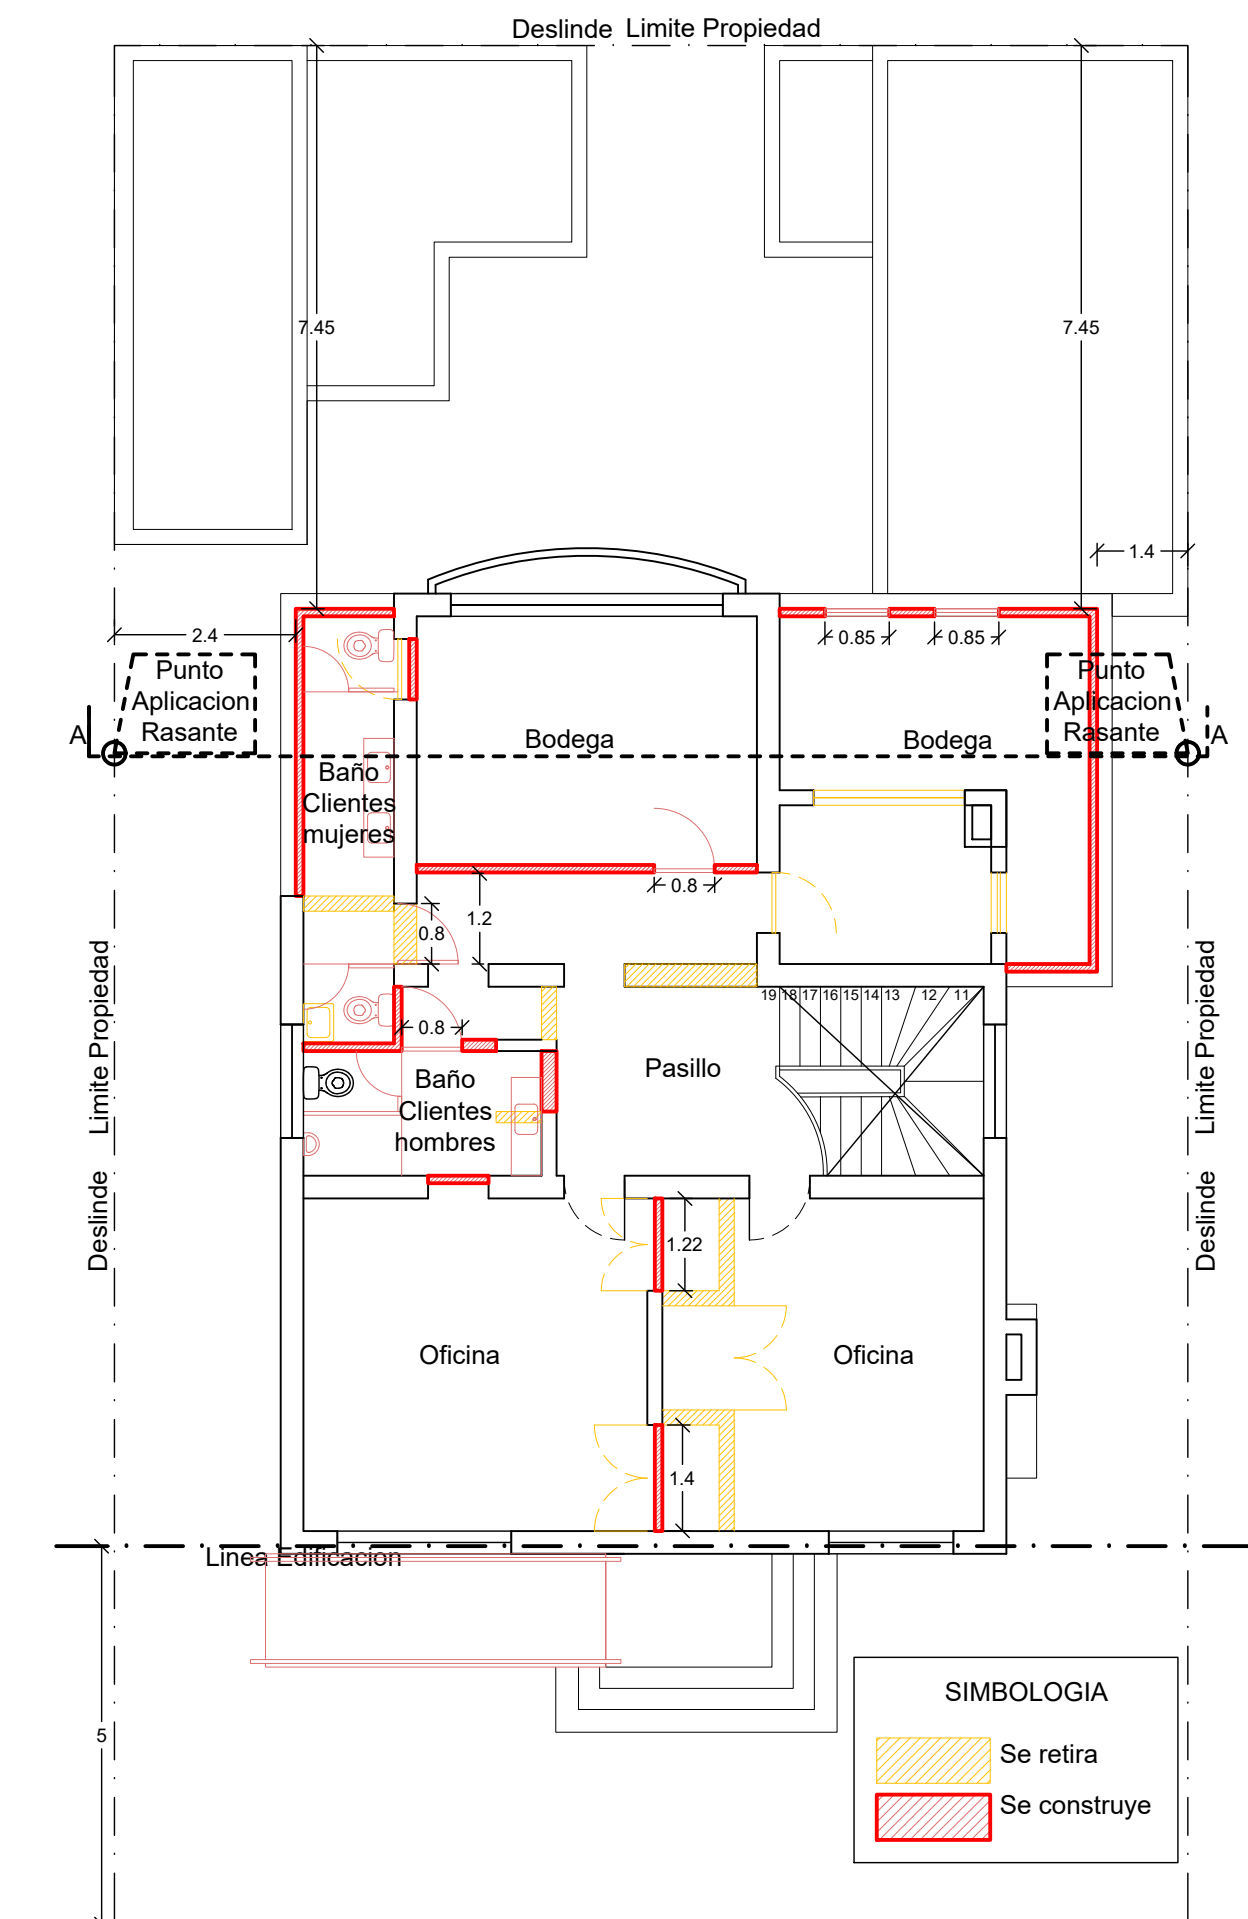


Situacion Propuesta Nivel 2
Esc. 1:100

Nivel 1

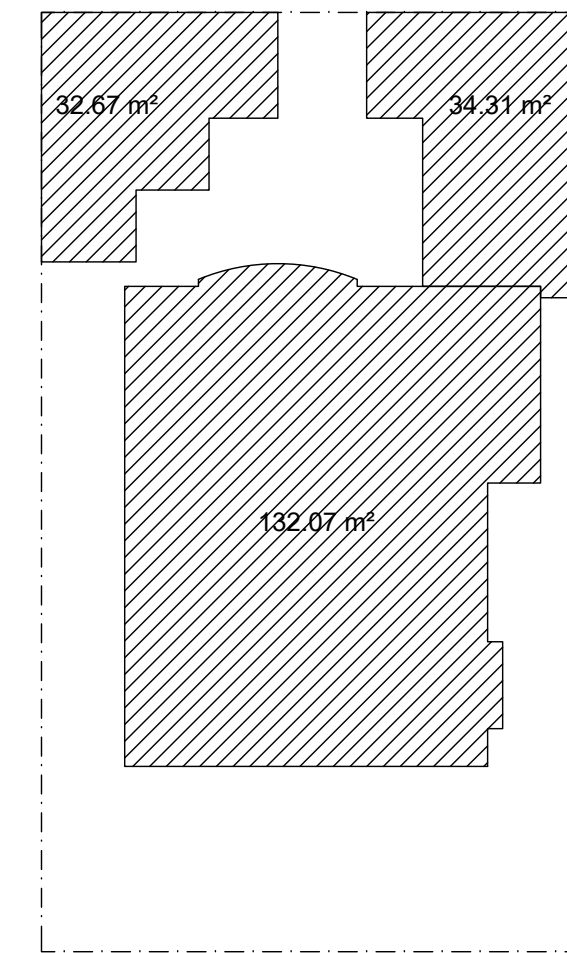


Resumen de Superficies			
	Exist	Proy	TOTAL
Nivel -1	9,00	0,00	9,00
Nivel 1	197,04	0,00	197,04
Nivel 2	101,86	17,90	119,76
TOTAL	298,90	17,90	316,80

Nivel 2

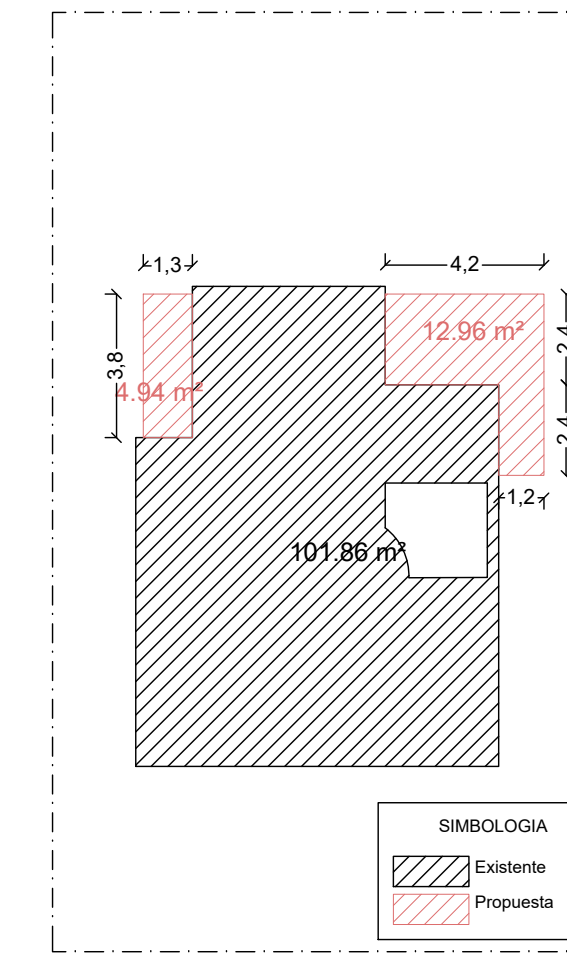


Cuadro de Superficies Normativas				
Destino de la Edificación	Sup.Total Existente	Sup.Total Proyectada	N° Pisos sobre N.N.T.	
Vivienda	289,90	316,80	2	
Superficie Terreno	Coef. Constructibilidad	Coef. de Ocupación de Suelo	Niv 1: n/a	
388,00	Permitido 1,4	Permitido (N1 y N Sup.)	Sup.: 0,4	
	Existente 0,7	Existente	51%	
	Proyectado 0,8	Proyectado	51%	

Cuadro de Superficies Propuesta
Esc. 1:250

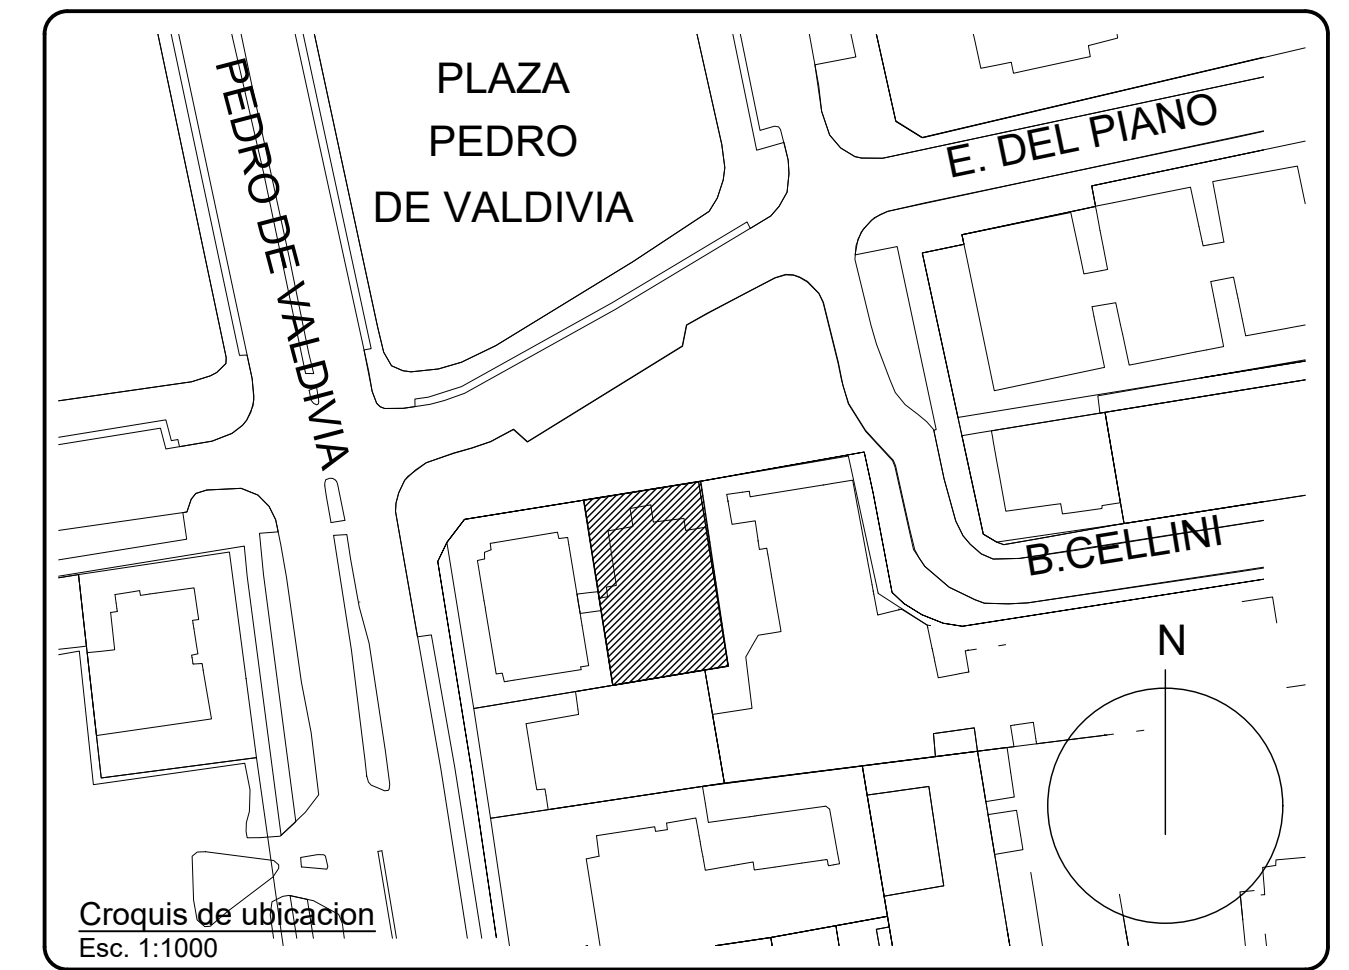

Croquis de ubicación
Esc. 1:1000


Nivel 1

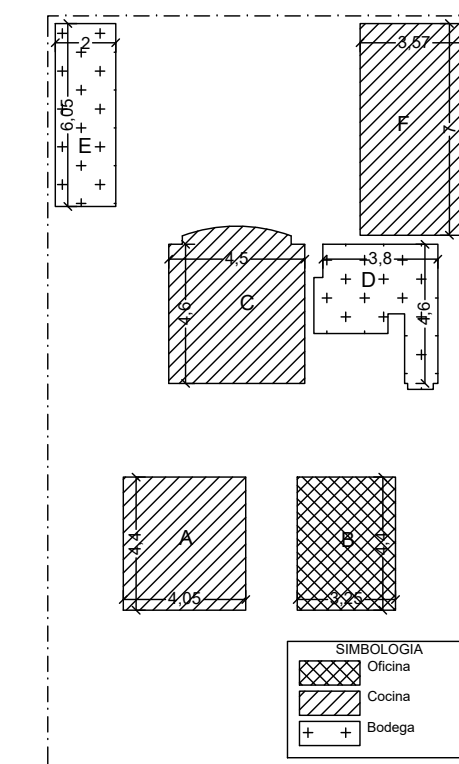

Estudio de Carga de Ocupacion				
Polygono	Destino	C.Ocup	Superficie	Personas
Permiso Original (14/44)				
Nivel 1	Vivienda	30 m²/p	120,13	4,00
Nivel 2	Vivienda	30 m²/p	91,05	3,04
TOTAL				8
Permiso DOM2285 del 29-9-85 (Preuniversitario)				
Nivel 1	Oficina	10 m²/p	80,10	8,01
	S. Clases	1,5 m²/p	25,00	16,67
Nivel 2	Oficina	10 m²/p	65,04	6,50
TOTAL				32
Situacion Proyectada				
Nivel 1	Cocina	15 m²/p	65,29	4,35
	Oficina	10 m²/p	14,30	1,43
	Bodega	40 m²/p	25,49	0,64
Nivel 2	Oficina	10 m²/p	38,71	3,87
	Bodega	40 m²/p	38,87	0,97
TOTAL				12

Estudio Carga de Ocupacion Propuesta
Esc. 1:250

Nivel 2

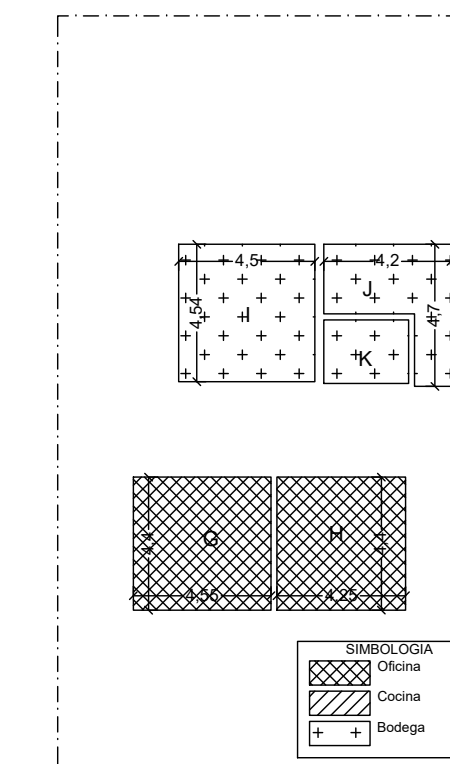

Desglose de Superfices y C. de Ocupacion				
Polygono	Destino	C.Ocup	Superficie	TOTAL
Nivel 1				
A	Cocina	15 m²/p	17,83	1,19
B	Oficina	10 m²/p	14,30	1,43
C	Cocina	15 m²/p	22,48	1,50
D	Bodega	40 m²/p	13,39	0,33
E	Bodega	40 m²/p	12,10	0,30
F	Cocina	15 m²/p	24,99	1,67
Nivel 2				
G	Oficina	10 m²/p	20,02	2,00
H	Oficina	10 m²/p	18,69	1,87
I	Bodega	40 m²/p	20,45	0,51
J	Bodega	40 m²/p	12,54	0,31
K	Bodega	40 m²/p	5,88	0,15
subtotal				11,26
TOTAL				12 Pers.

I. Municipalidad de Providencia

Habilt. Rest. Plaza Pedro de Valdivia


ASESORIAS E INVERSIONES CONCHALI LTDA
Propietario




Propietario: Asesorias e Inversiones Conchali Ltda
RUT: 78.796.070-7

Dirección: Plaza Pedro de Valdivia n°:2025
Comuna: Providencia
rol: 03228 - 012
Destino Solicitado: Restaurant


Contenido:
-Plano Situacion Existente y Propuesta
- Cuadro superficie Exis. y Propuesta

Cristian Wrbka M.
rol: 3-10885
Arquitecto
cwrwka@eieconsultores.cl

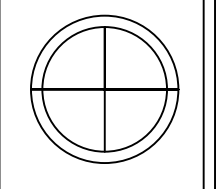


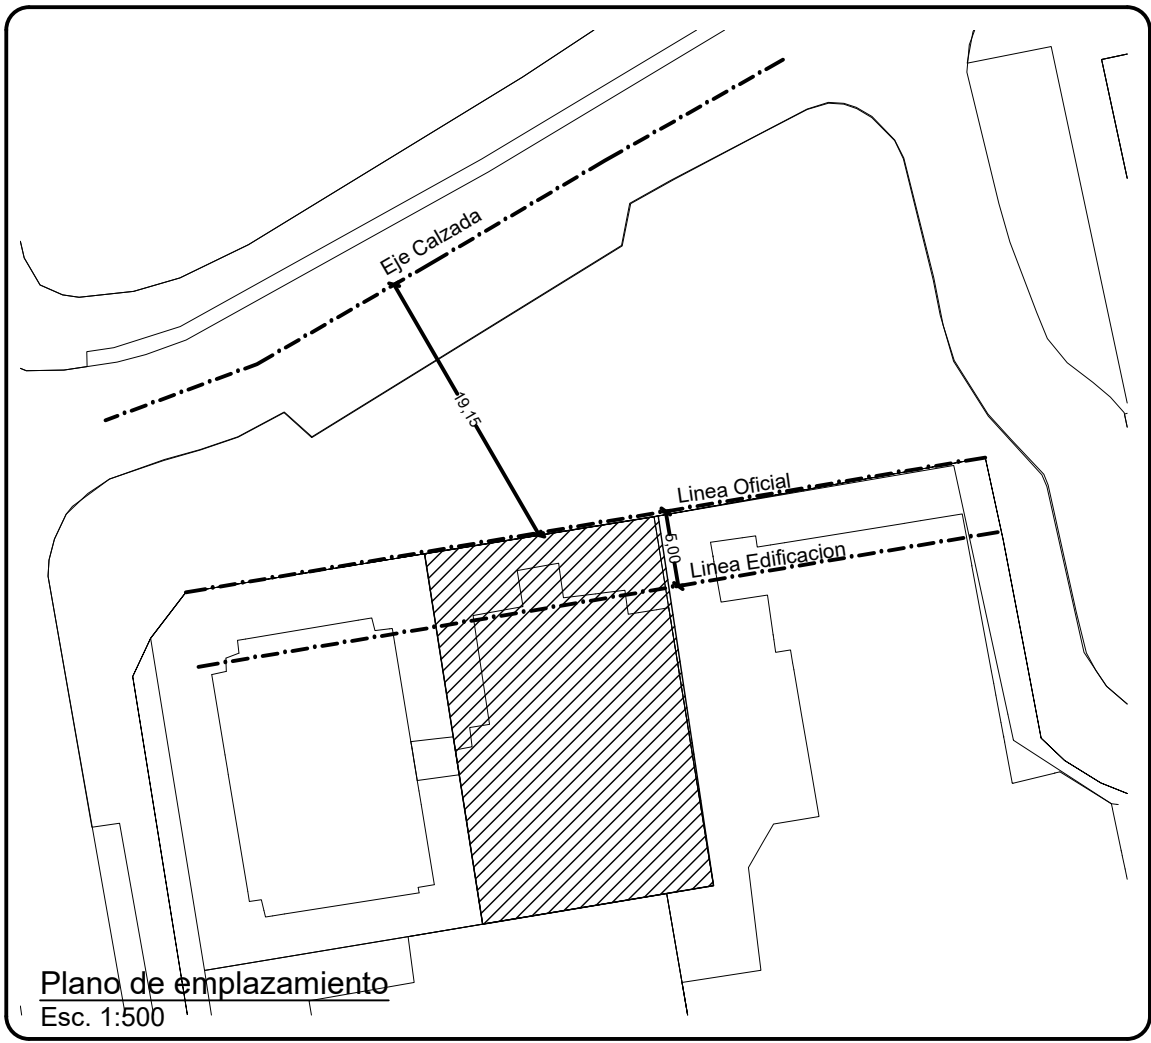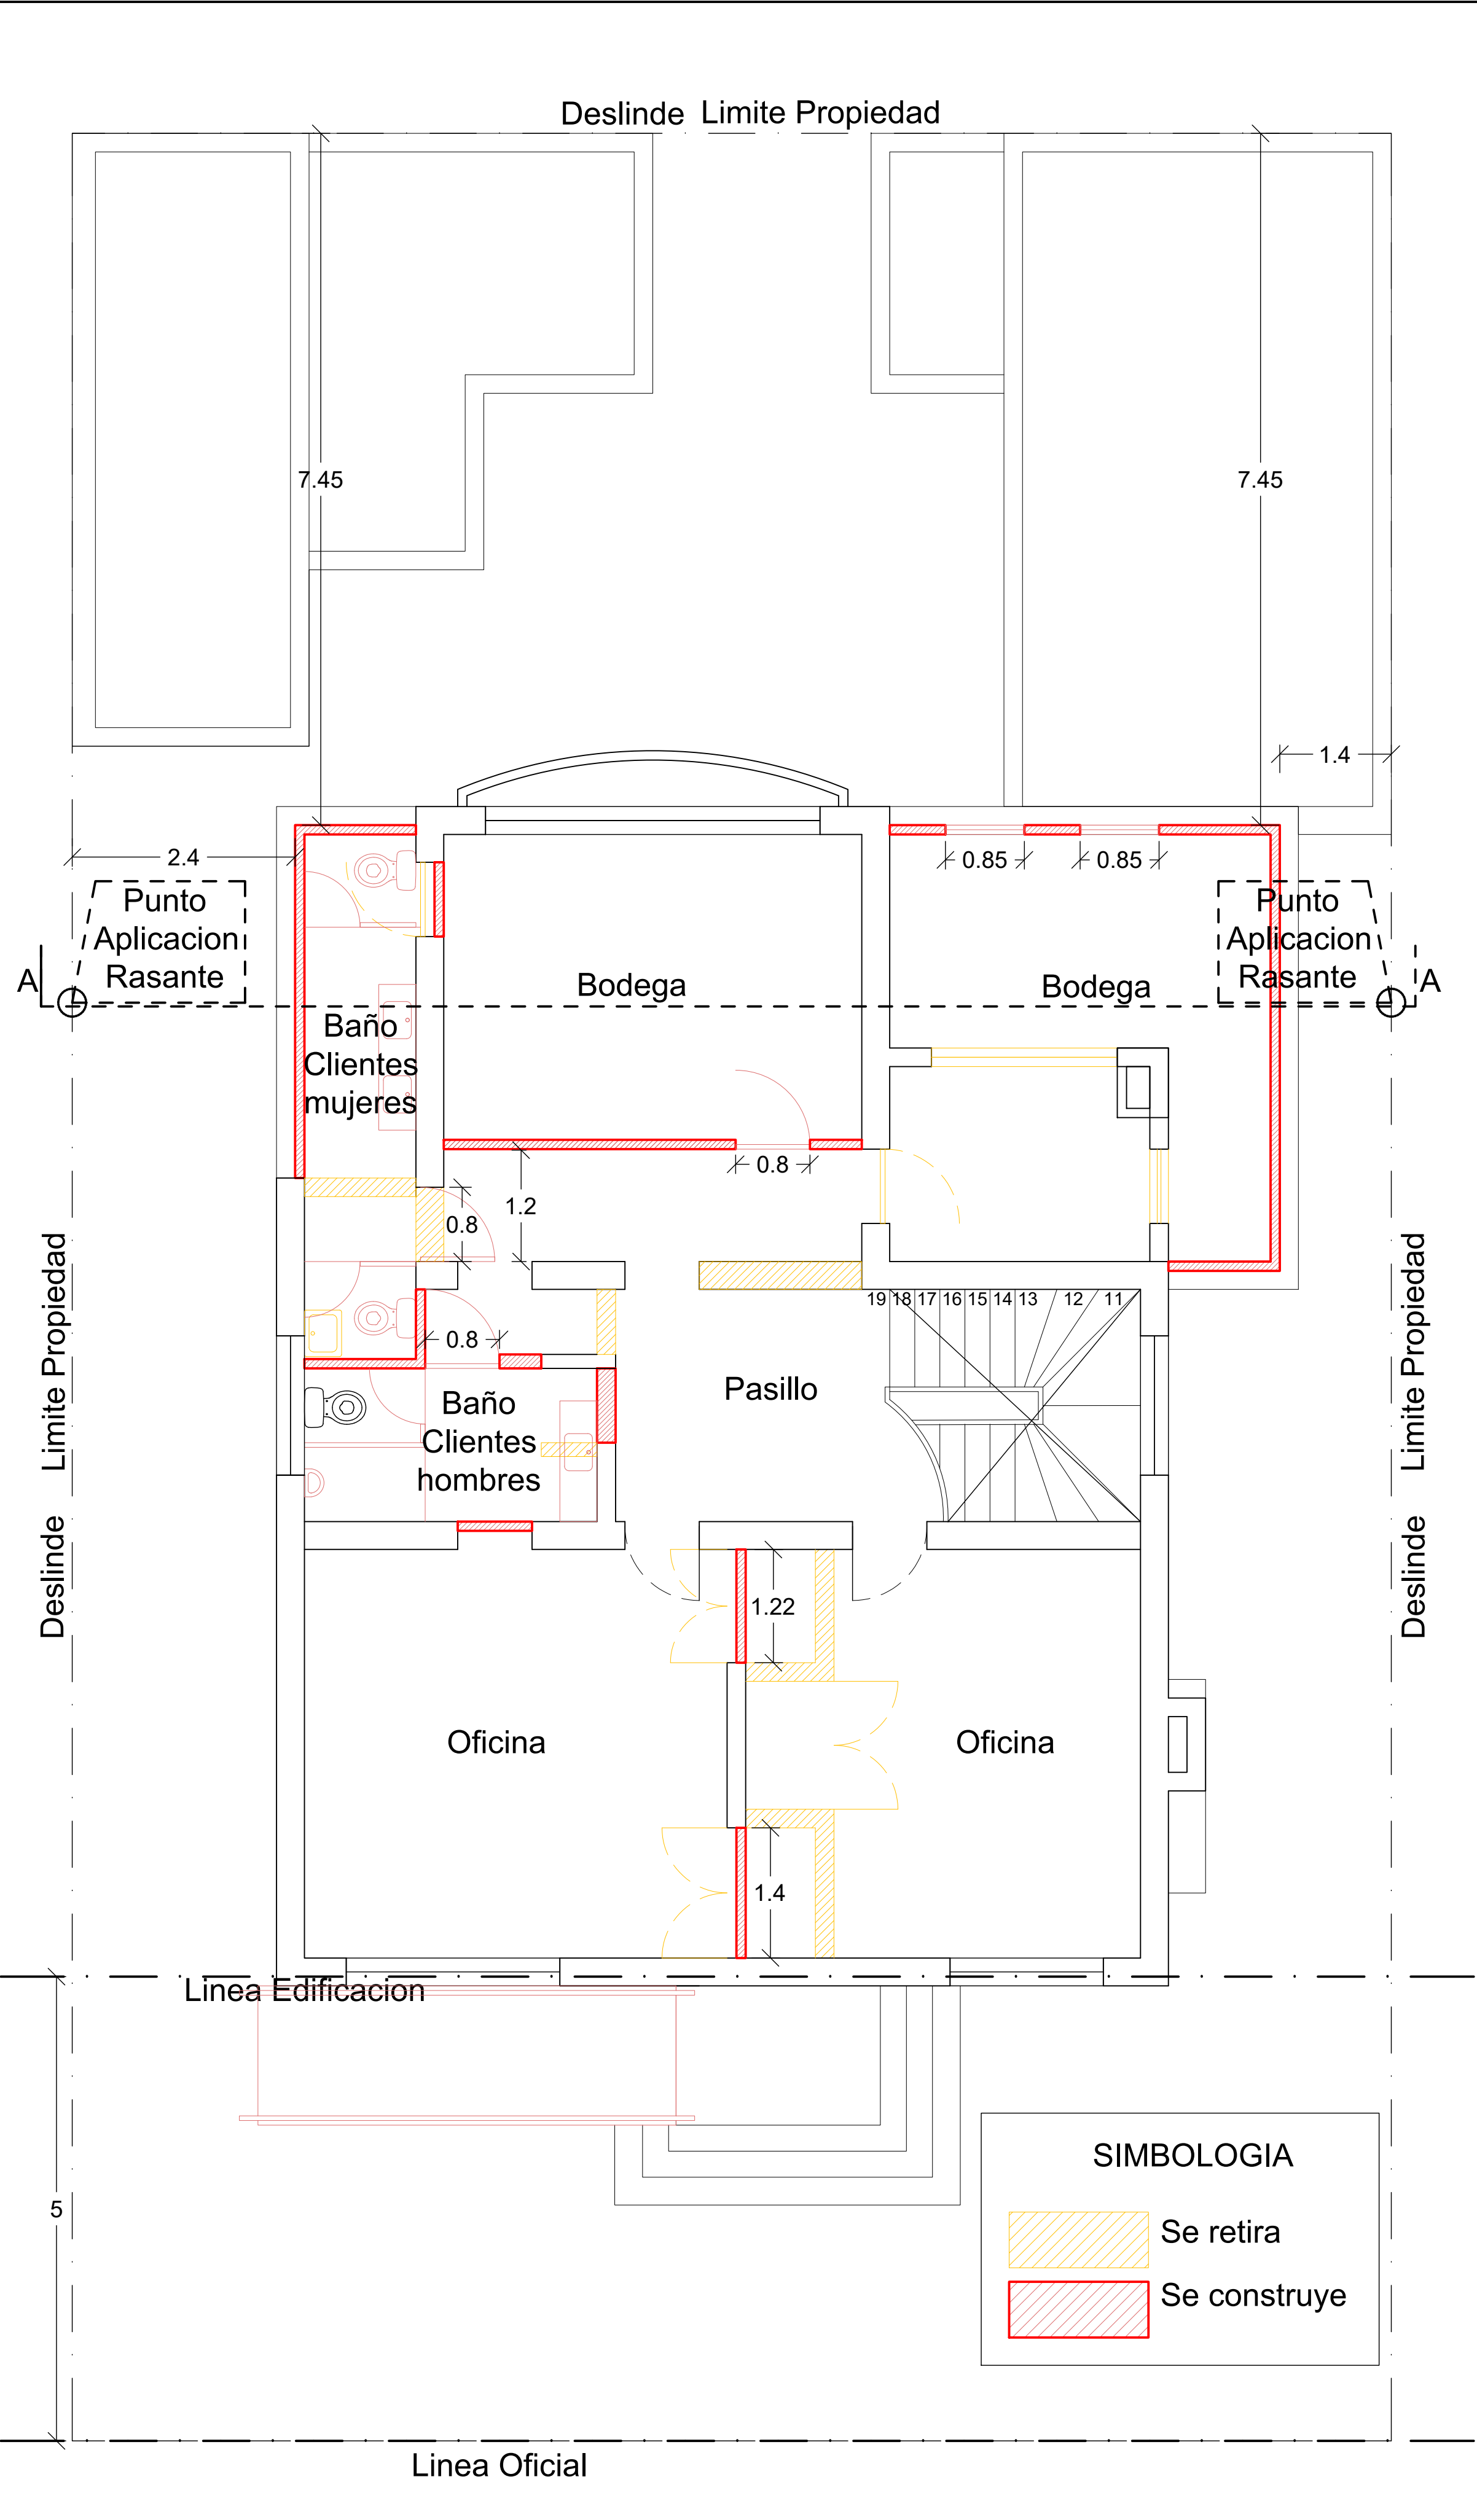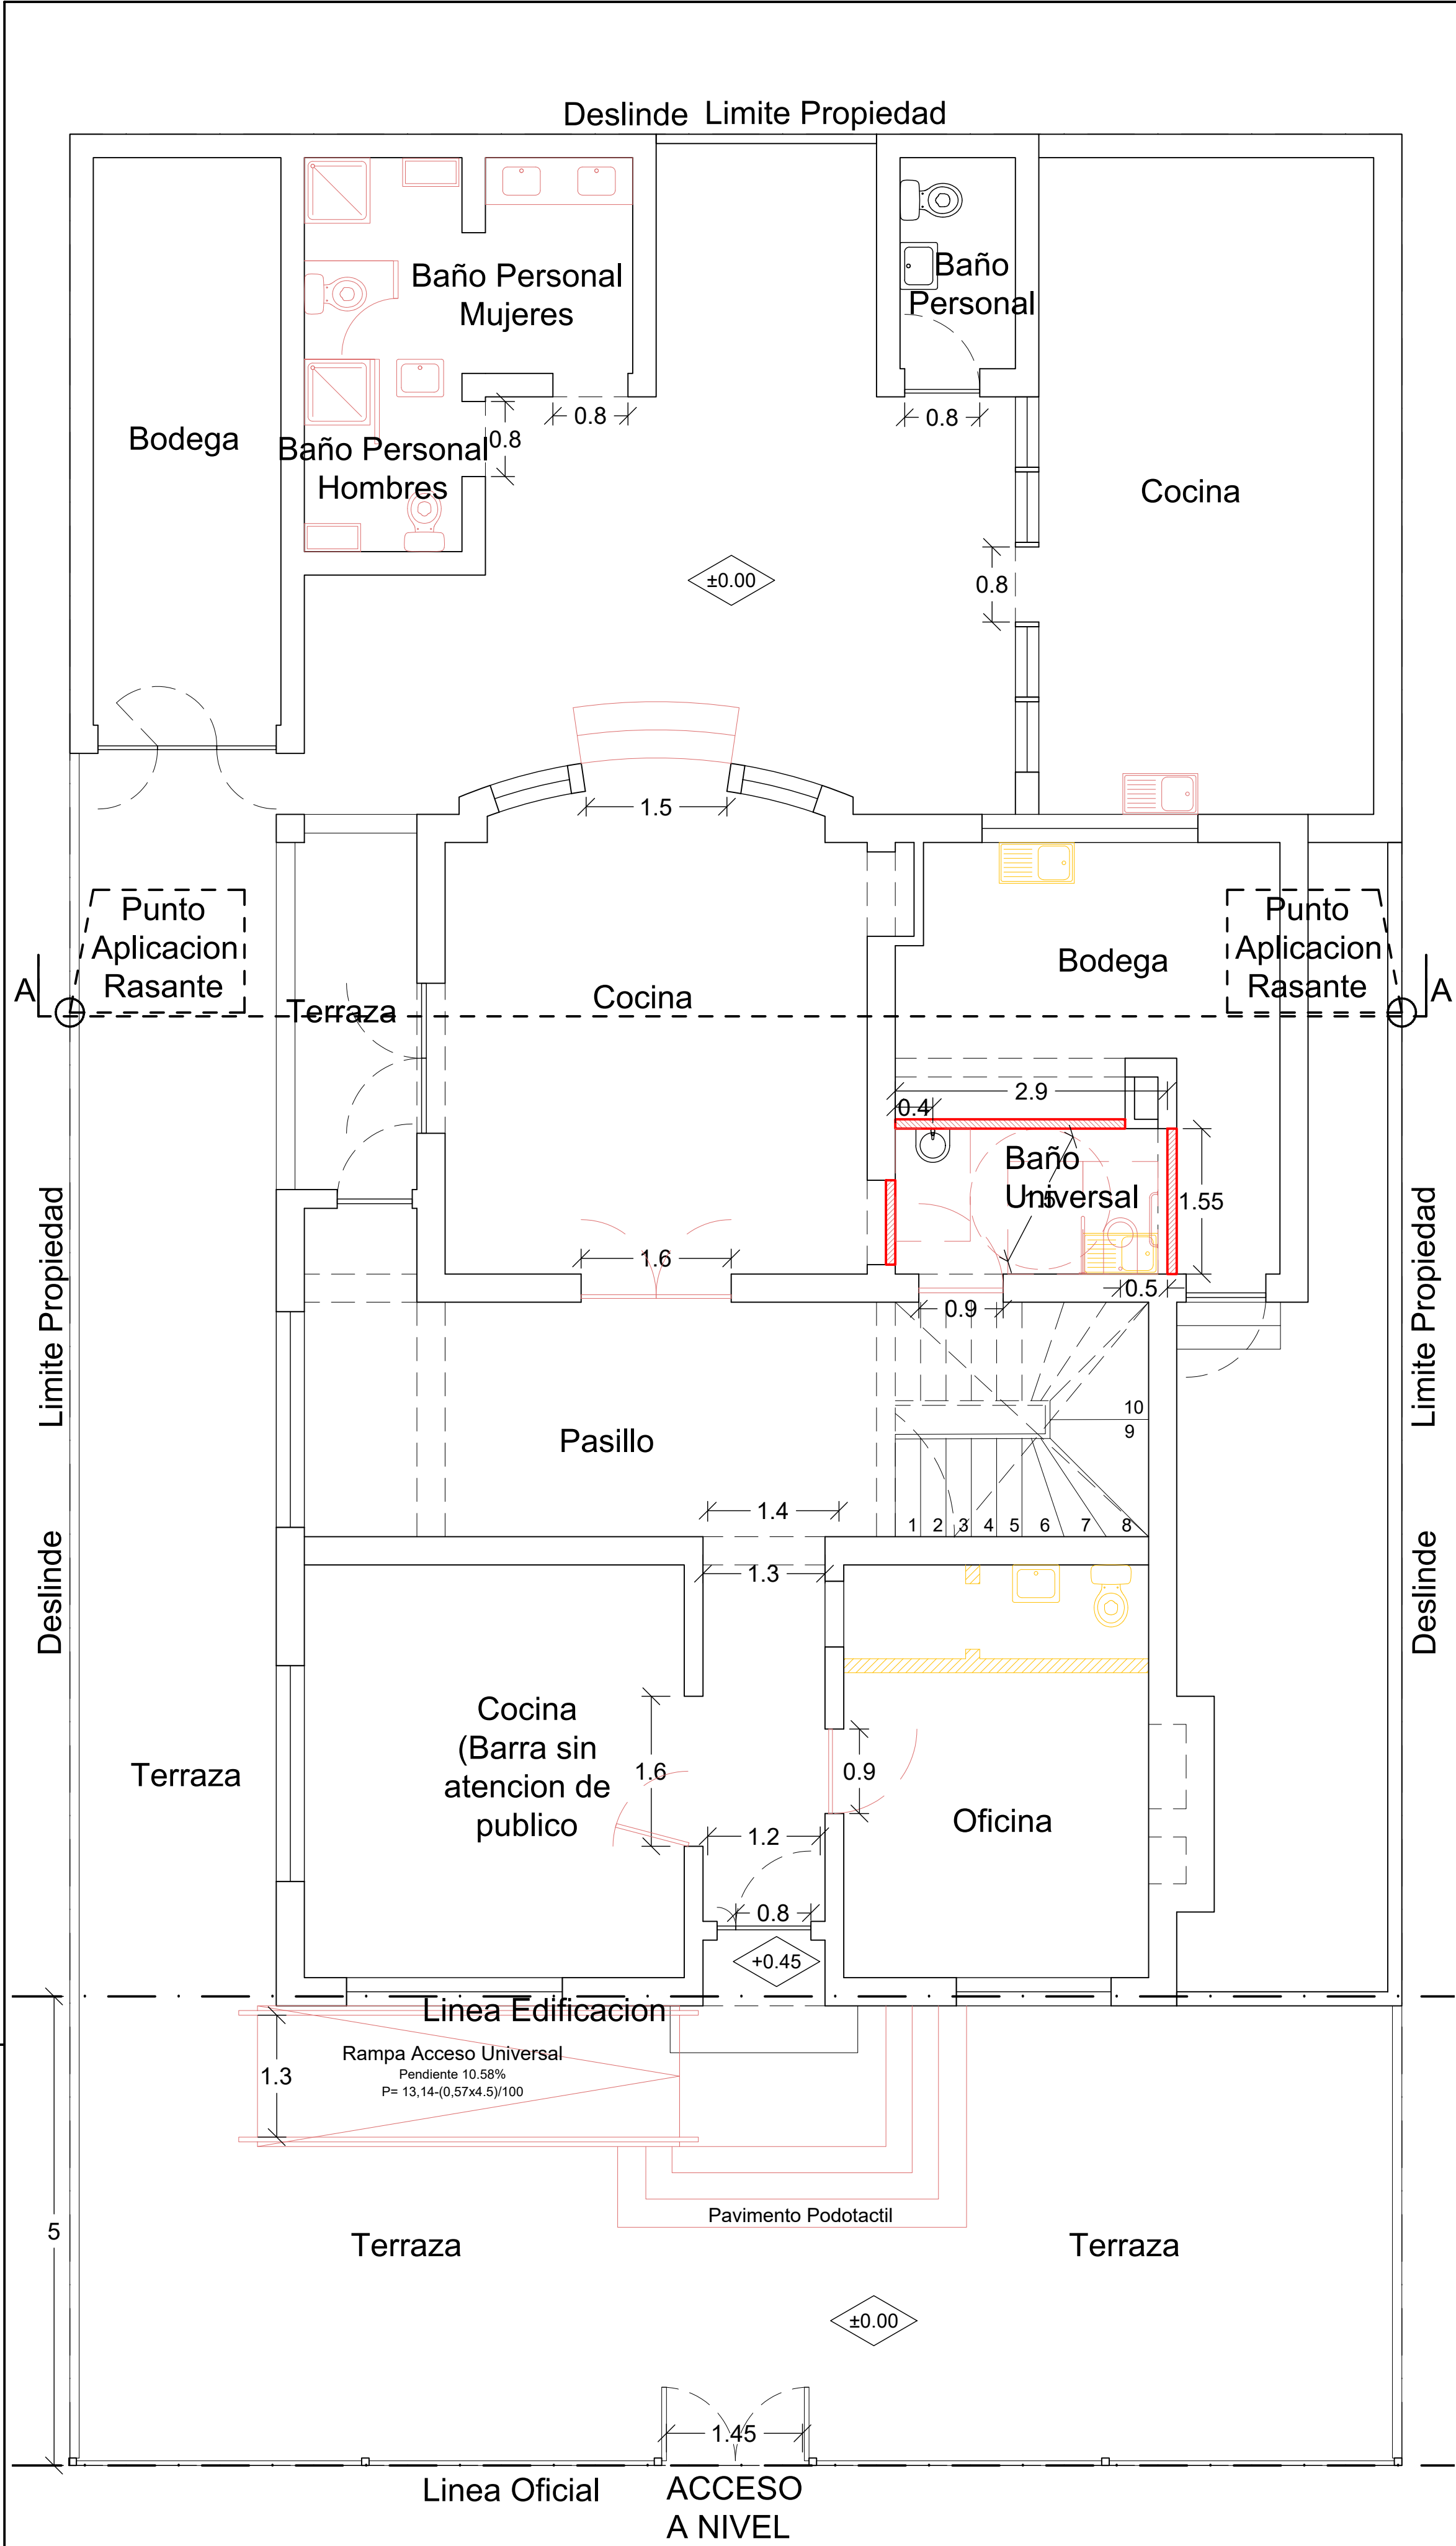


I. Municipalidad de Providencia	
Habilit. Rest. Plaza Pedro de Valdivia	
ASESORIAS E INVERSIONES CONCHALI LTDA Propietario	
Propietario: Asesorias e Inversiones Conchali Ltda RUT: 78.796.070-7	
Dirección: Plaza Pedro de Valdivia n°2025 Comuna: Providencia rol: 03228 - 012 Destino Solicitado: Restaurant	
Contenido: -Plano Situación Existente y Propuesta - Cuadro superficie Exis. y Propuesta	
Cristian Wrbka M. rol: 3-10885 Arquitecto cwrbka@eleconsultores.cl	2/4

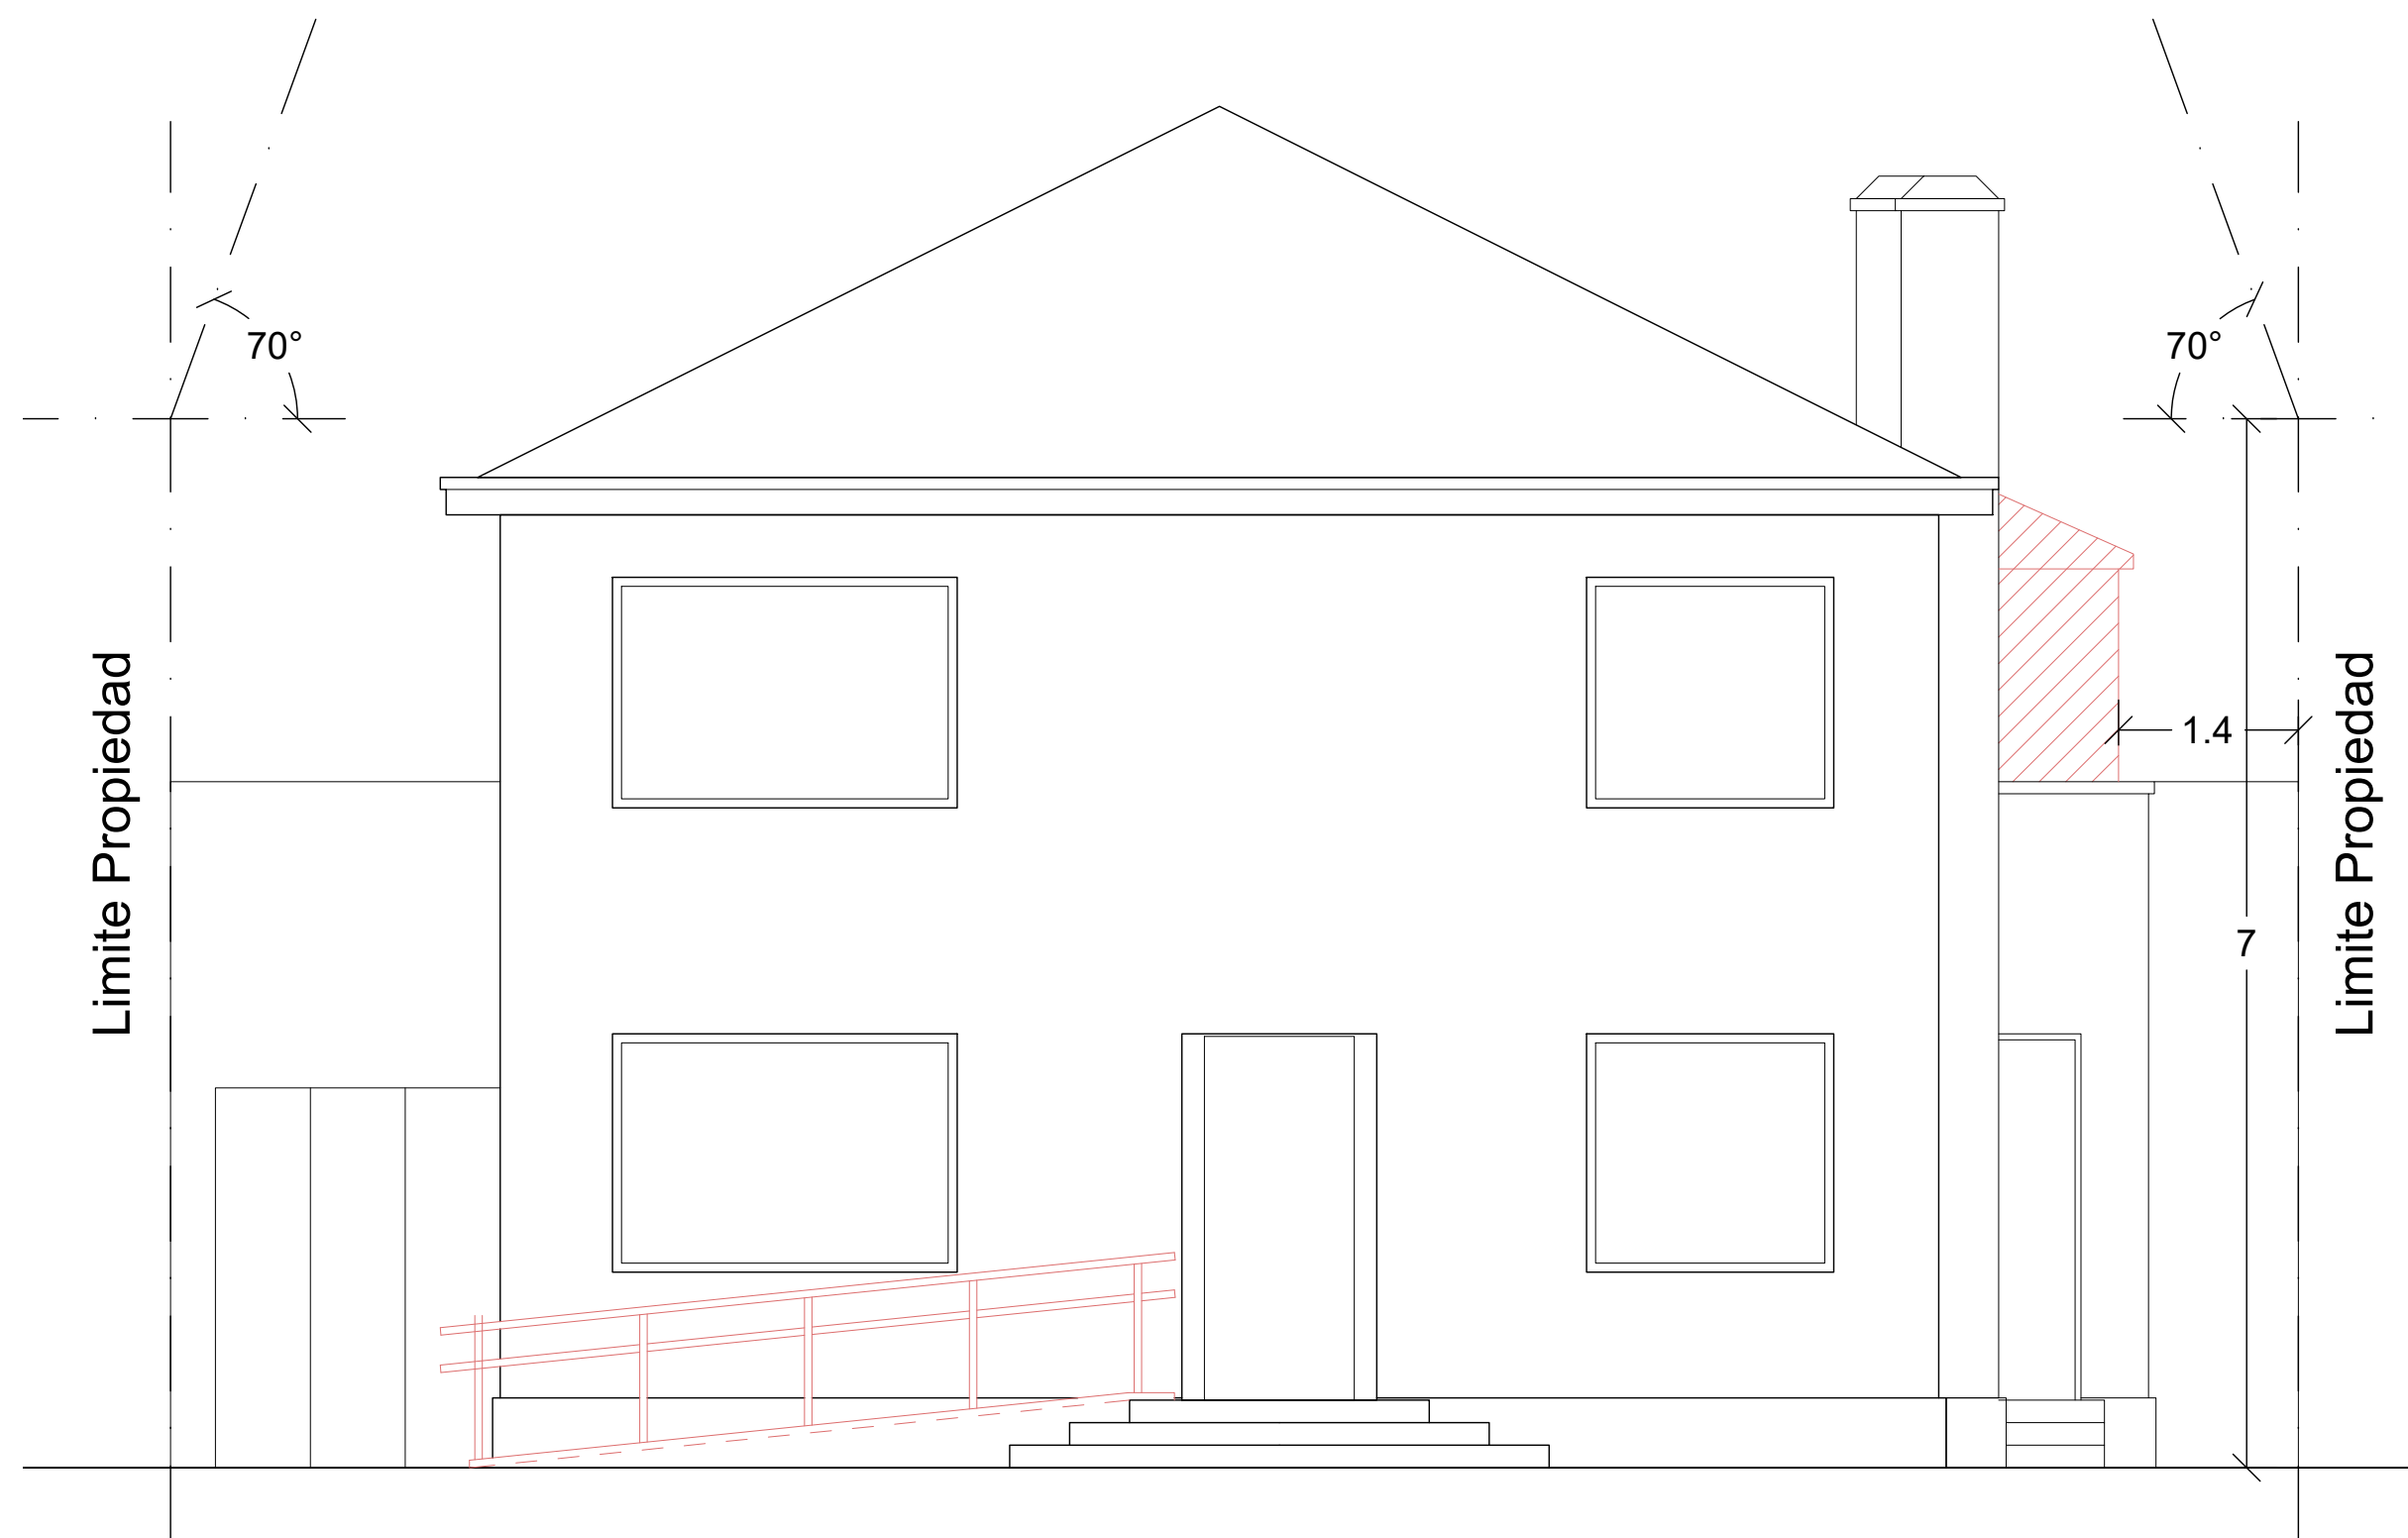


Elevación Norte
Esc. 1:50

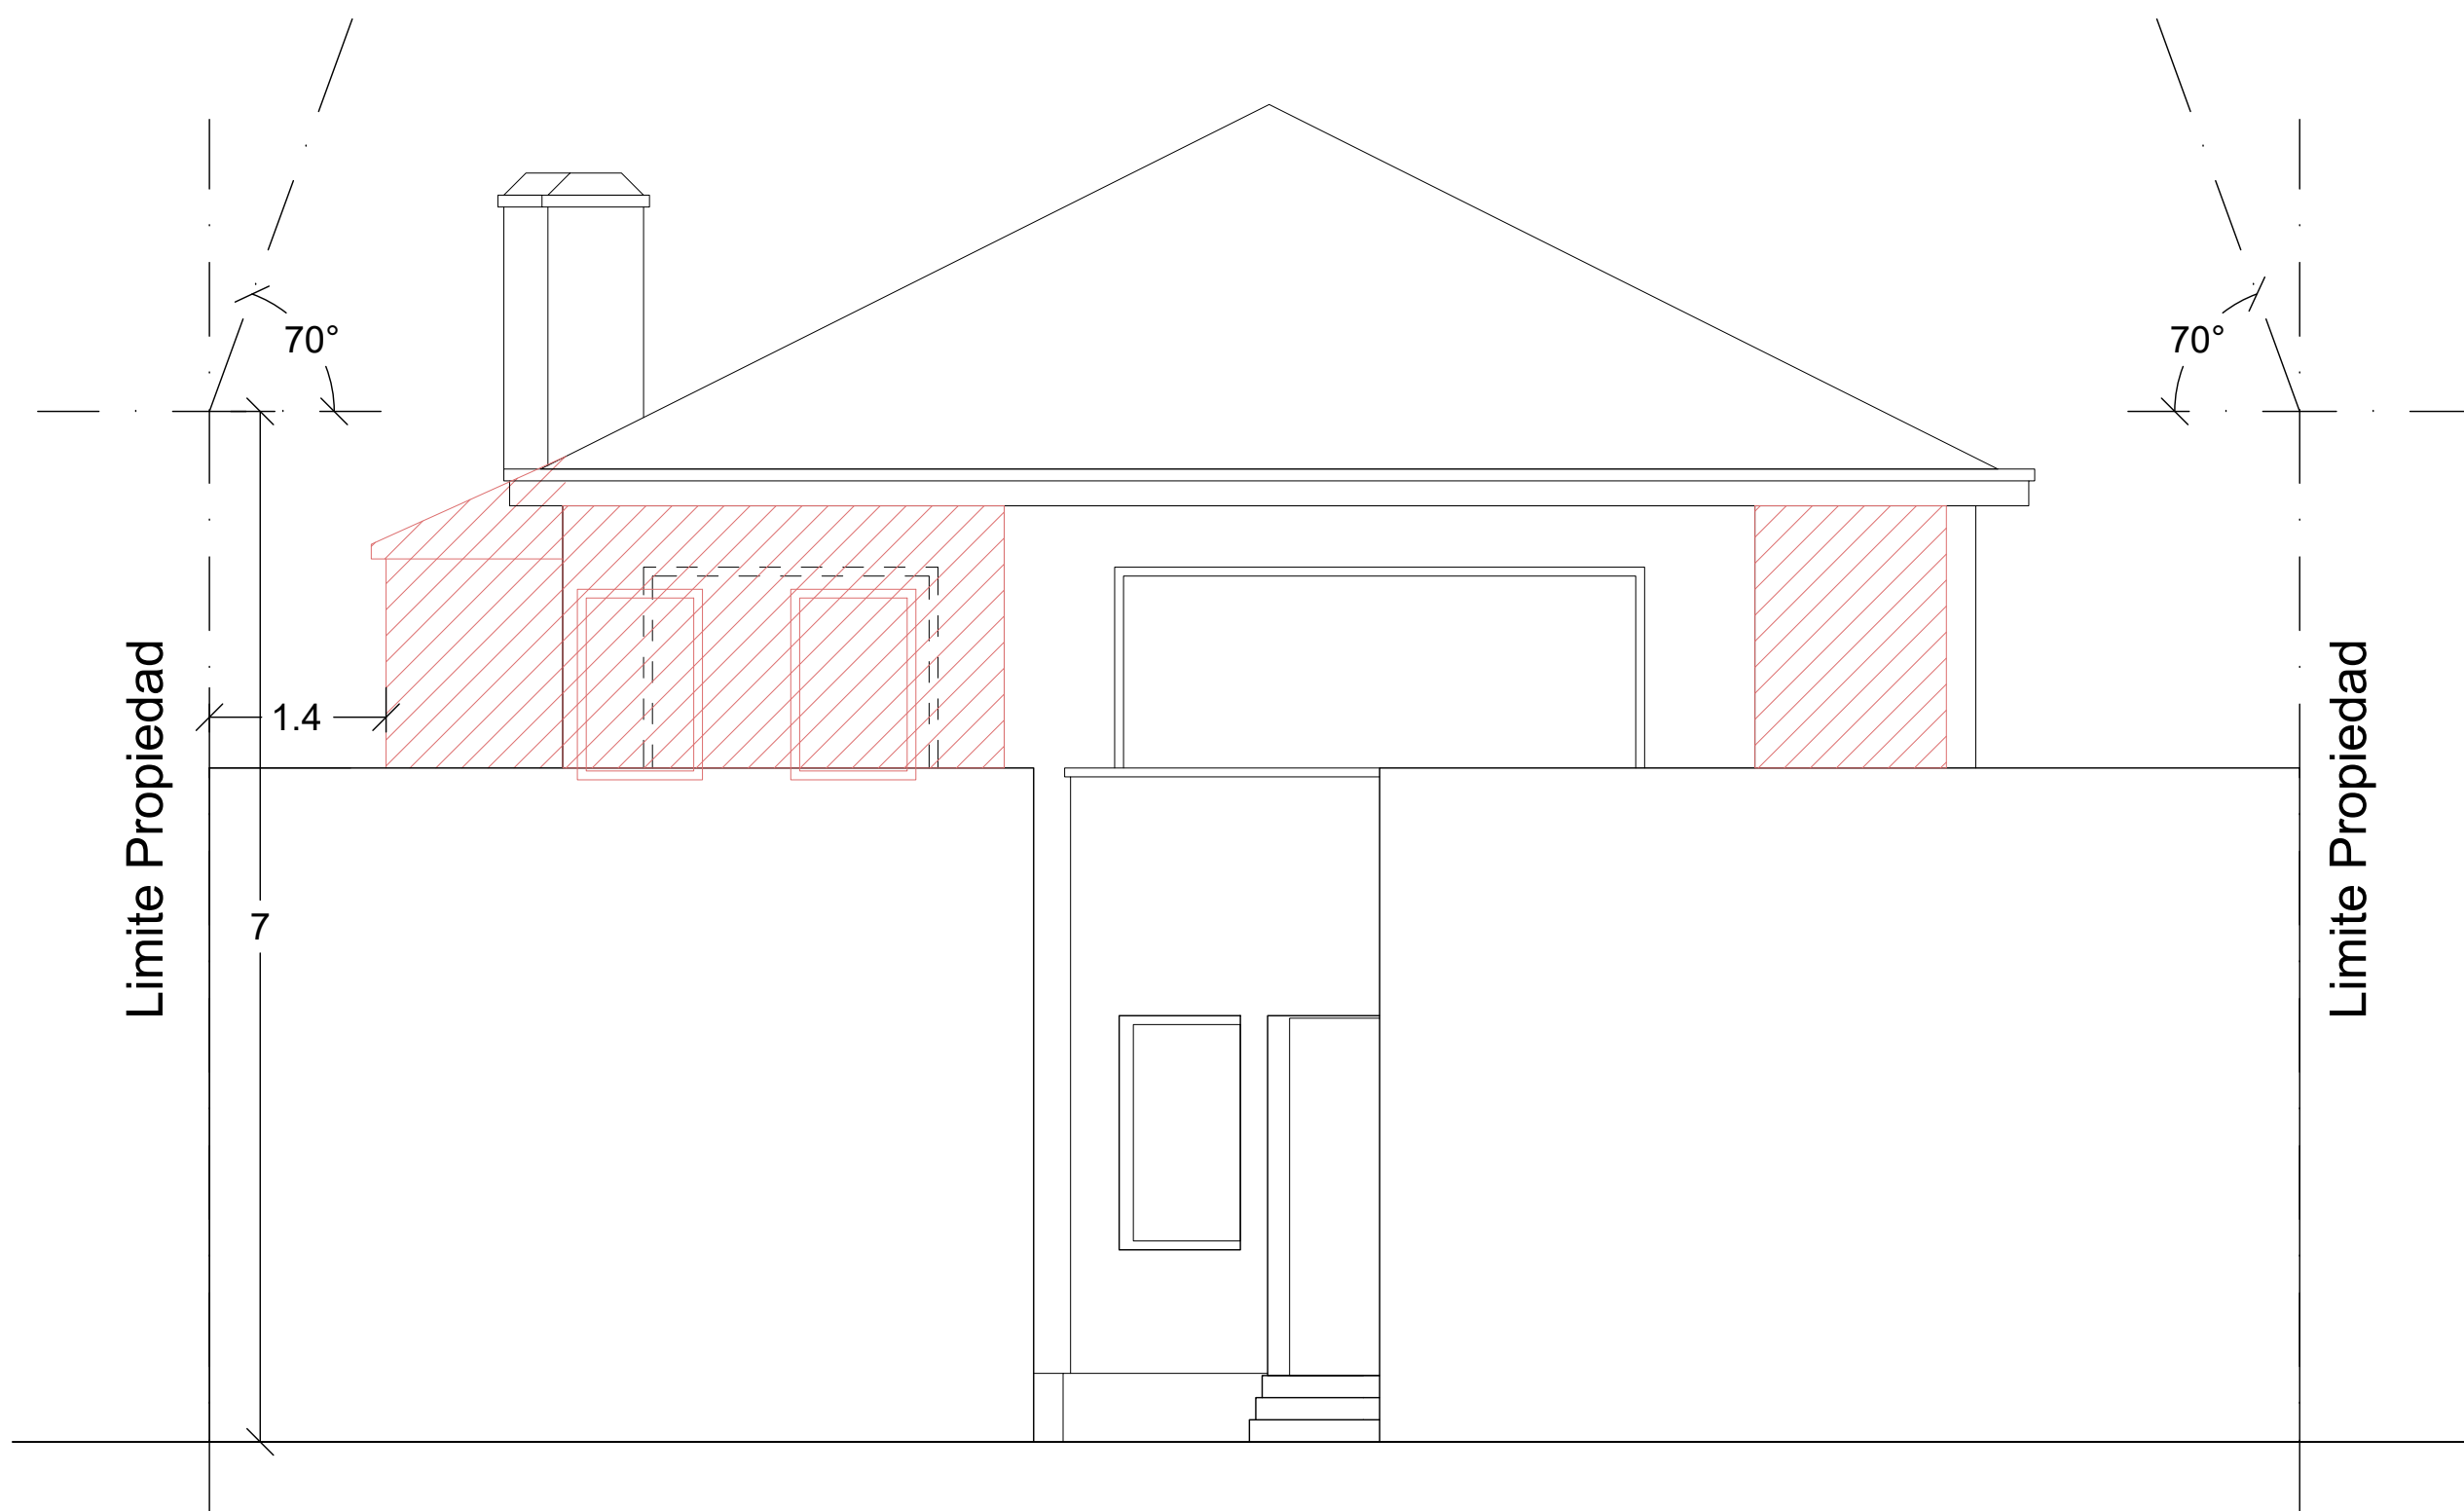

Elevación Sur
Esc. 1:50

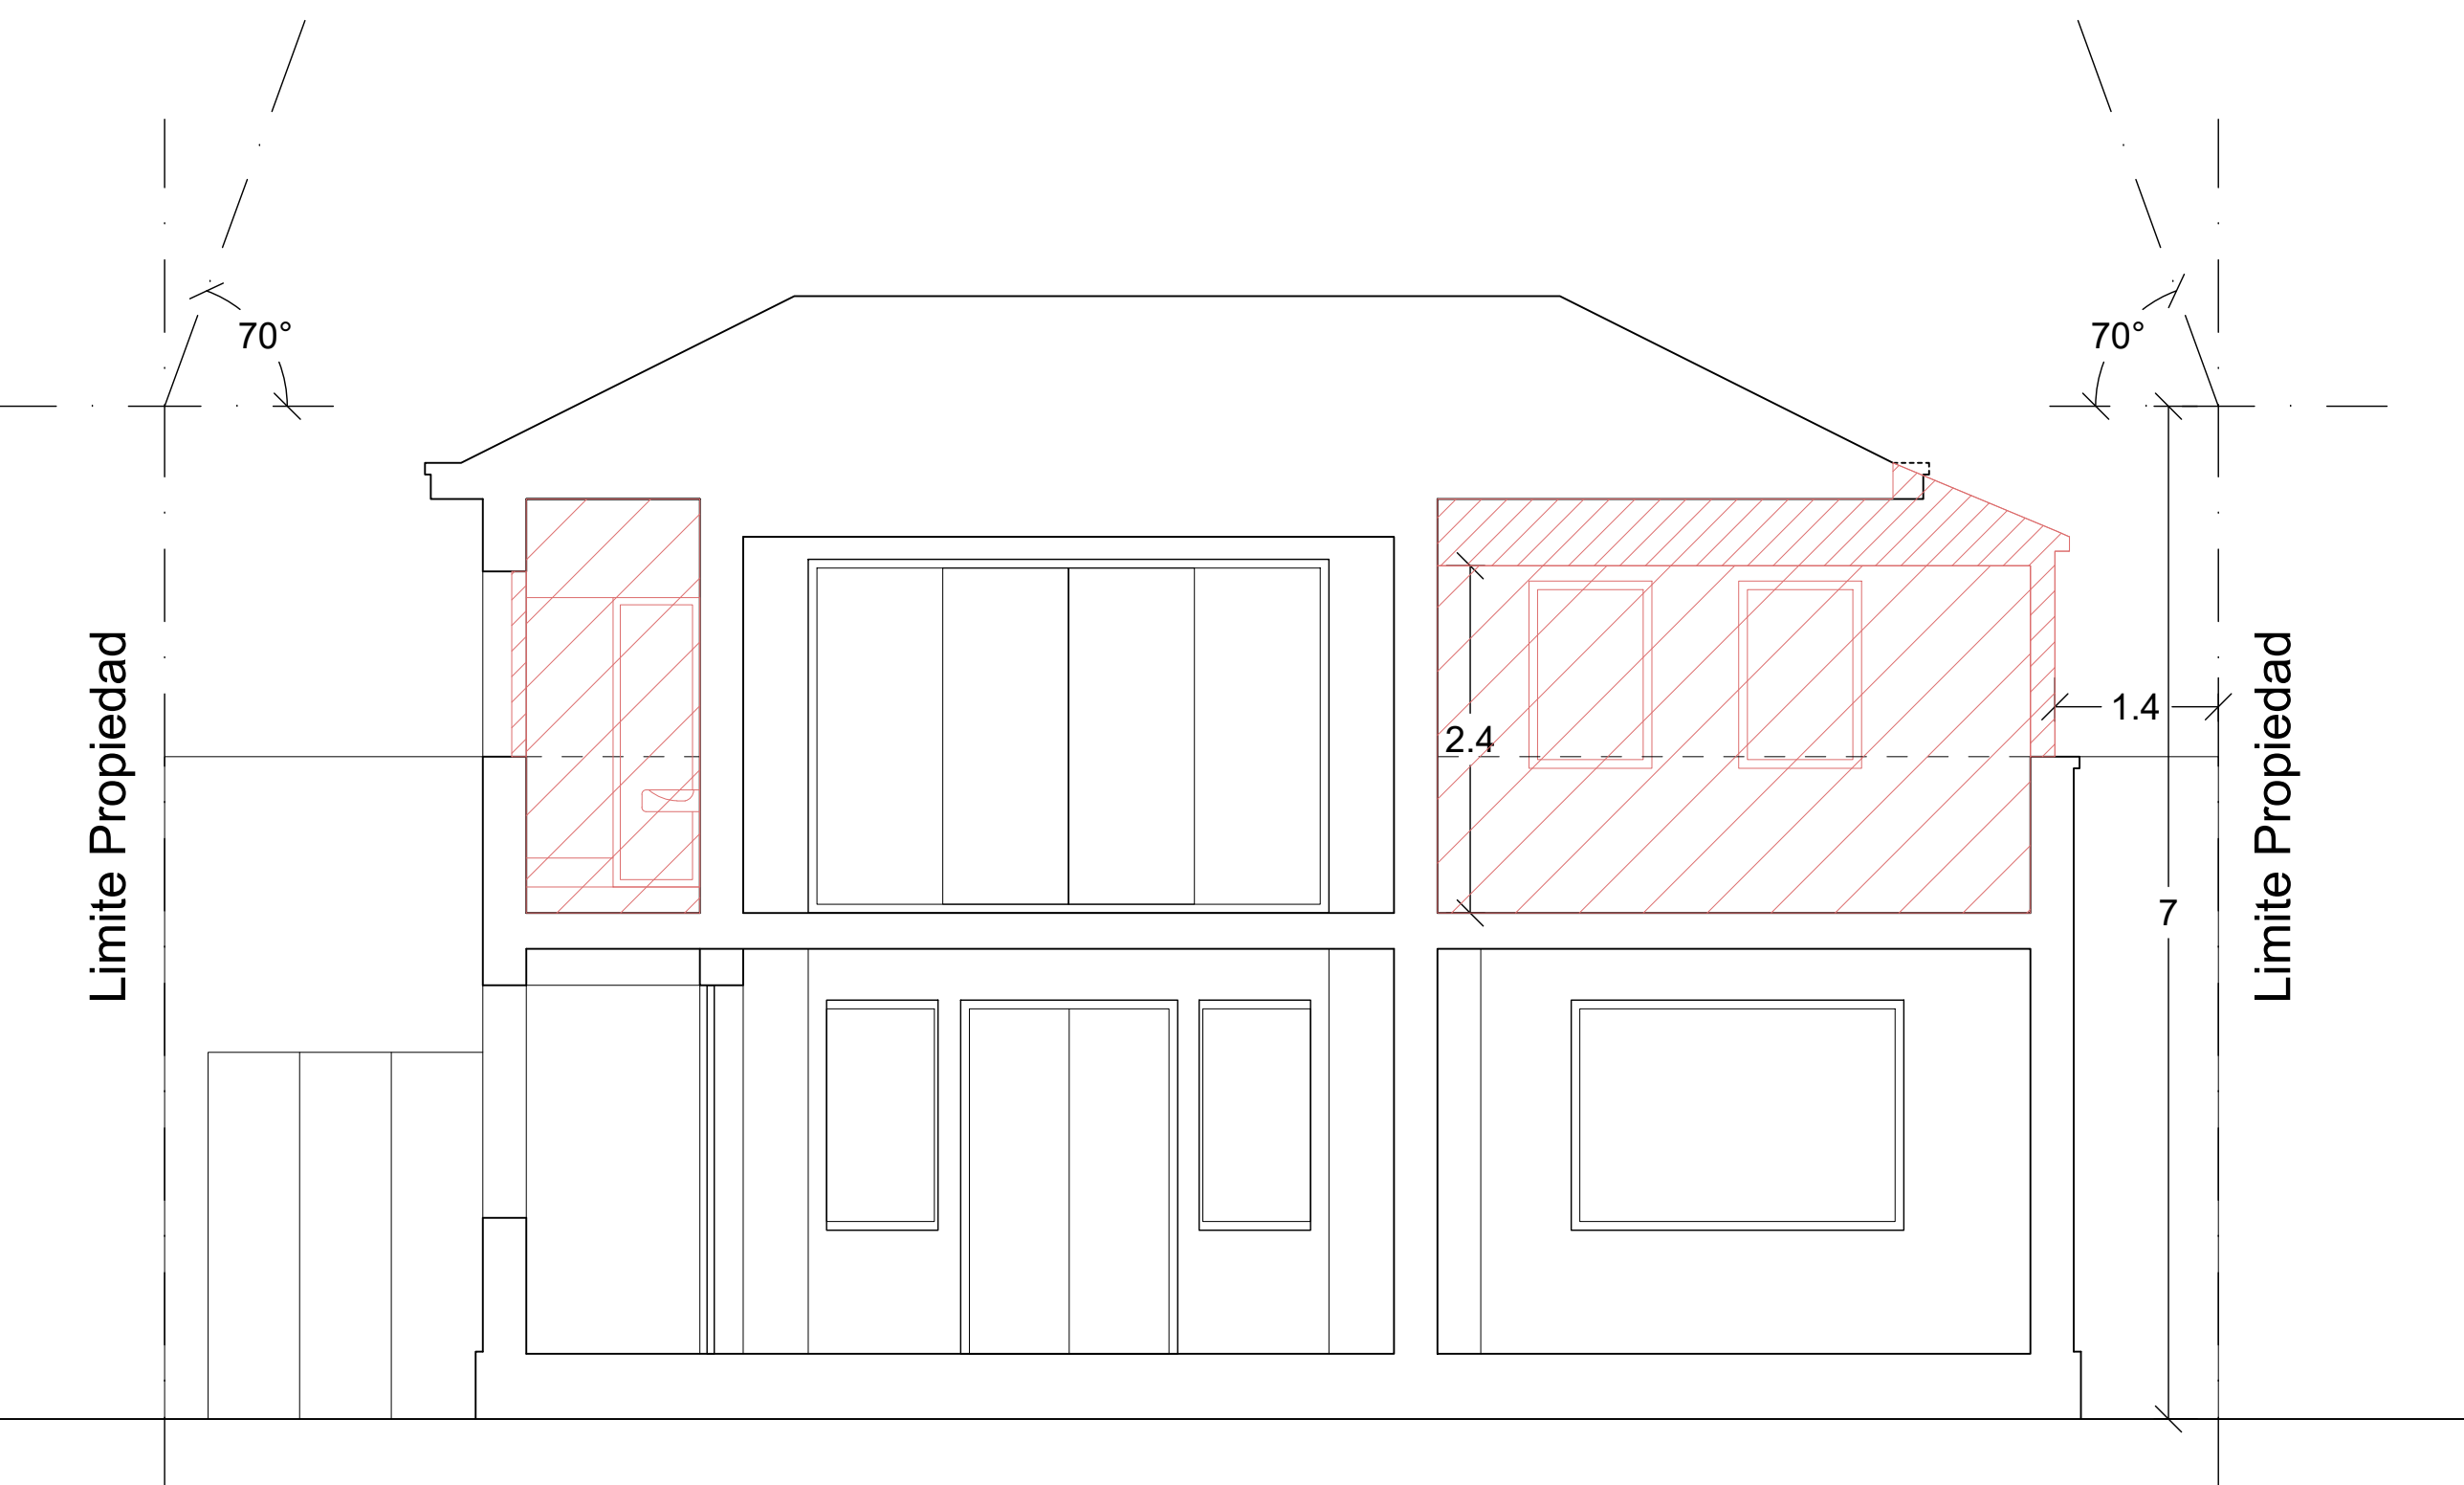


Corte A-A
Esc. 1:50

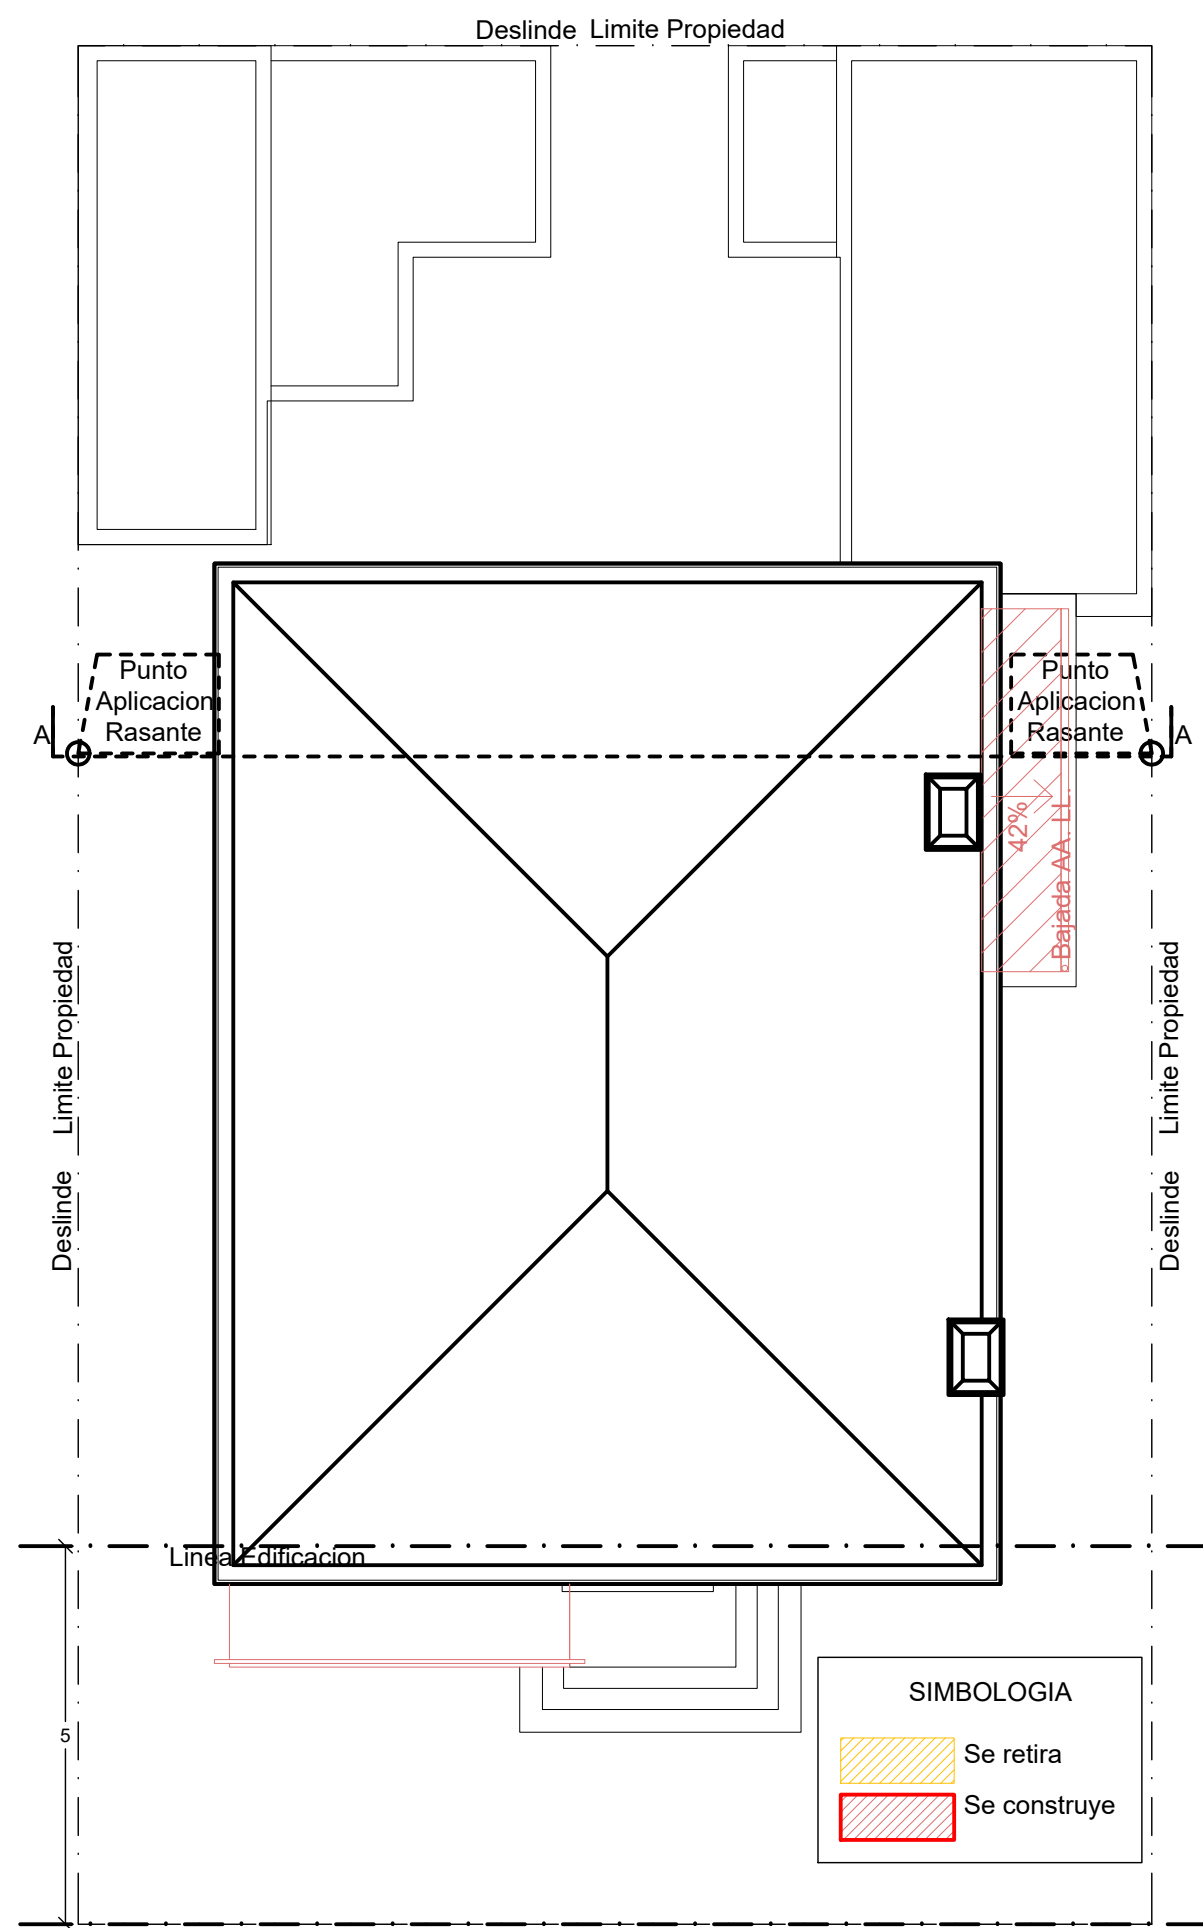


Situación Propuesta Cubiertas
Esc. 1:100

I. Municipalidad de Providencia		
Habilit. Rest. Plaza Pedro de Valdivia		
ASESORIAS E INVERSIONES CONCHALI LTDA Propietario		
Propietario: Asesorias e Inversiones Conchali Ltda RUT: 78.796.070-7		
Dirección: Plaza Pedro de Valdivia n°2025 Comuna: Providencia rol: 03228 - 012 Destino Solicitado: Restaurant		
Contenido: -Elevaciones Norte y Sur - Corte A-A - Planta de Cubiertas		
Cristian Wrbka M. rol: 3-10885 Arquitecto cwrbka@eleconsultores.cl		3/4

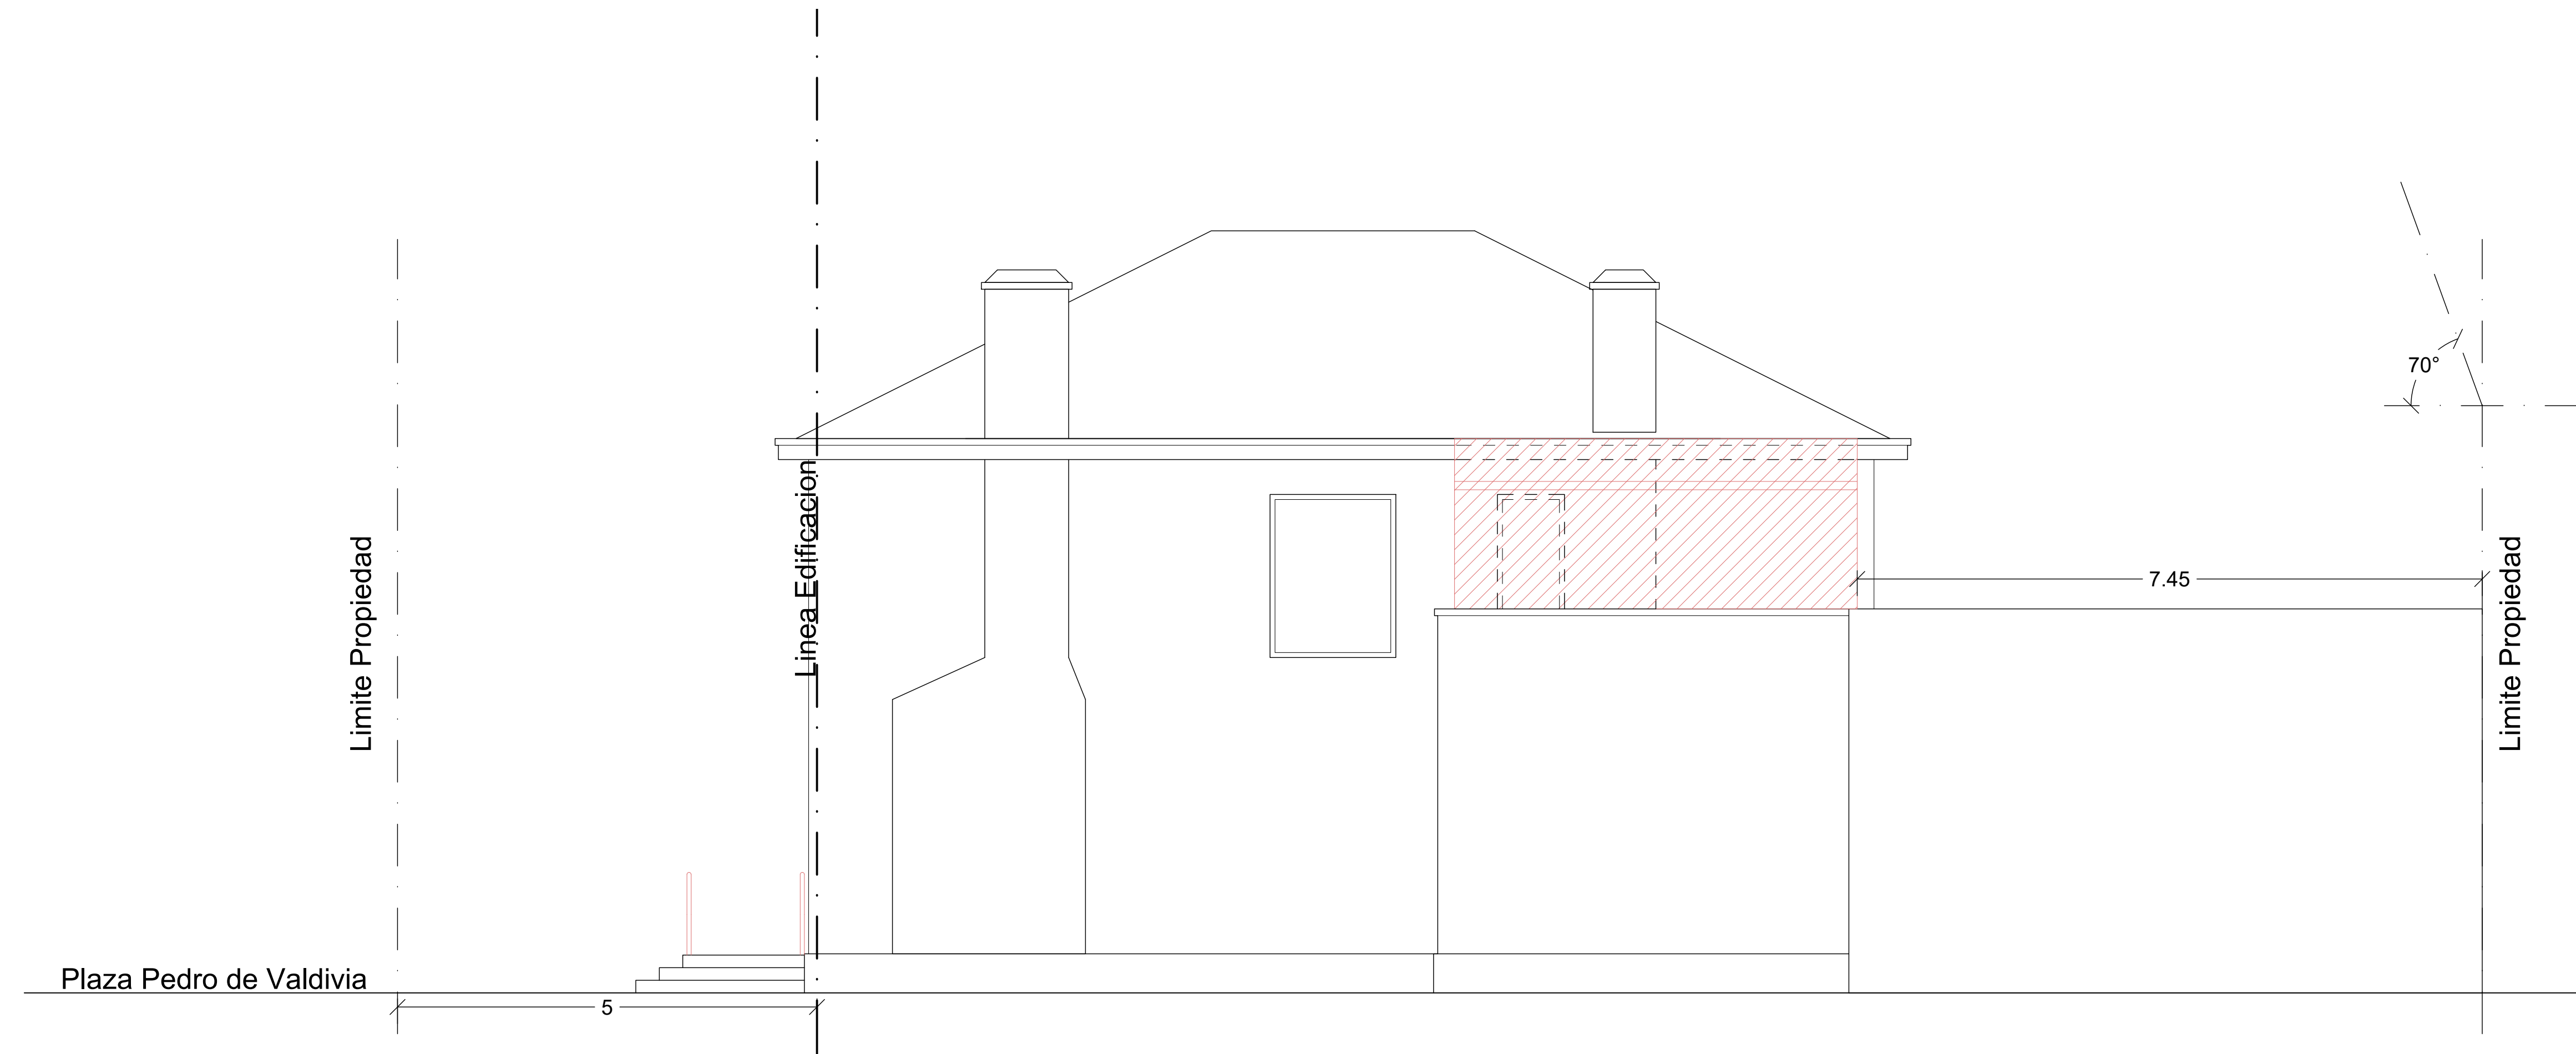

Elevación Oeste
Esc. 1:50

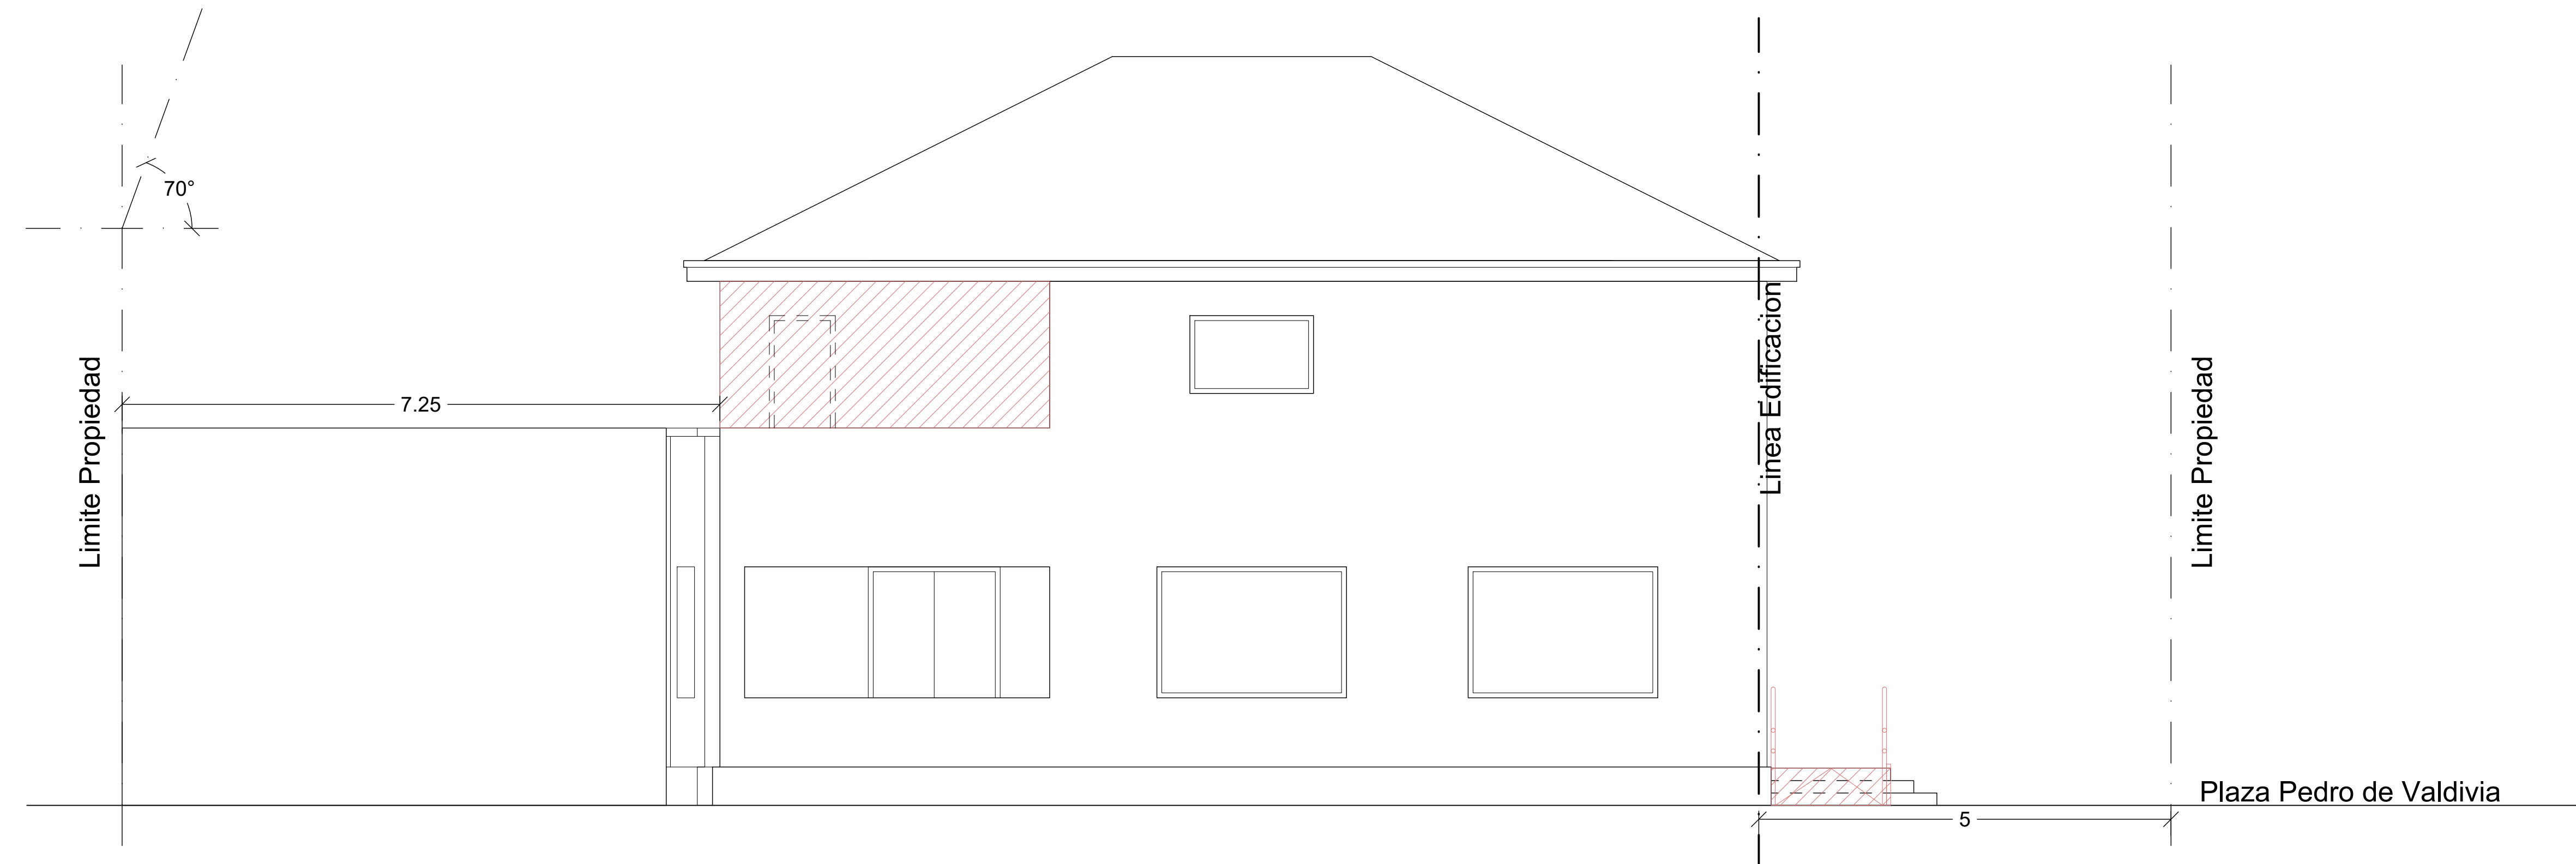

Elevación Este
Esc. 1:50

I. Municipalidad de Providencia		
Habilit. Rest. Plaza Pedro de Valdivia		
ASESORIAS E INVERSIONES CONCHALI LTDA Propietario		
Propietario: Asesorias e Inversiones Conchali Ltda RUT: 78.796.070-7		
Dirección: Plaza Pedro de Valdivia n°:2025 Comuna: Providencia rol: 03228 - 012 Destino Solicitado: Restaurant		
Contenido: -Elevaciones Este y Oeste		
Cristian Wrbka M. rol: 3-10885 Arquitecto cwrbka@eieconsultores.cl		4/4