




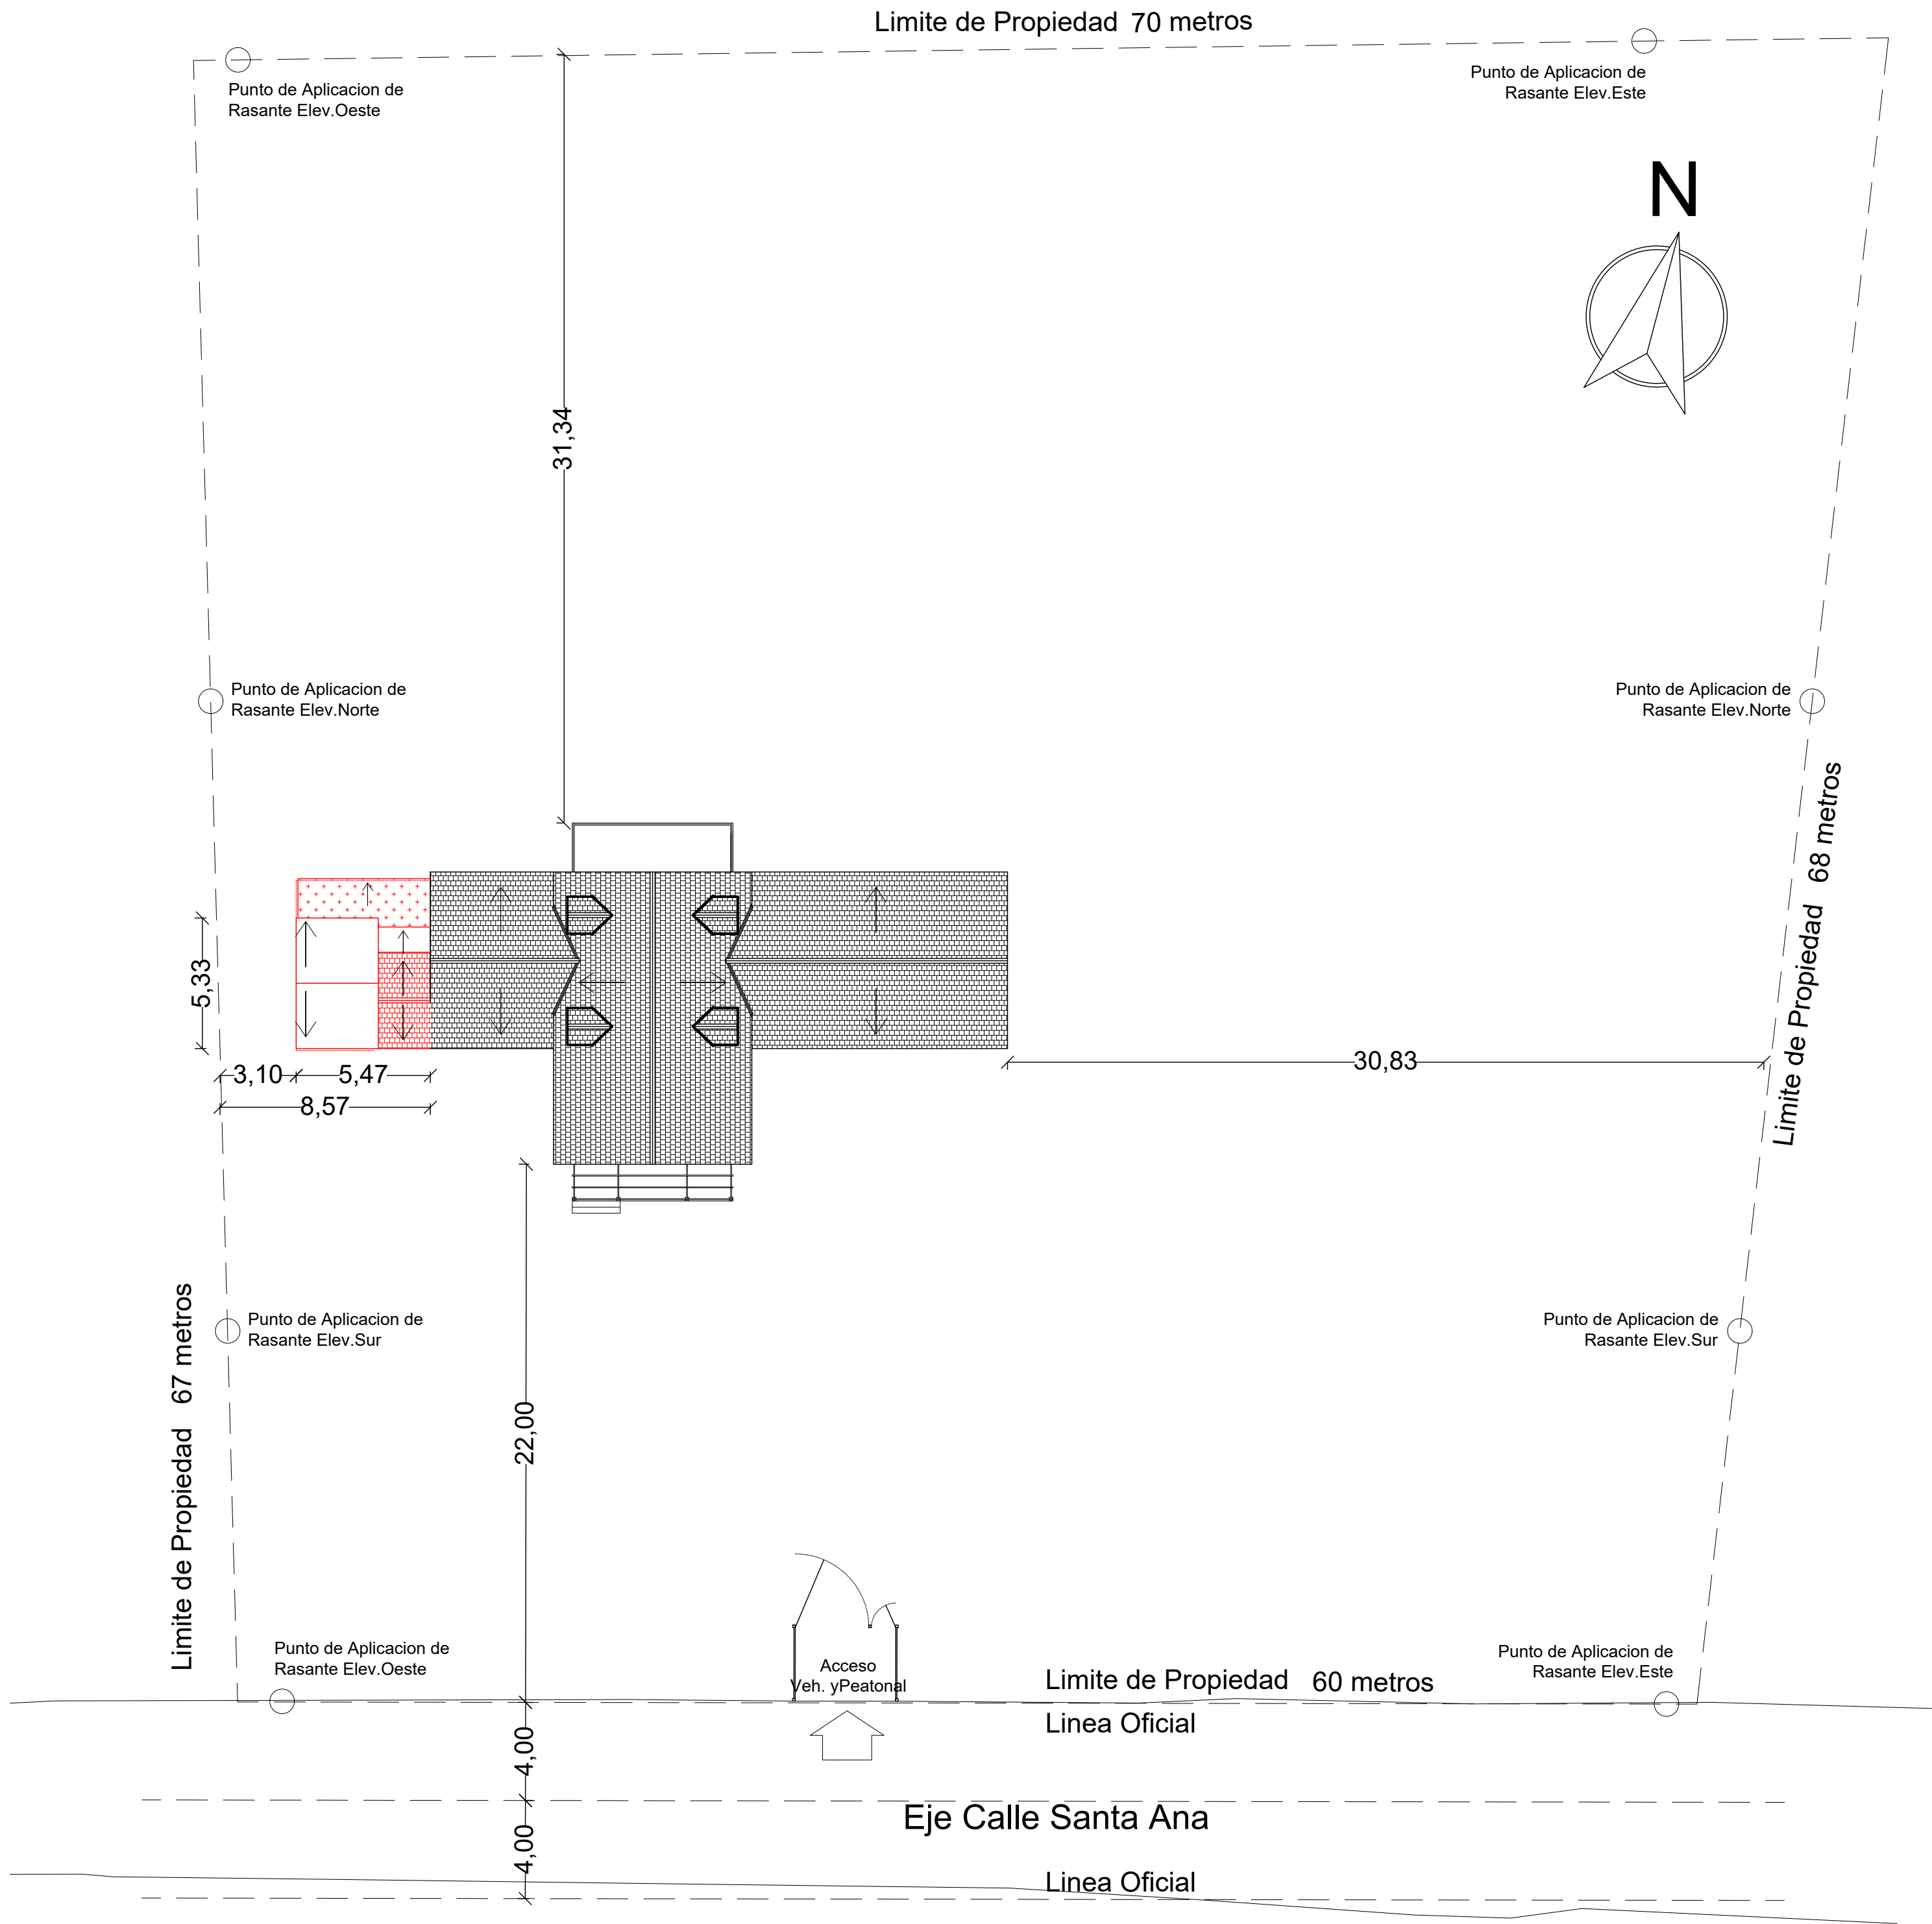


Planta Emplazamiento
Esc 1:200


Elevación General Sur
Esc 1:200

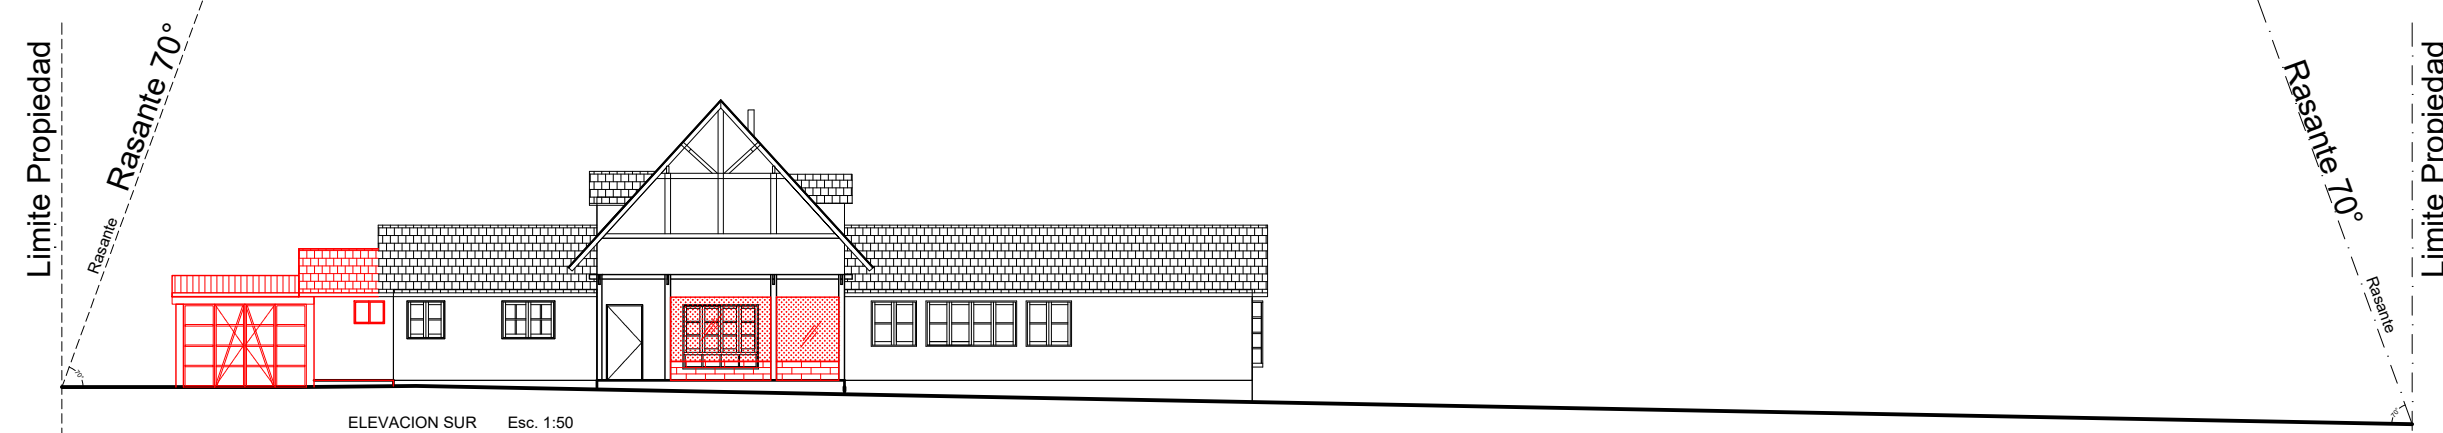

Elevación General Poniente
Esc 1:200

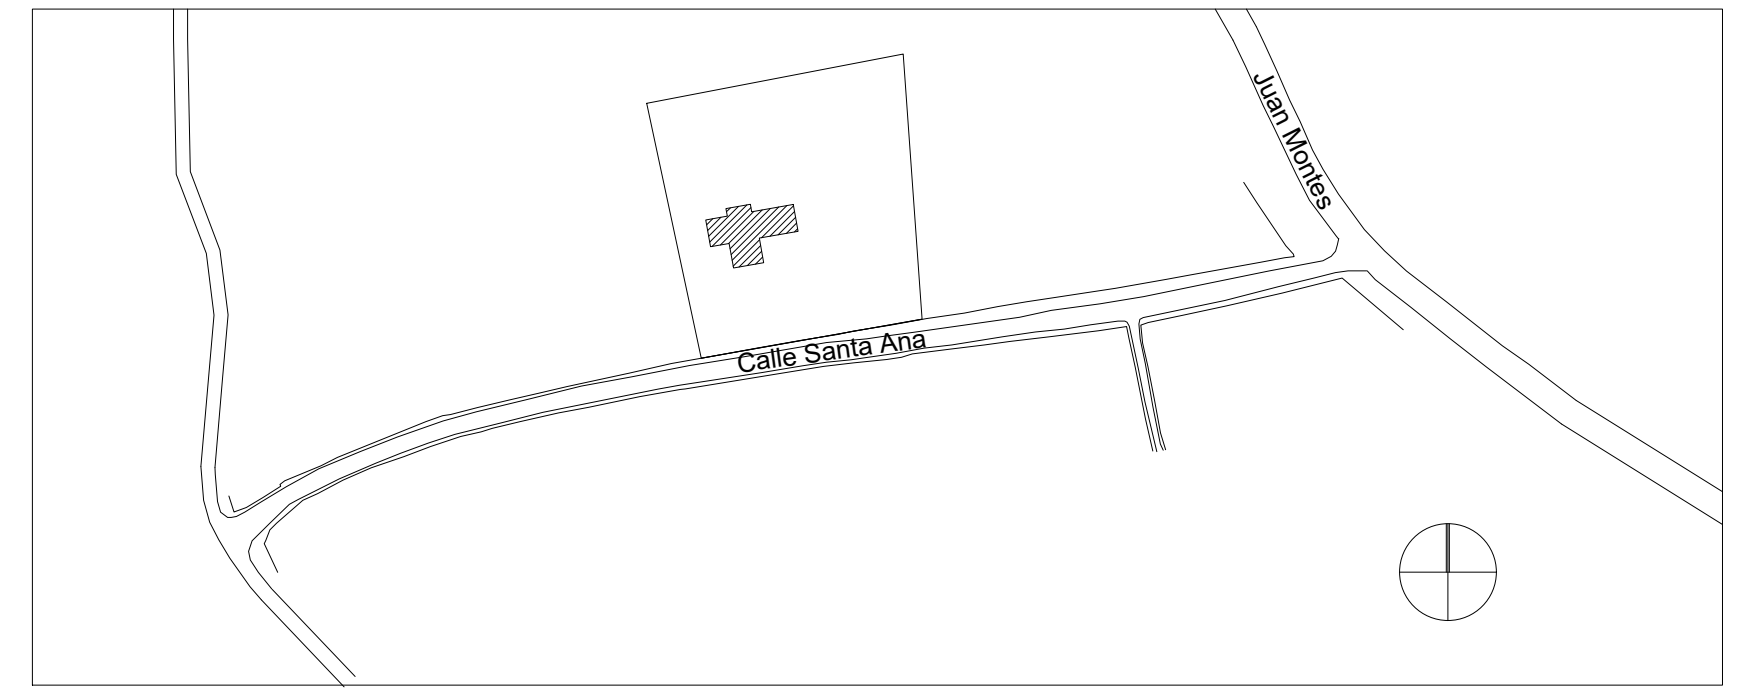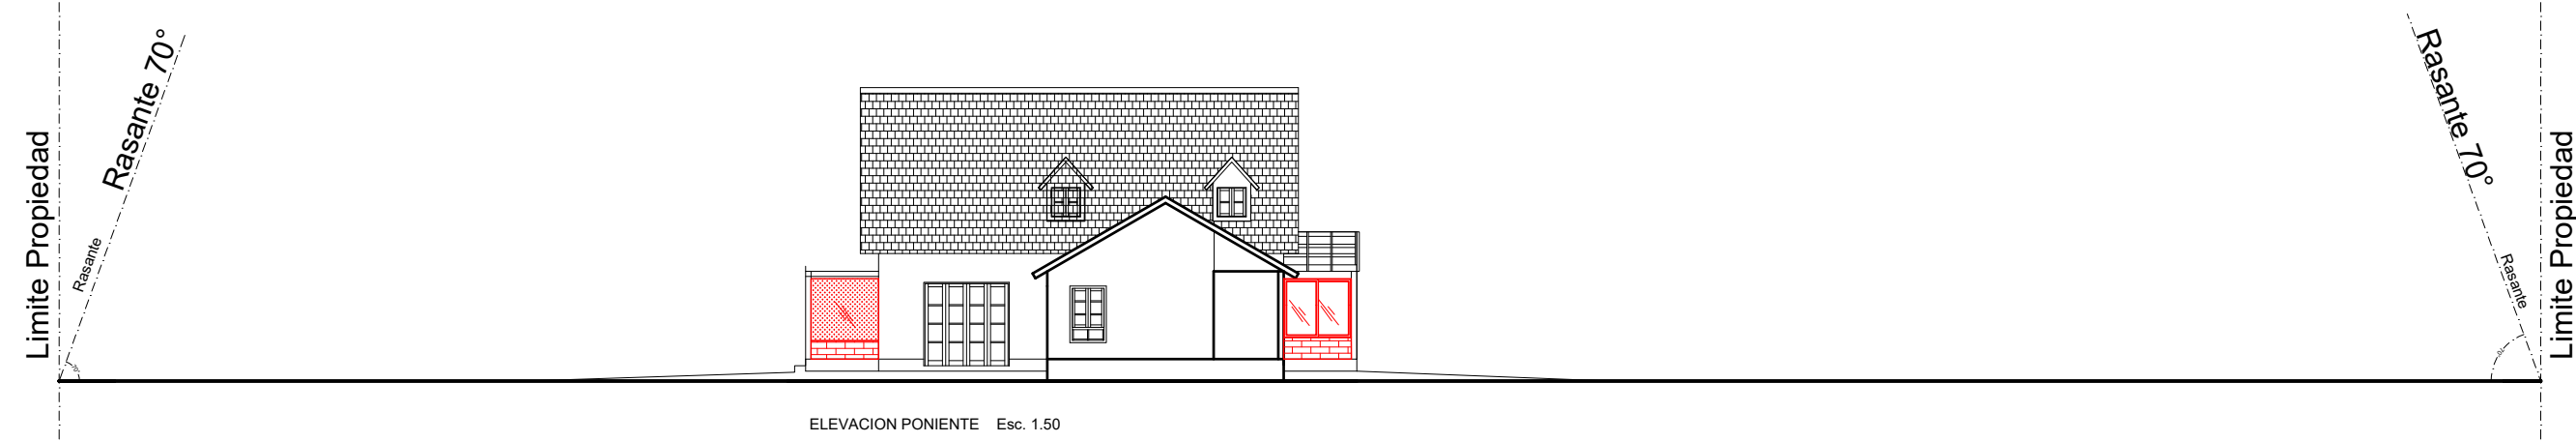

Plano Ubicación
Esc 1:2000

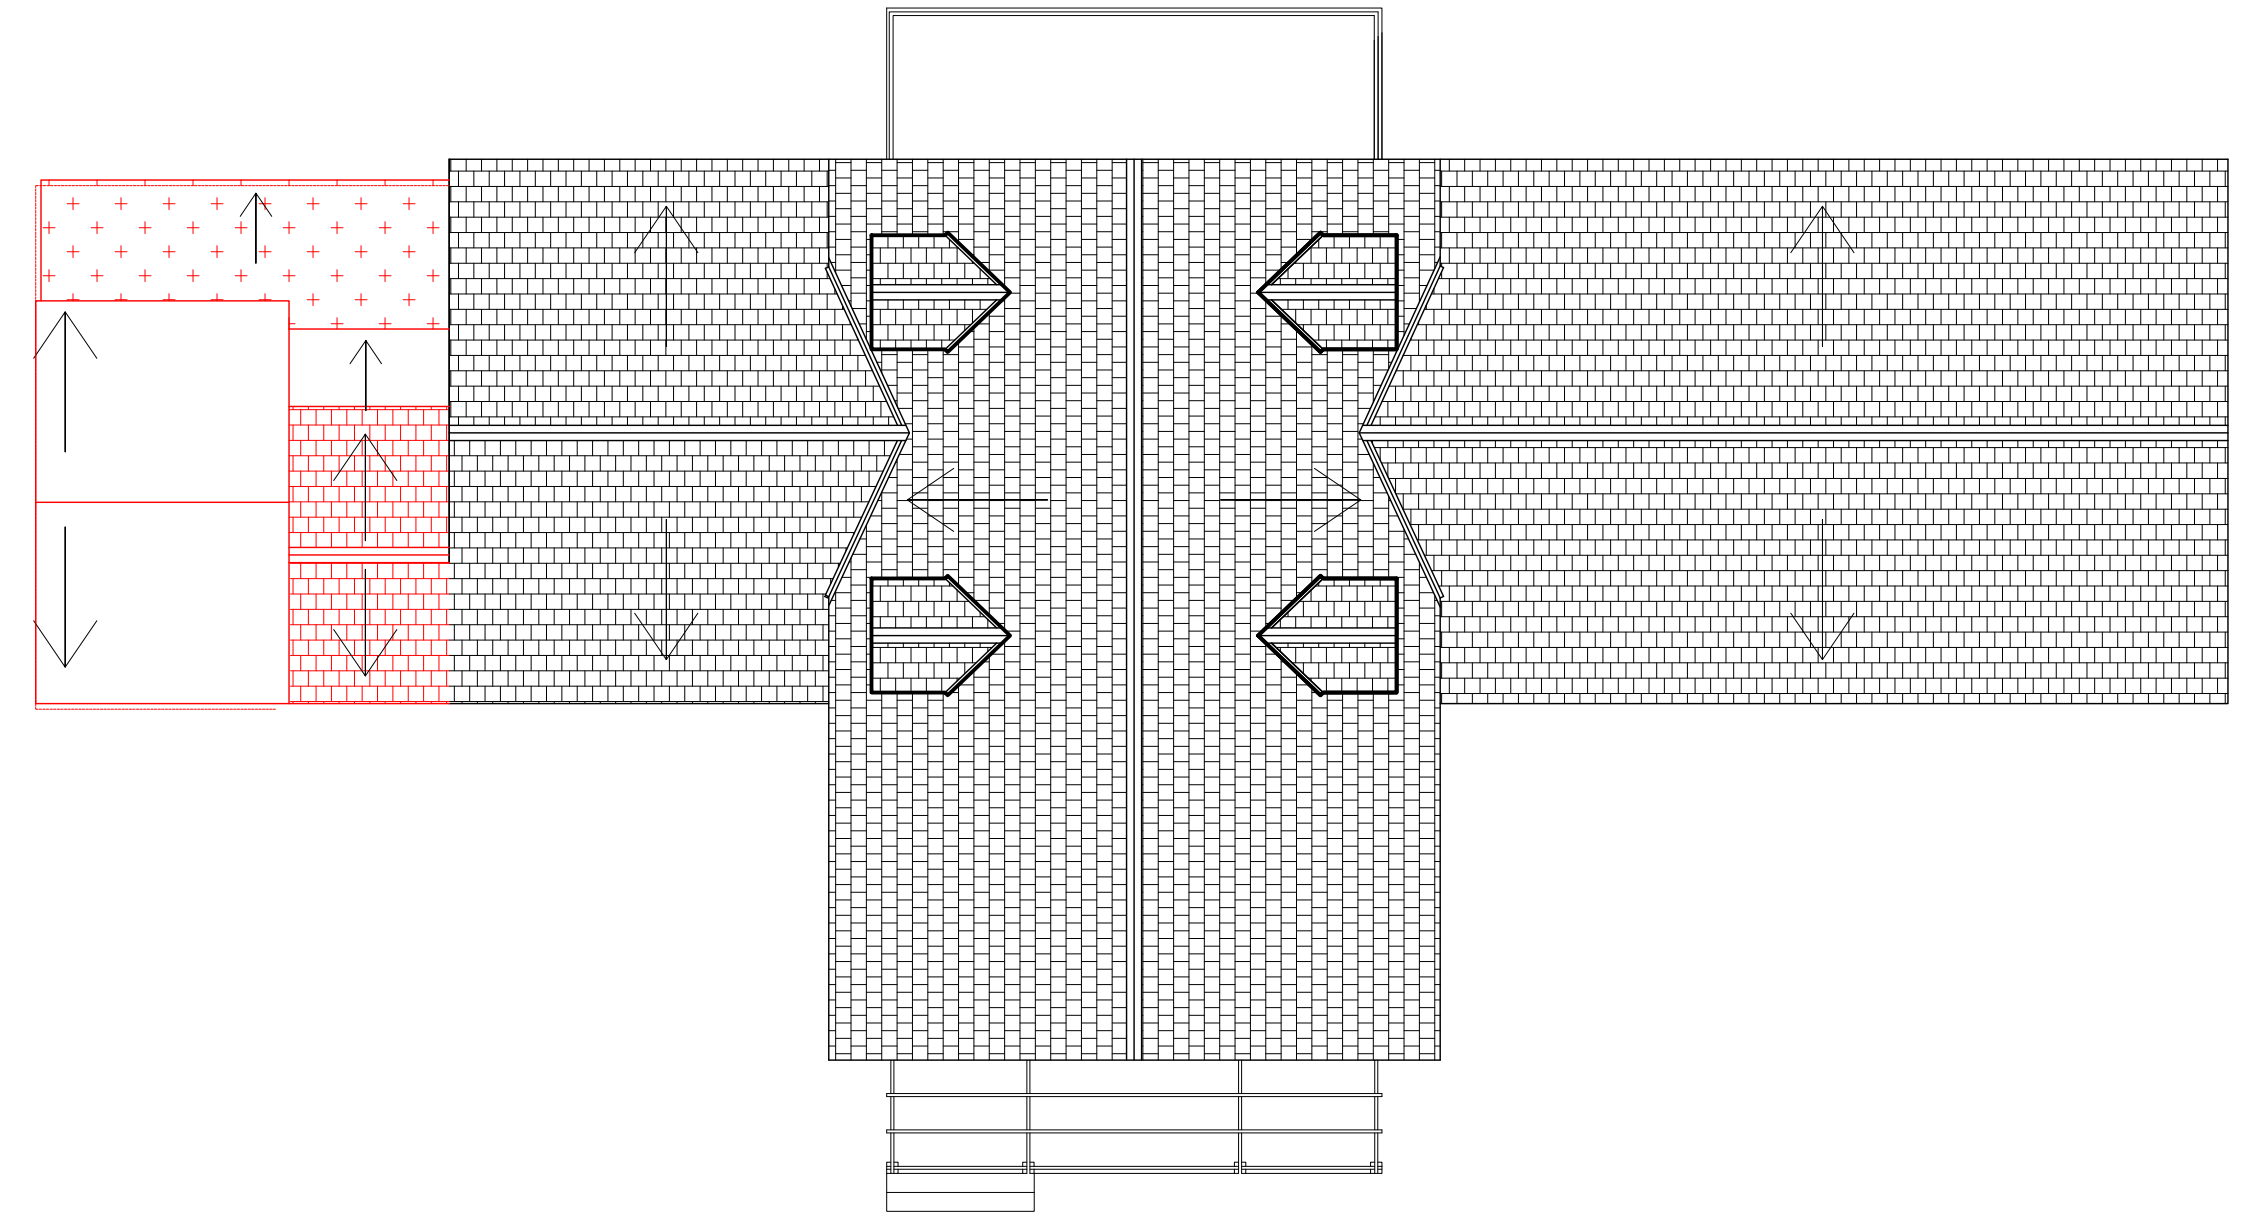


Planta Techos
Esc 1:100

CUADRO GENERAL DE SUPERFICIES (P.Edif. N°01/02 05-09-02)	
A) Superficie construida Primer Piso (interior cerrado)	134 m2 (x 100%)
B) Superficie construida Primer Piso (exterior cubierto)	70 m2 (x 50%)
C) Superficie construida Segundo Piso (interior cerrado)	43 m2 (x 100%)
D) Superficie construida Segundo Piso (terrace)	13 m2 (x 0%)
Superficie construida Total (ponderada)	212 m2
Superficie de ocupación en el terreno	204 m2
Superficie Terreno (aprox.)	4.454 m2
Porcentaje de ocupación de suelo	4.58 %
Porcentaje de constructibilidad	4.76 %


CUADRO GENERAL DE SUPERFICIES PROYECTADA	
Superficie construida P.Edif. n°01/02	212 m2
E) Superficie construida Primer Piso (interior cerrado)	38.0 m2 (x 100%)
F) Superficie construida Segundo Piso (interior cerrado)	13.4 m2 (x 100%)
B) Superficie construida Primer Piso (exterior cubierto)	70 m2 (x 50%)
Superficie construida Total (ponderada)	298.4 m2
Superficie de ocupación en el terreno	242.0 m2
Superficie Terreno (aprox.)	4.454 m2
Porcentaje de ocupación de suelo	5.43 %
Porcentaje de constructibilidad	6.70 %

Nota: Poligonos B se cierran lateralmente, por lo que se suma el 50% de superficie hasta completar el 100%)

Esquema de Superficies Primer Piso

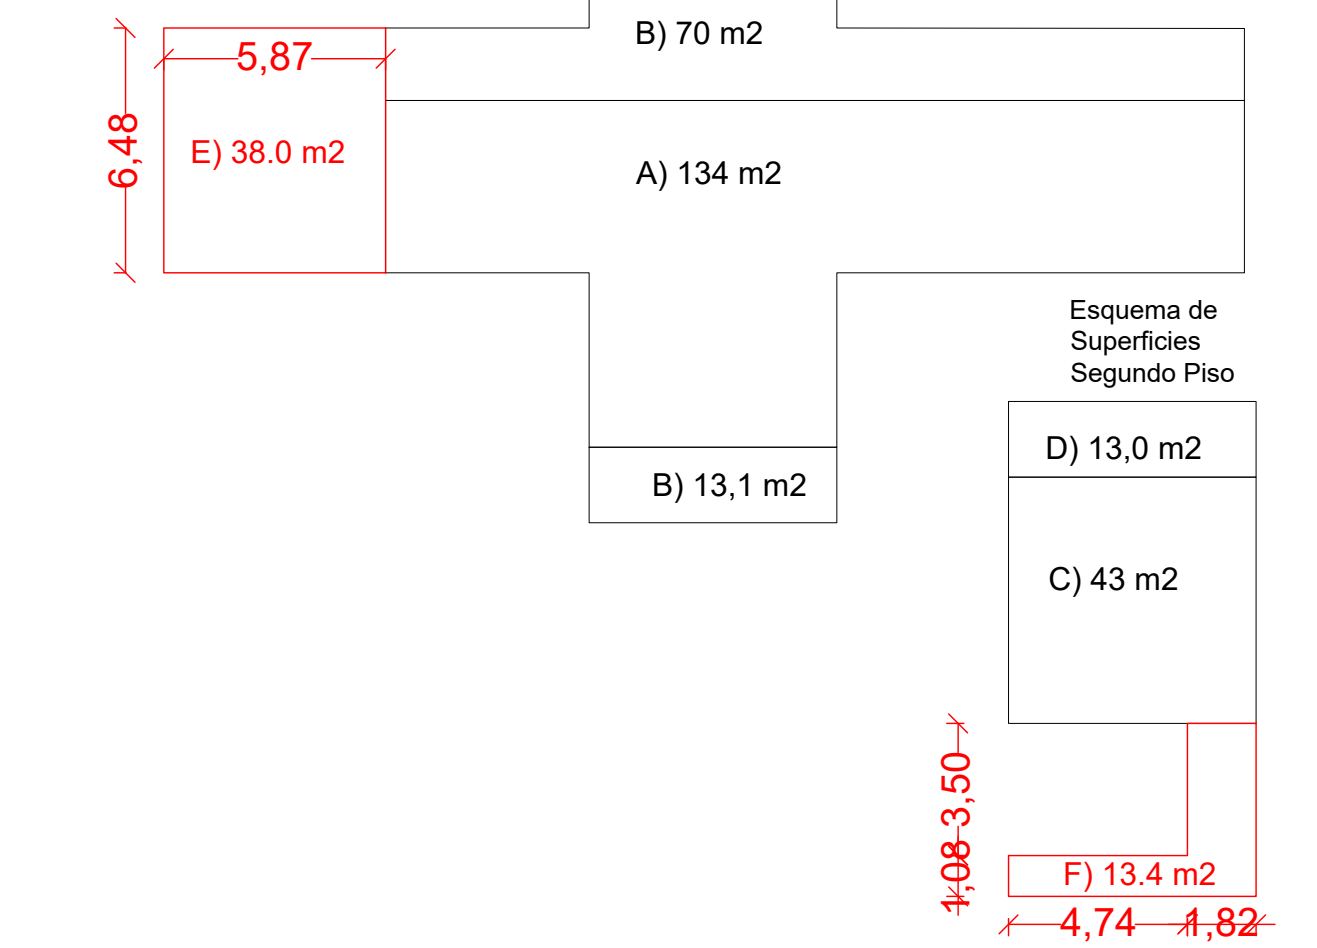


SIMBOLOGIA

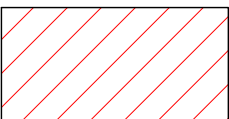 Se construye

CREA CIUDAD ARQUITECTURA

OBRA: PROYECTO CASA CAMPOLINDO

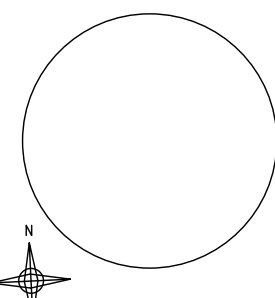UBICACION: 


CLIENTE: Maria Soledad Cabello
DIRECCIÓN: Calle Santa Ana s/n
COMUNA: Nariño
C.C. 54-121

ARQUITECTO: Tomás Fajardo Cabello
Arquitecto P.U.C. - I.C.A. 8373
Juana de Arco 2012 al 31. F. 344 45 44
tomafajardo@creaciudad.cl


CONTENIDO: Croquis de Ubicación
Plano de Emplazamiento
Planta de Techos
Cuadro de Superficies
Fecha: Agosto 2023 Dibujo: JMA

Lamina: 1 de 4

A1
Escala: Indicada

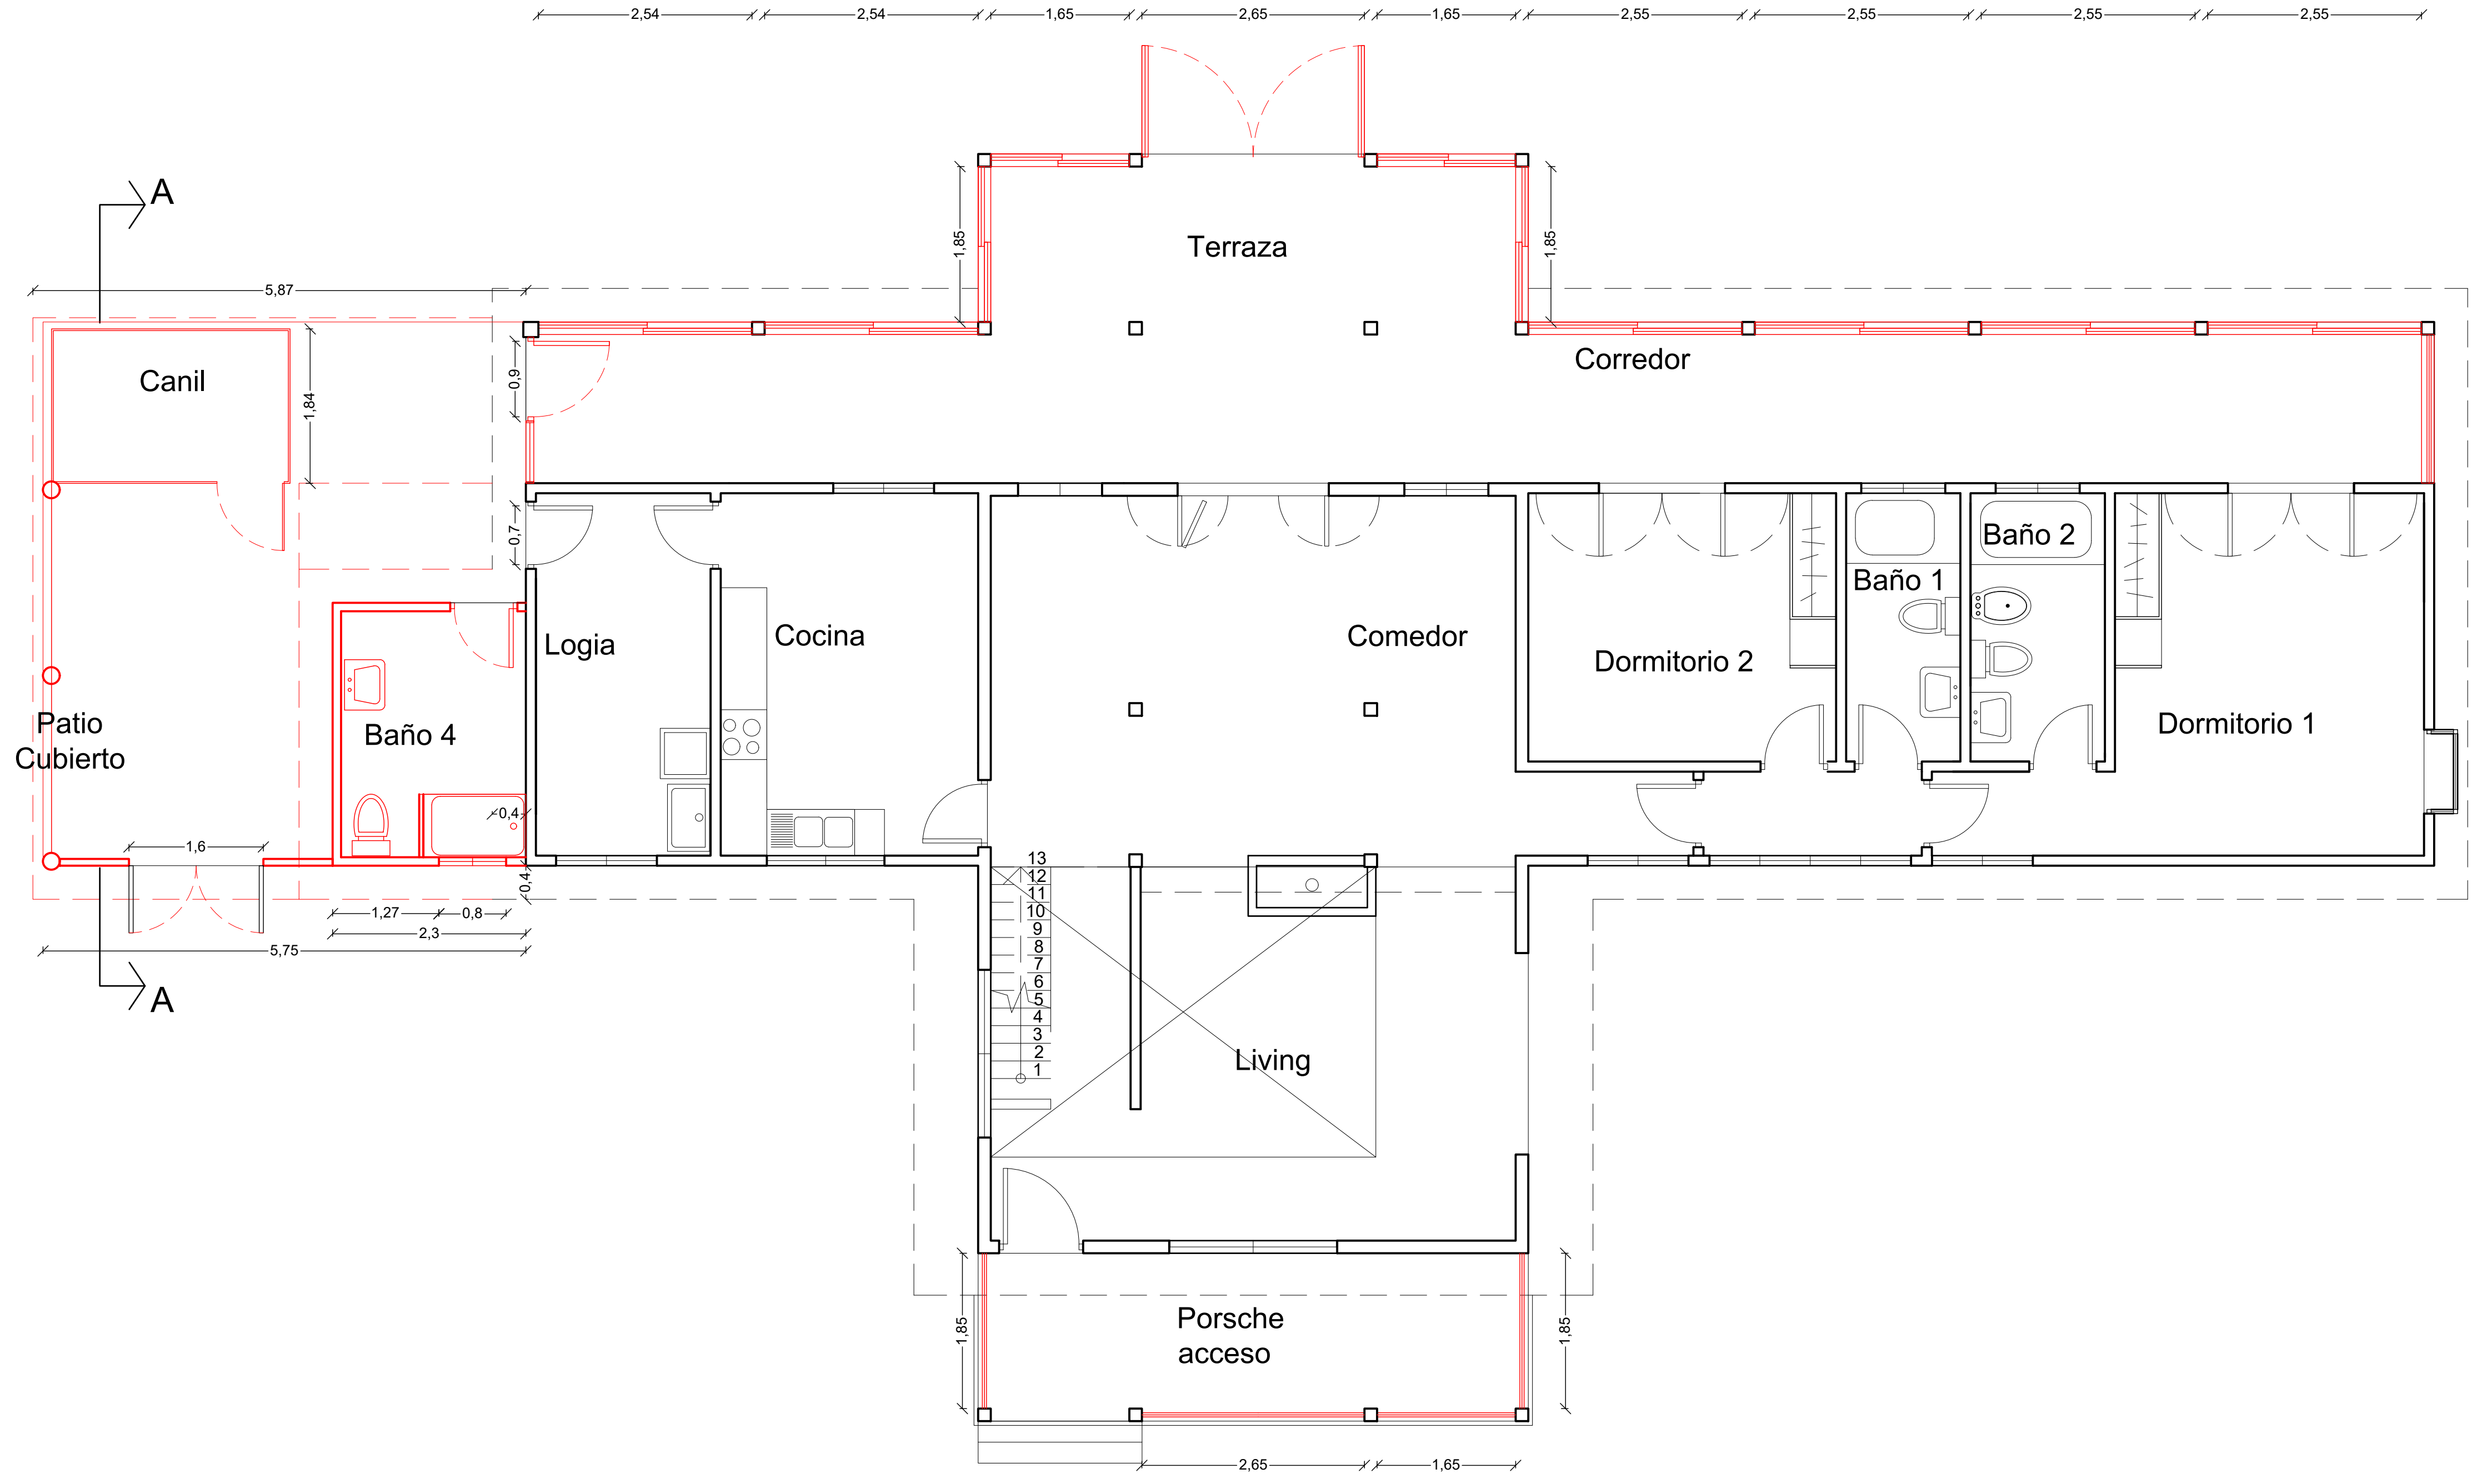


Planta Primer Piso
Esc 1:50

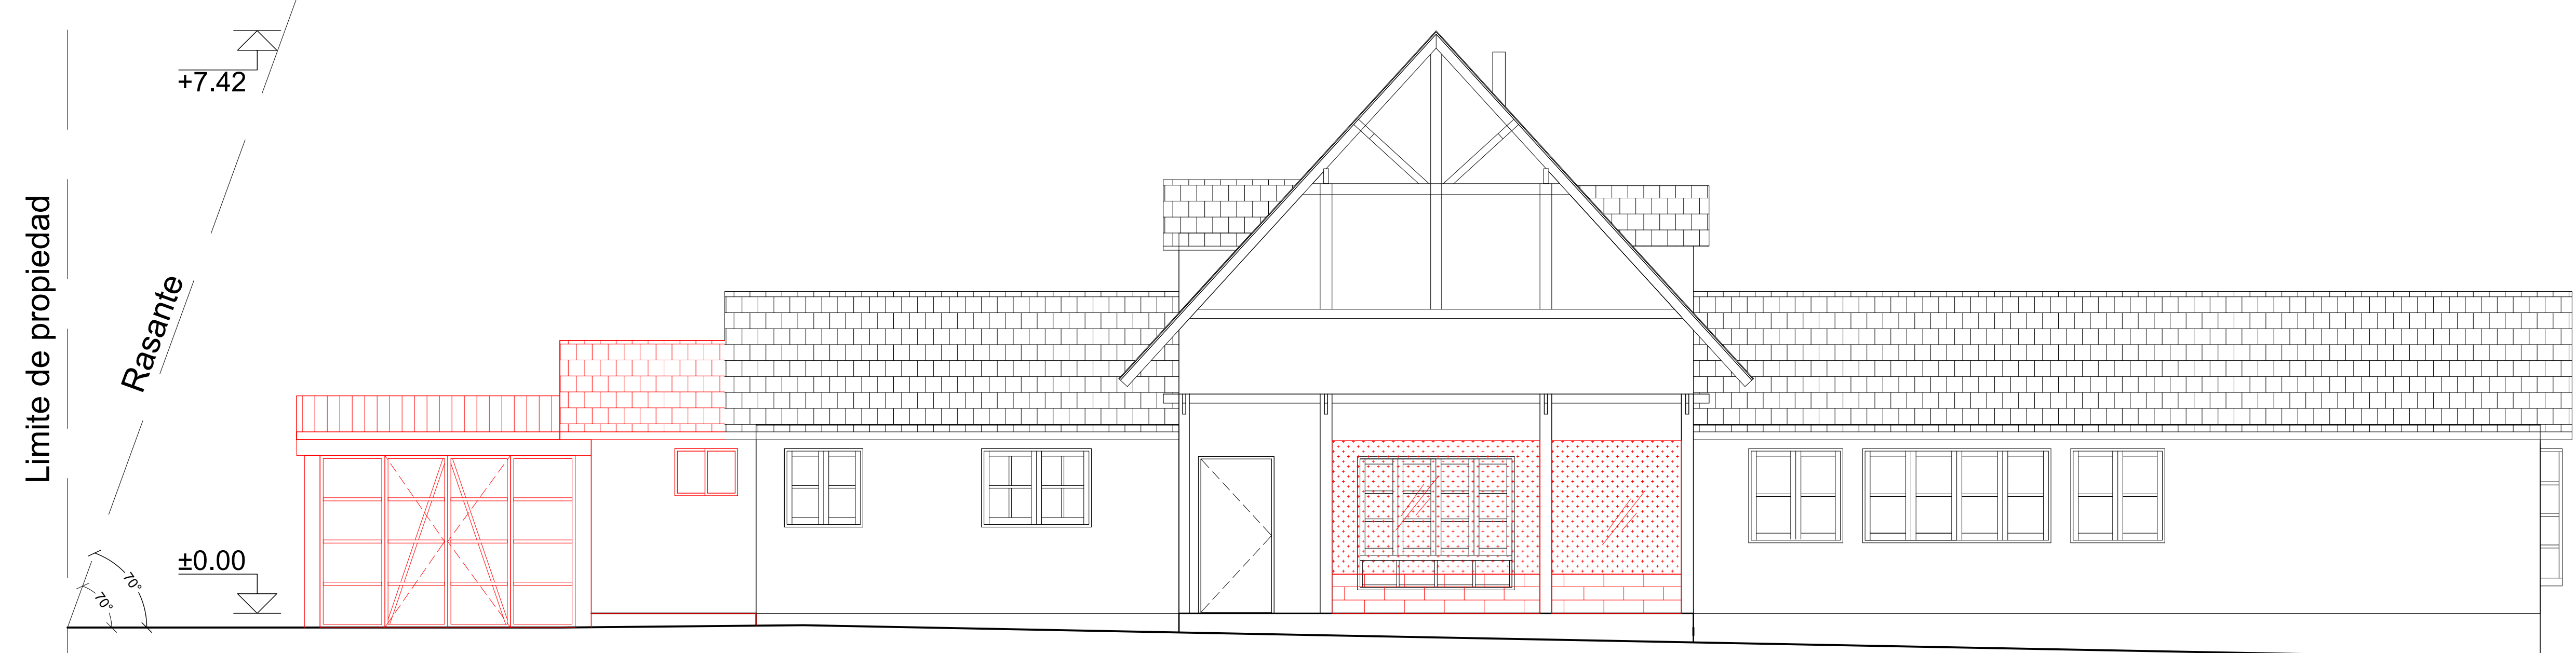


Elevación Sur
Esc 1:50


SIMBOLOGIA

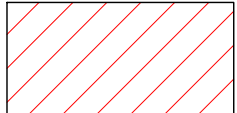 Se construye

CREATIVIDAD ARQUITECTURA		
OBRA: PROYECTO CASA CAMPOLINDO		
UBICACIÓN:	CLIENTE:	ARQUITECTO:
	Maria Soledad Cabello DIRECCIÓN: Calle Santa Ana s/n COMUNA: Nariño C.C. 54-121	Tomás Fajardo Cabello Arquitecto P.U.C. - I.C.A. 8373 Jornal de Año 2012 al 31. F. 344-45-44 tomafajardo@creatividad.cl
	CONTENIDO:	
	Planta Proyecto de Arquitectura -Primer Piso -Elevación Sur	
Fecha: Agosto 2023	Dibujo: JMA	Lamina: 2 de 4 A2 Escala: Indicada

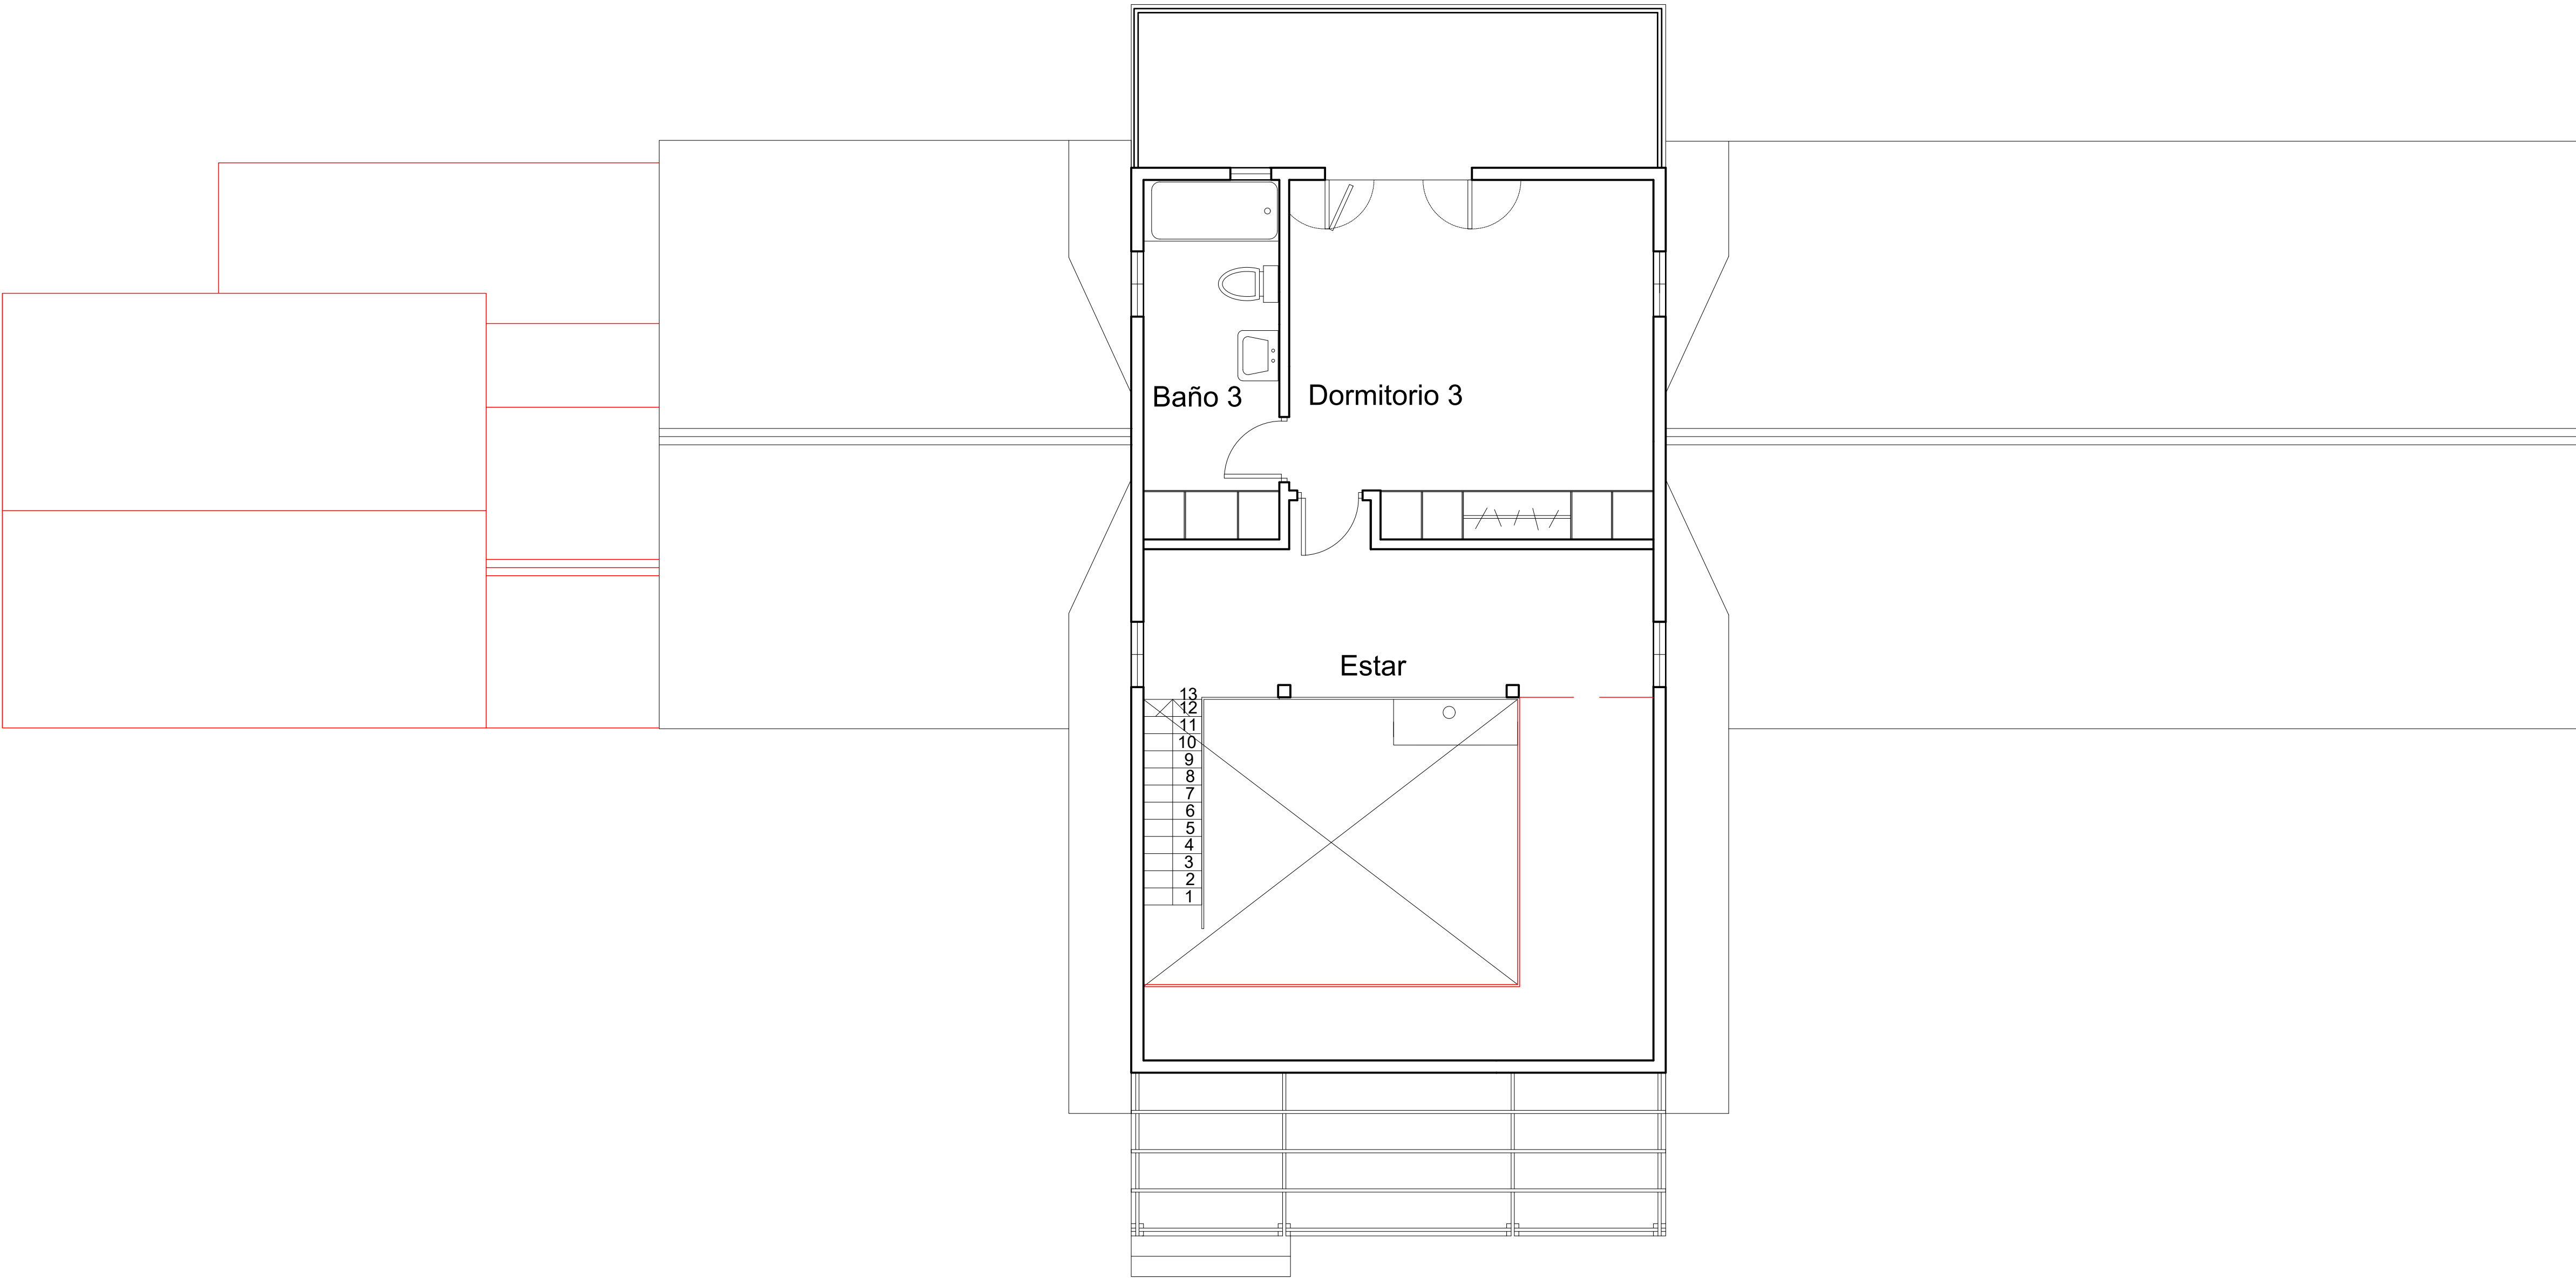


Planta Segundo Piso
Esc 1:50

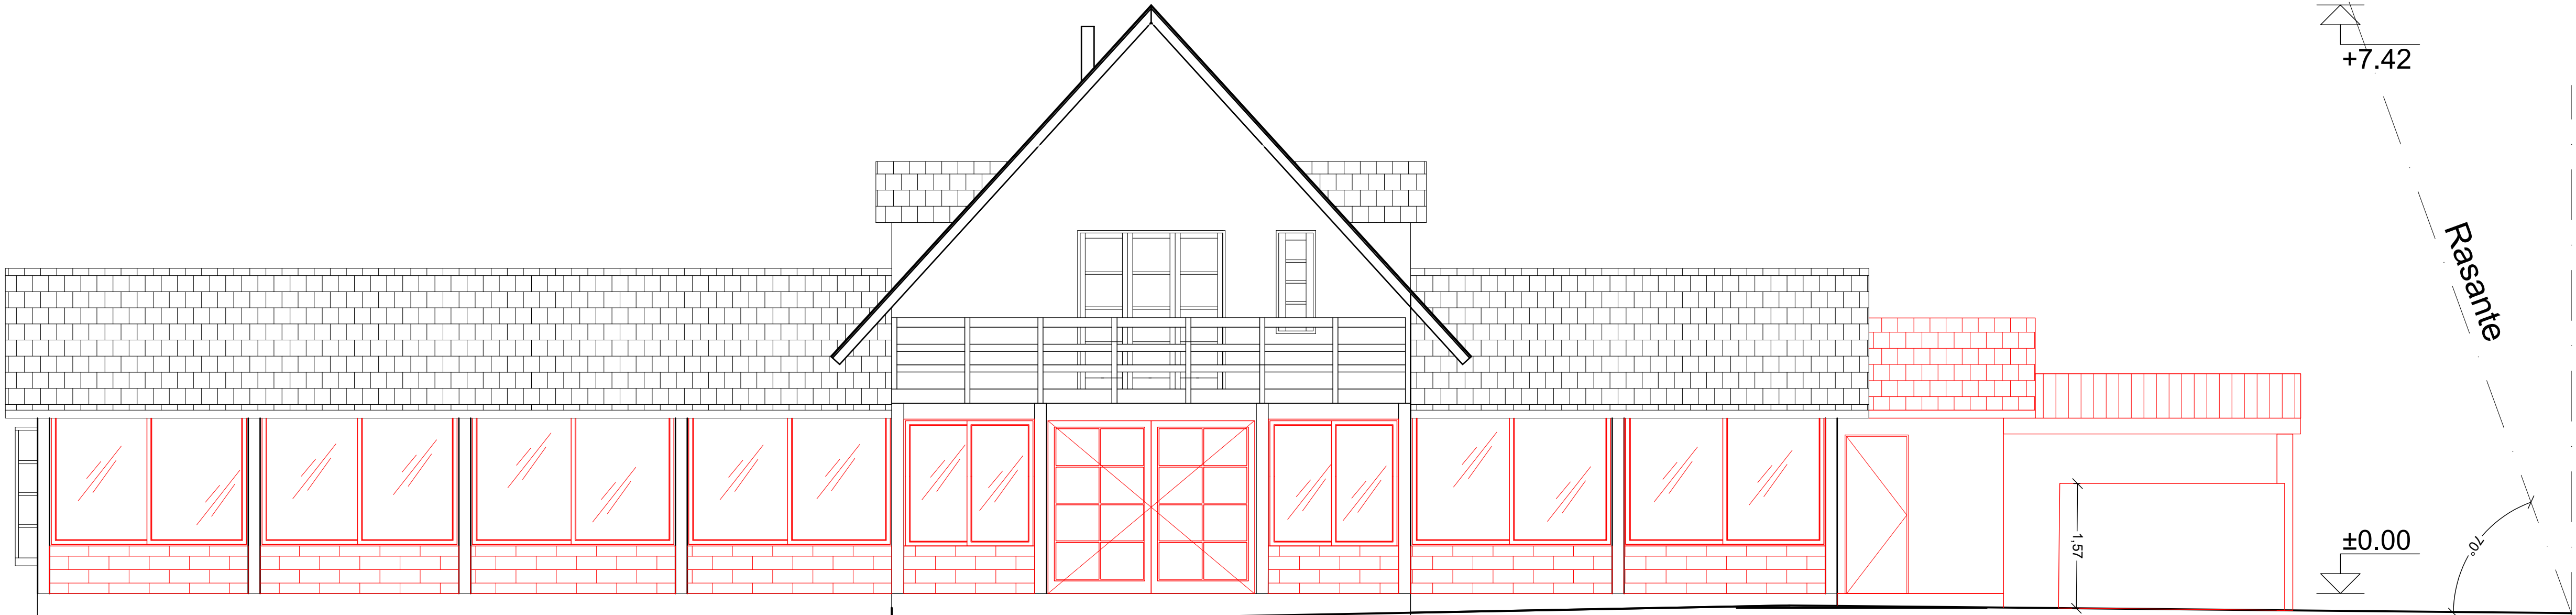

Elevación Norte
Esc 1:50

SIMBOLOGIA

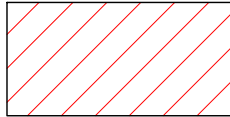 Se construye


CREATIVIDAD ARQUITECTURA		
PROYECTO CASA CAMPOLINDO		
OBRA:	CLIENTE:	ARQUITECTO:
UBICACIÓN:	Maria Soledad Cabello DIRECCIÓN: Calle Santa Ana s/n COMUNA: Riquelme R.C. 54-121	Tomás Fajardo Cabello Arquitecto P.U.C. - I.C.A. 8373 Jornal de Año 2012 al 31 F. 344 45 44 tomafajardo@creatividad.cl
	CONTENIDO:	Lamina: 3 de 4
	Planta Proyecto de Arquitectura	A3 Escala: Indicada
	-Segundo Piso -Elevación Norte	
Fecha: Agosto 2023	Dibujo: JMA	

Elevacion Poniente
Esc 1:50

Limite de propiedad

Rasante

70°

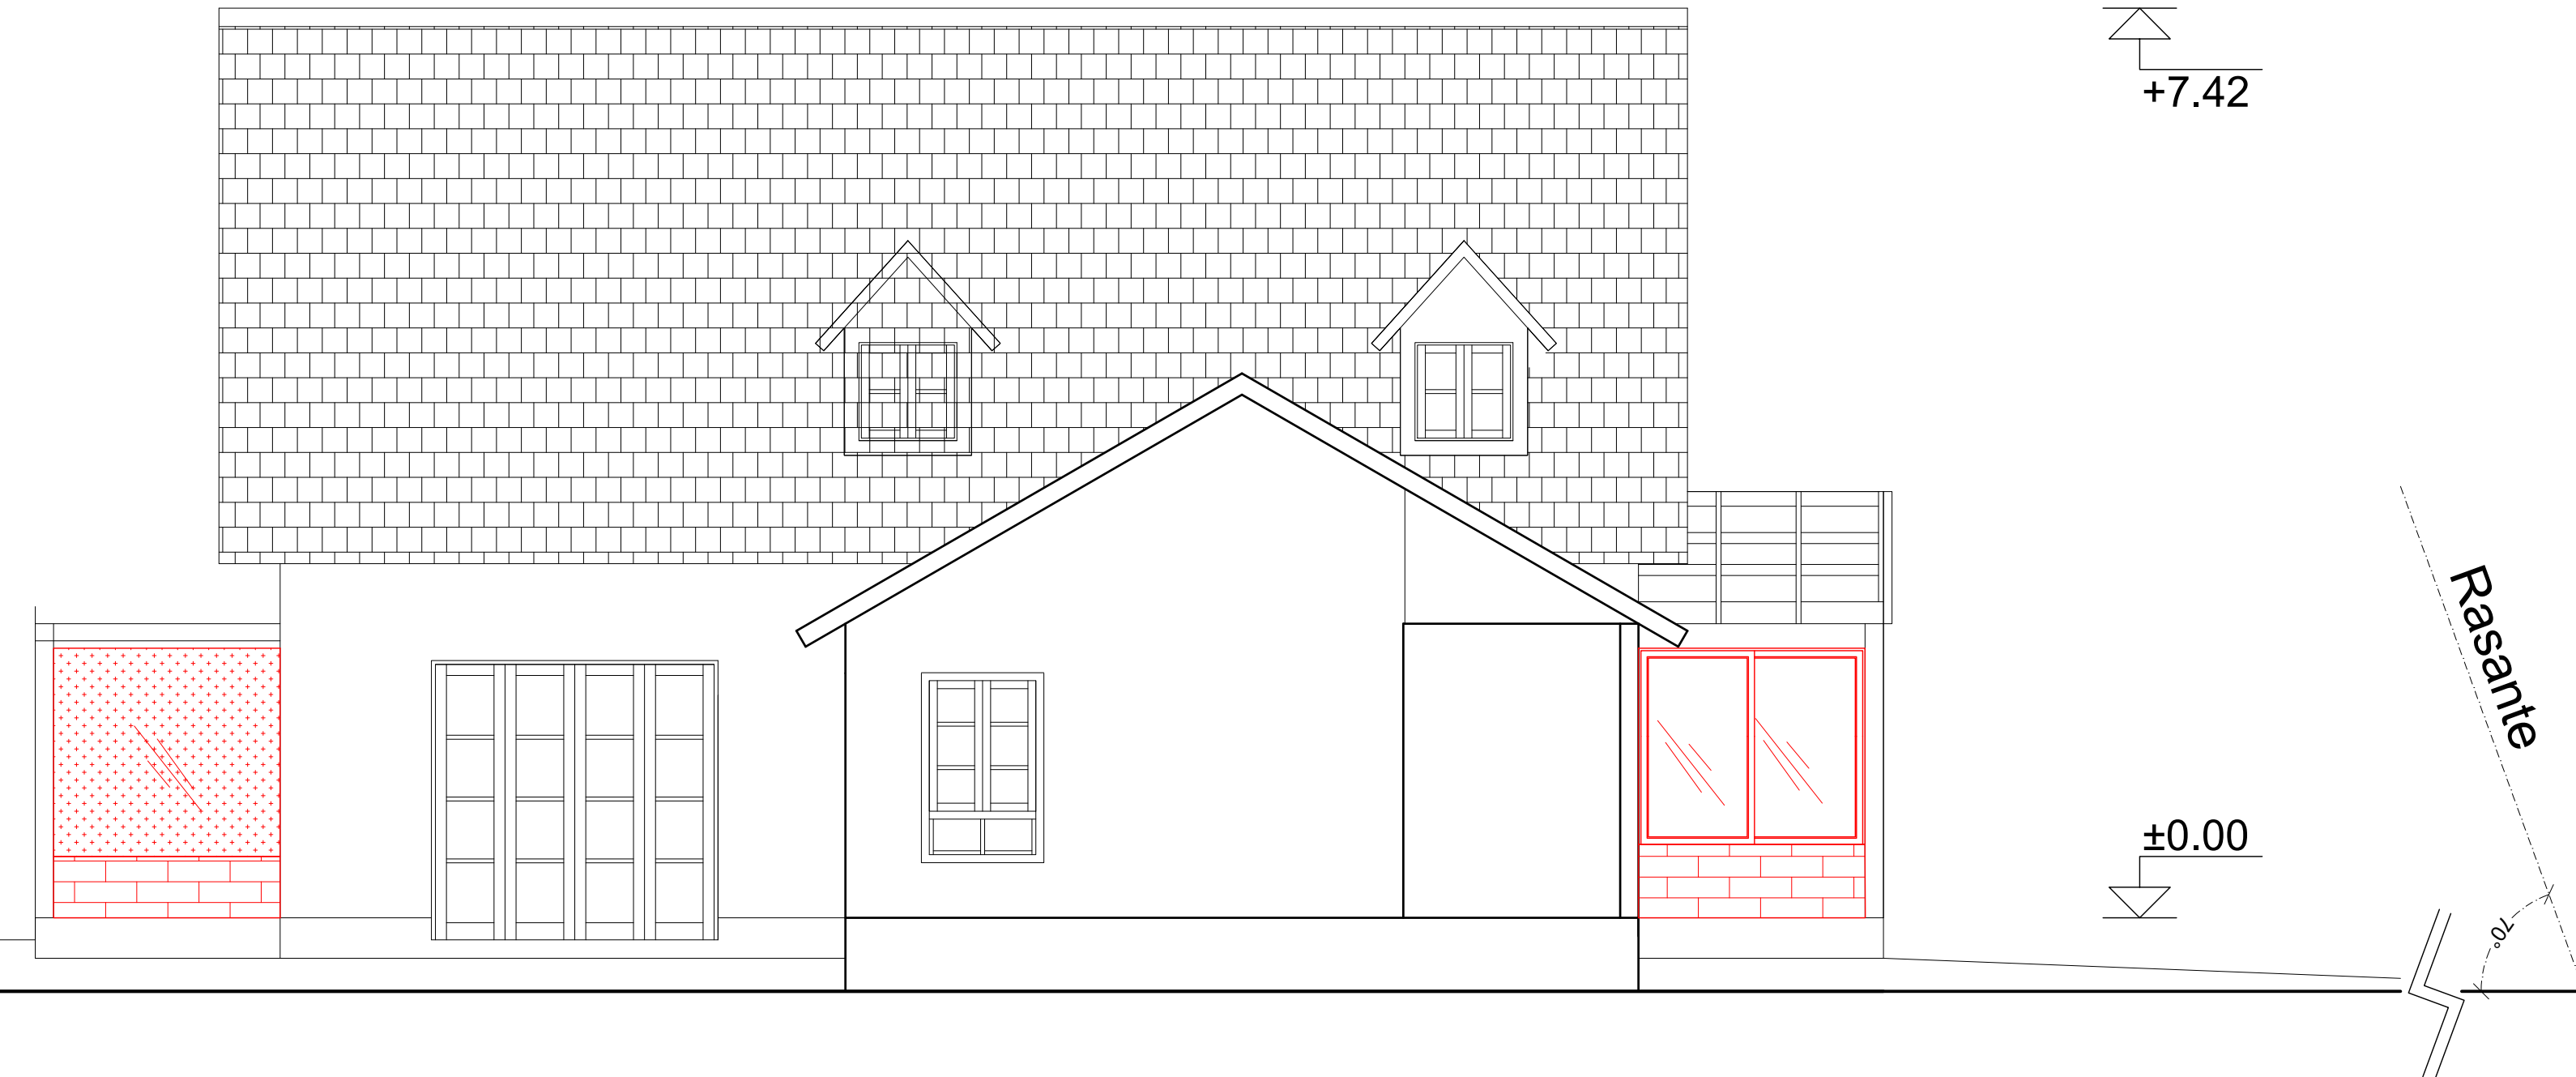

+7.42

±0.00

Limite de propiedad

Rasante


70°

Elevacion Oriente
Esc 1:50

Limite de propiedad

Rasante

70°

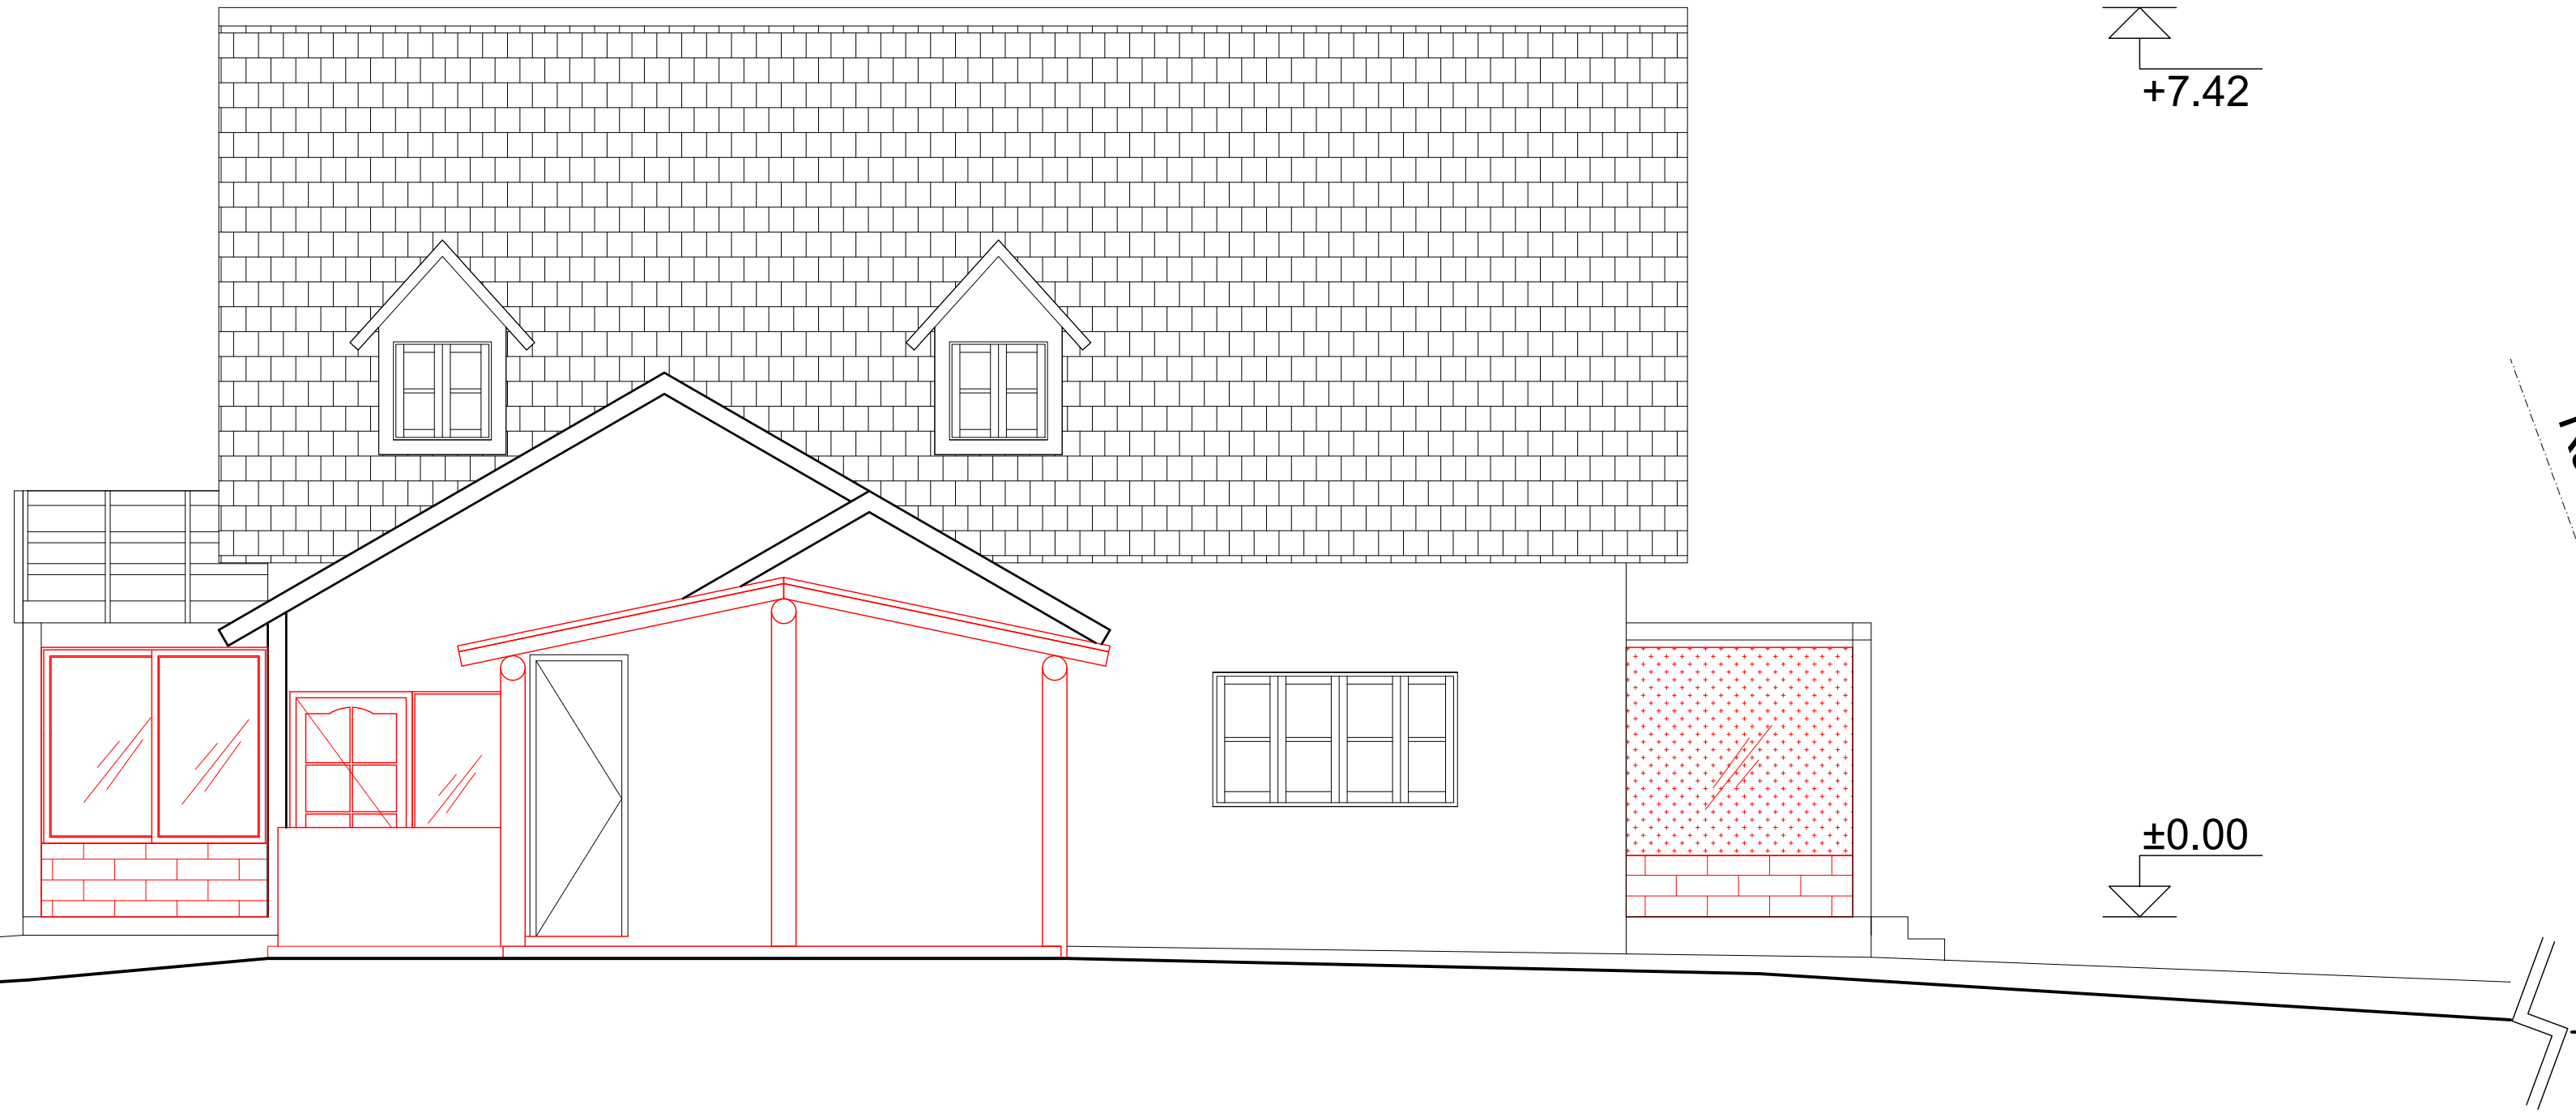

+7.42

±0.00

Rasante

70°


Limite de propiedad

Corte A-A
Esc 1:50

Limite de propiedad

Rasante

70°

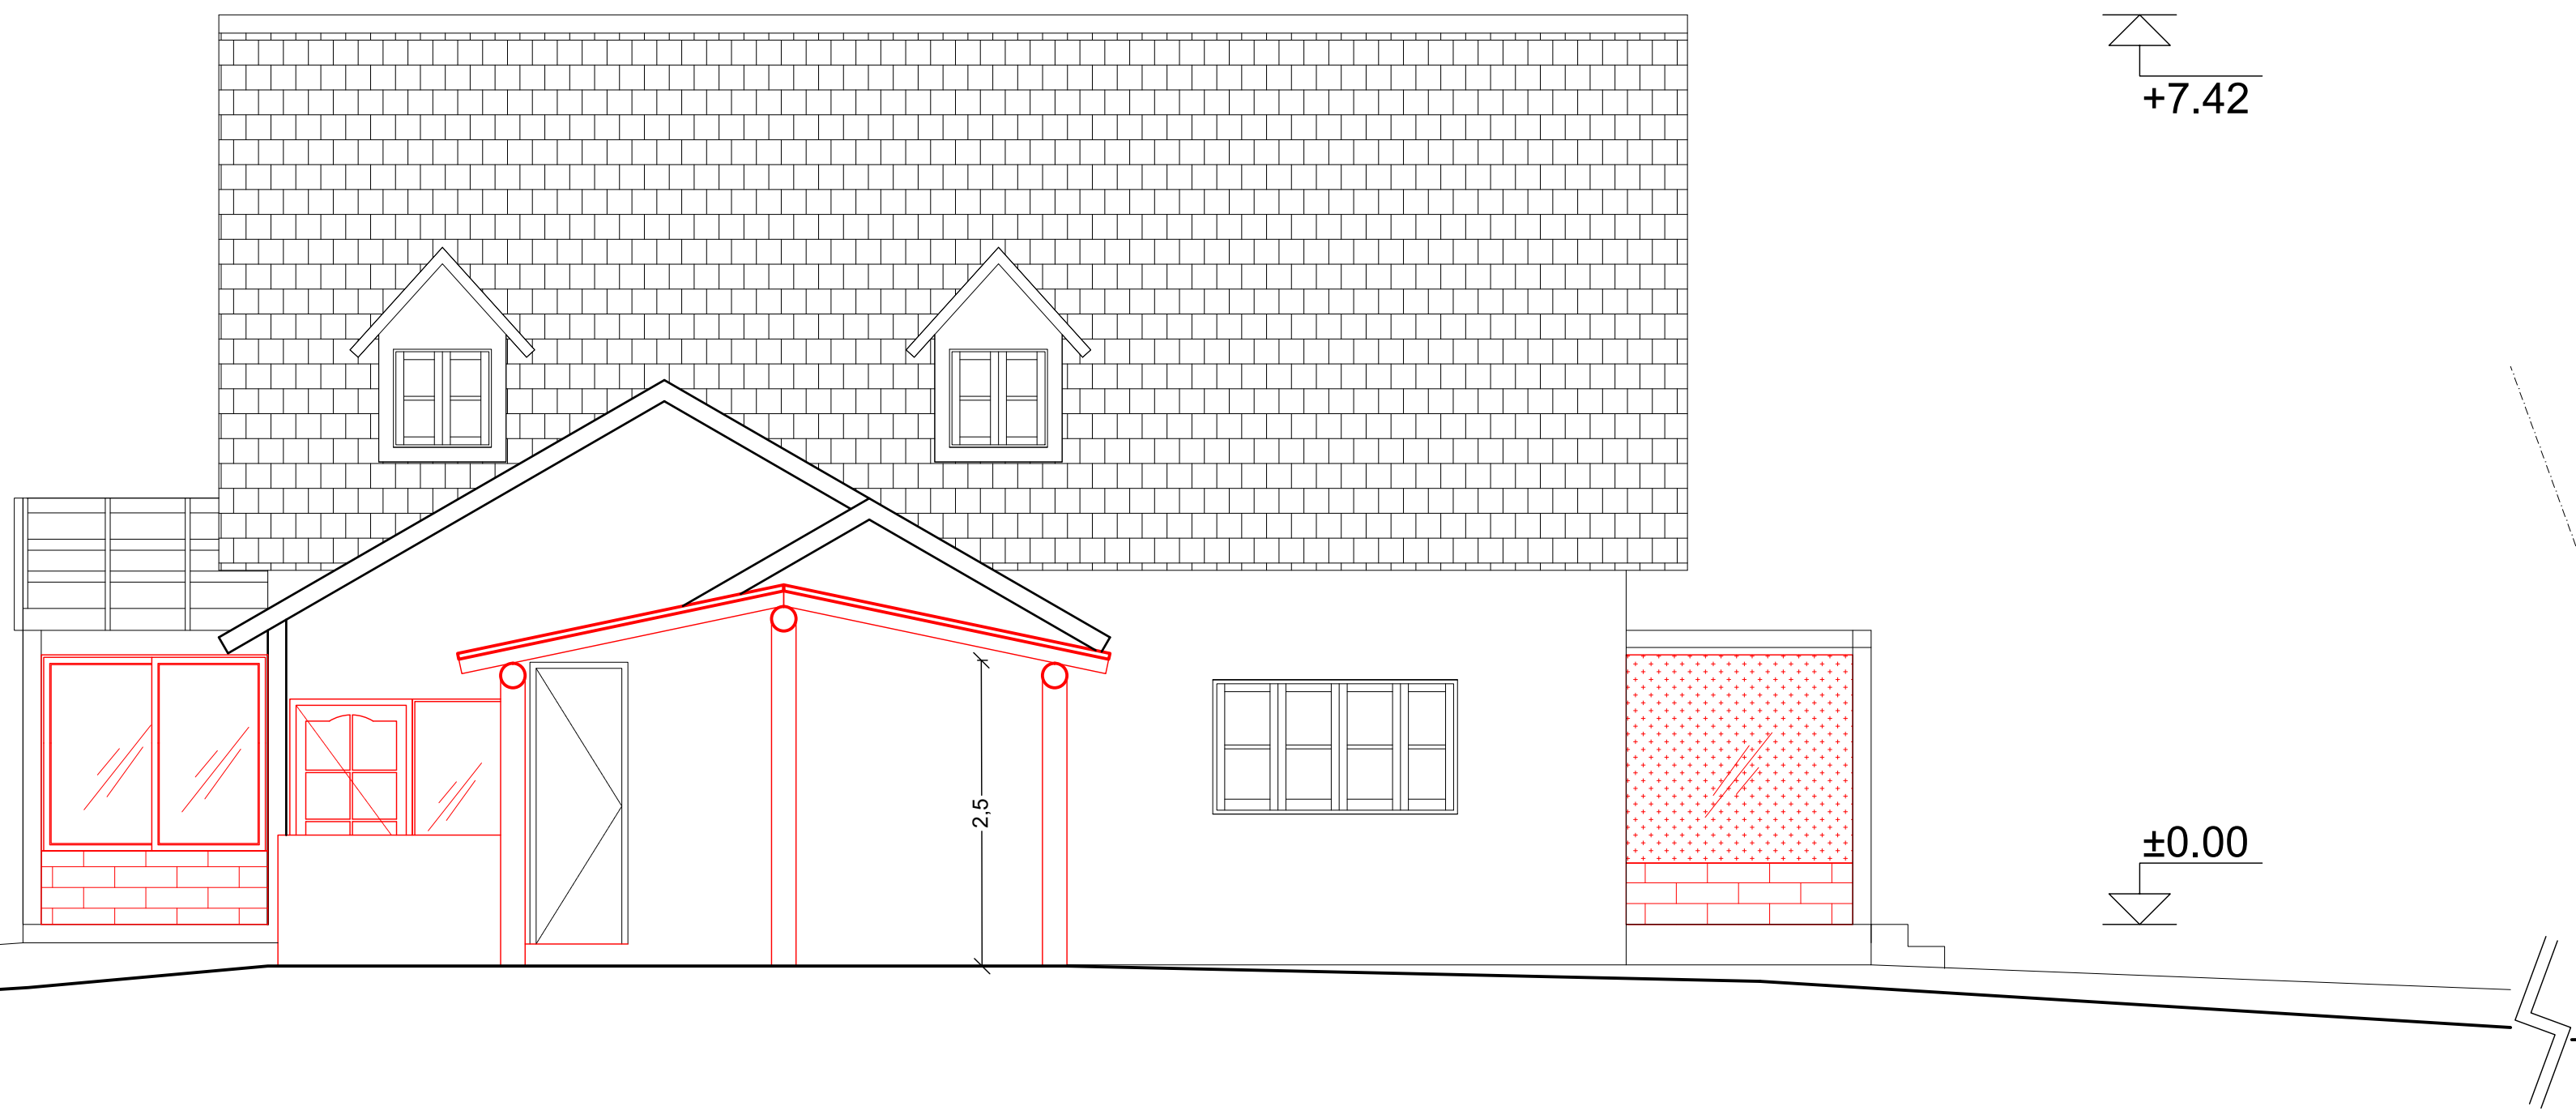

+7.42


±0.00

Rasante

70°

Limite de propiedad

SIMBOLOGIA

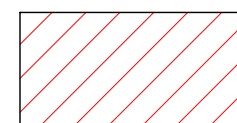


Se construye

CREATIVIDAD
ARQUITECTURA

OBRA: PROYECTO
CASA CAMPOLINDO

UBICACION:

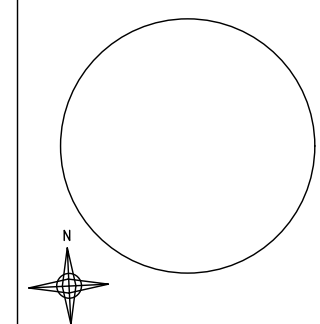

CLIENTE:

Maria Soledad Cabello
DIRECCIÓN: Calle Santa Ana s/n
COMUNA: Nariño
RCS: 54-121

ARQUITECTO:

Tomás Fajardo Cabello
Arquitecto P.U.C. - I.C.A. 8373
Jueves de Aro 2012 of. 31 F. 344 45 44
tomafajardo@creatividad.cl

CONTENIDO:
Elevación Oriente
Elevación Poniente
Corte A-A

Lamina: 4 de 4

A4
Escala: Indicada

Fecha: Agosto 2023 Dibujo: JMA