




Plano de Ubicación
Escala 1:5000

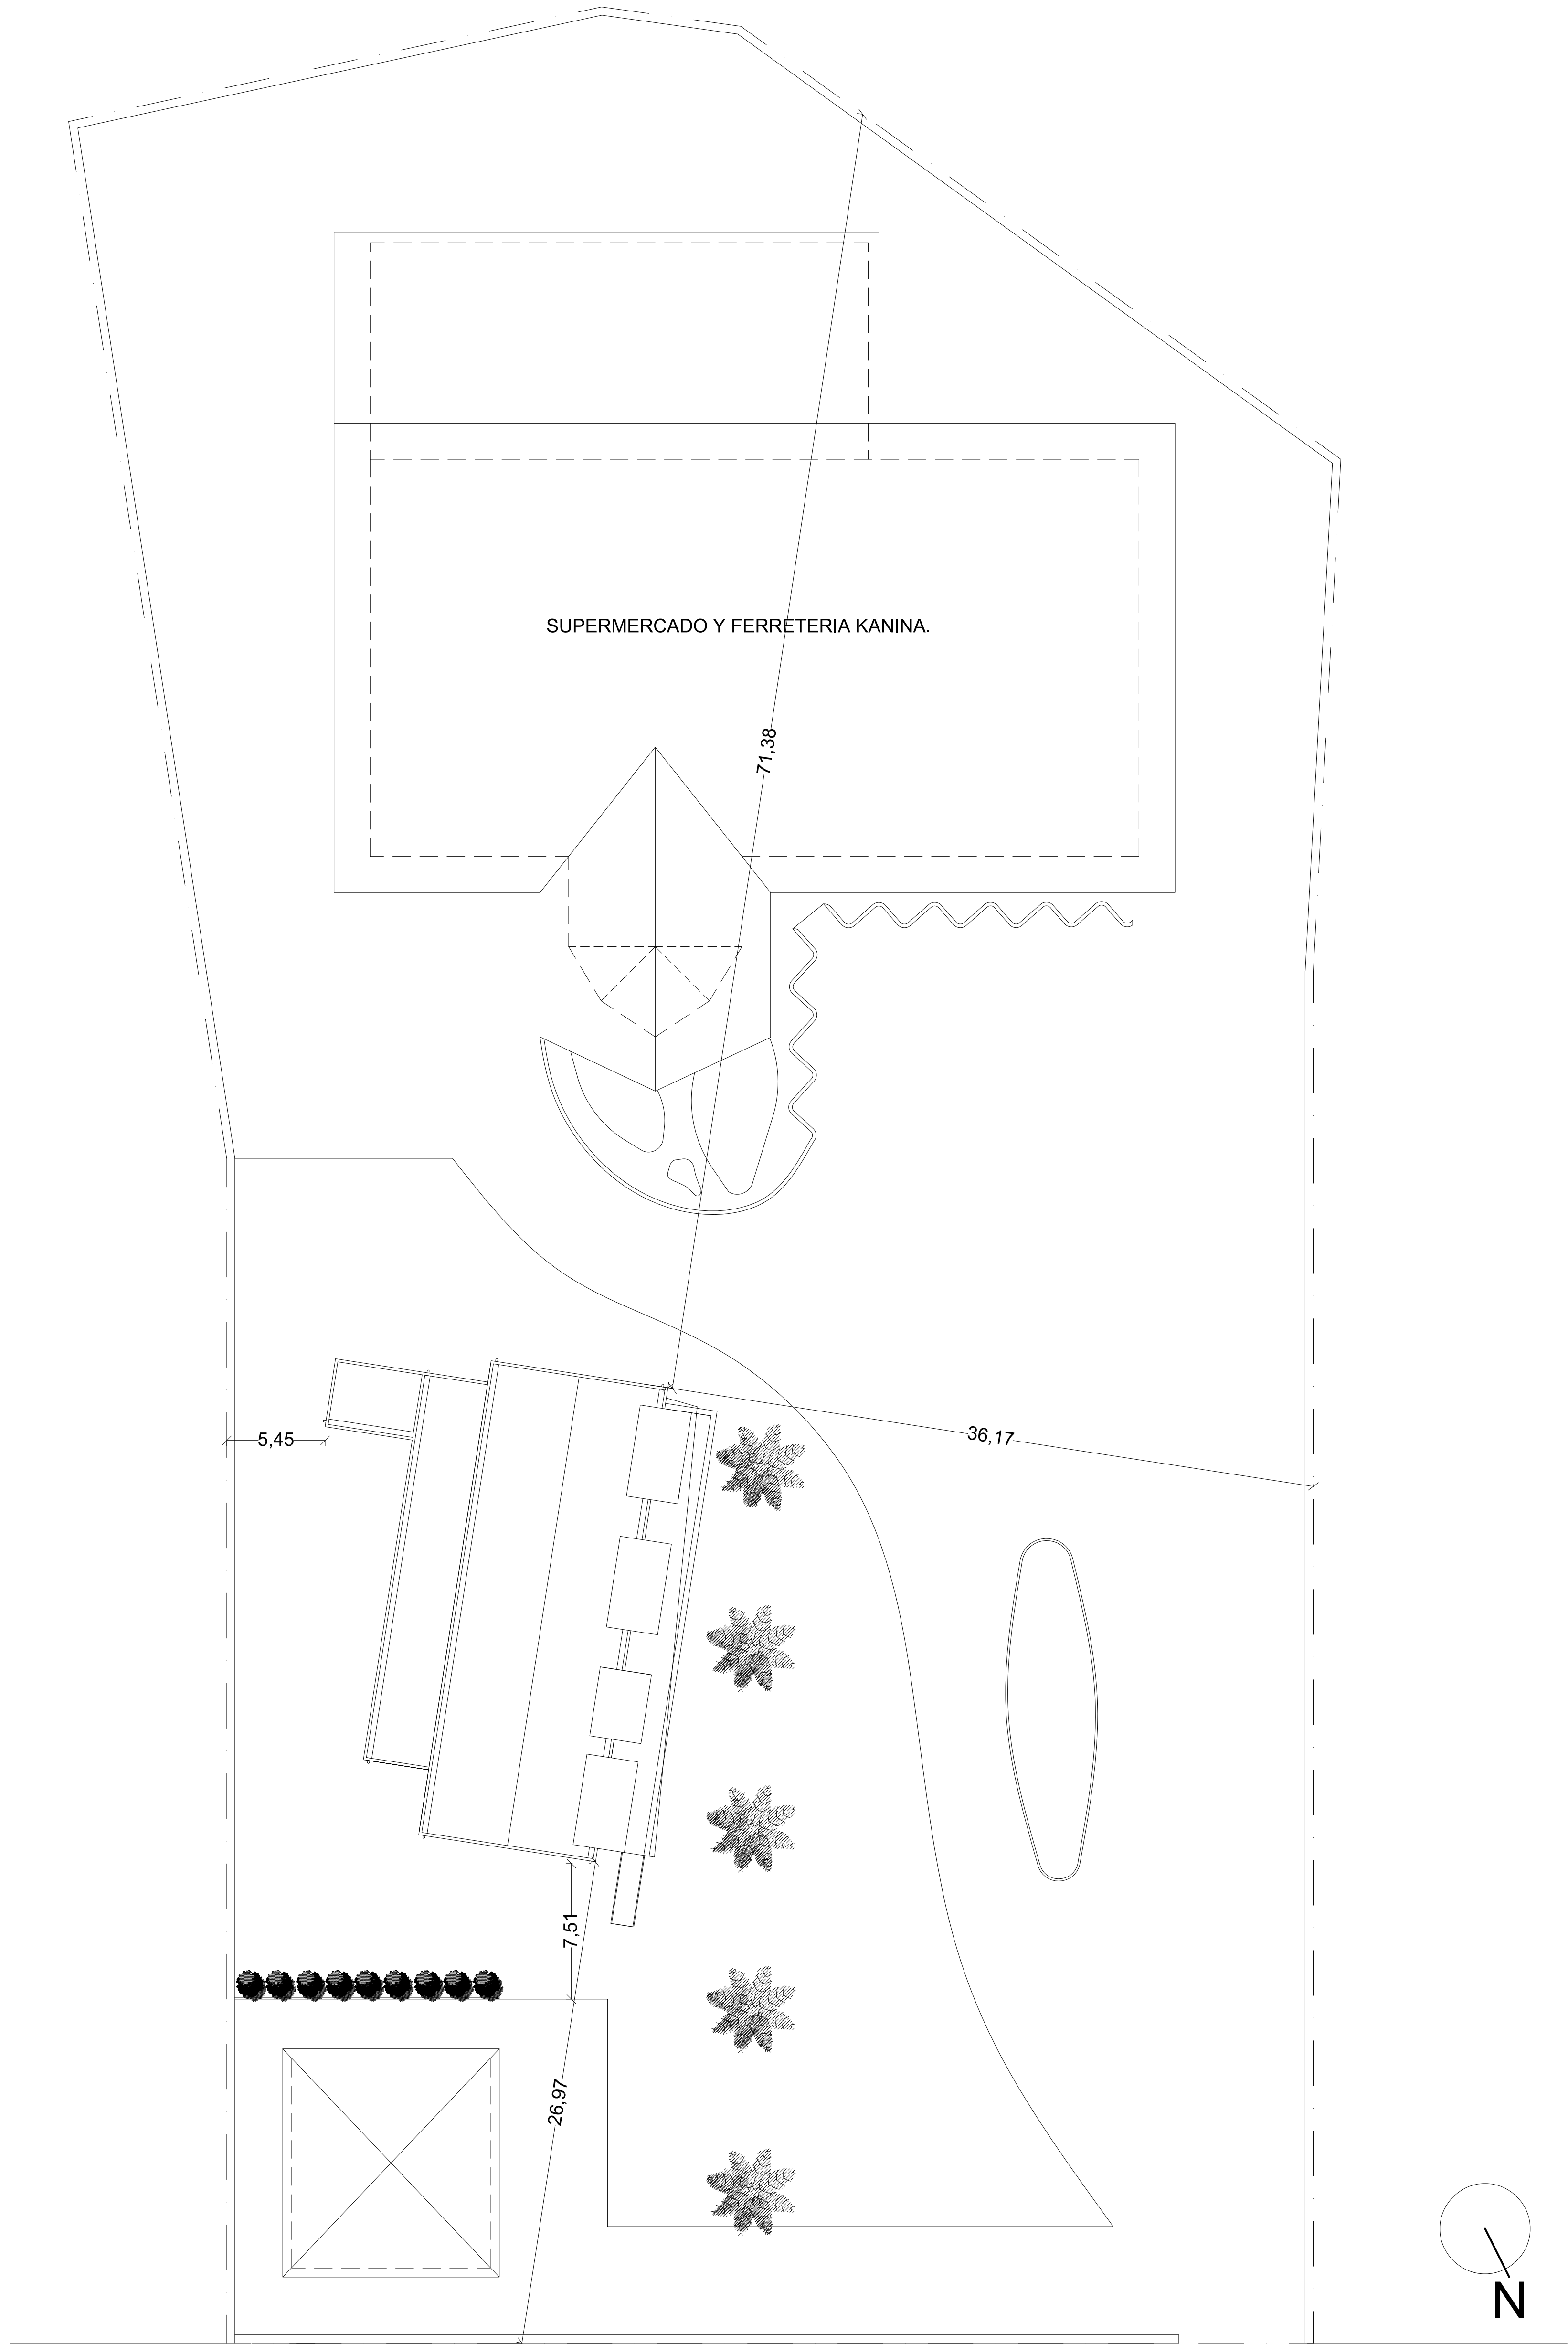

Plano de Emplazamiento
Escala 1:500

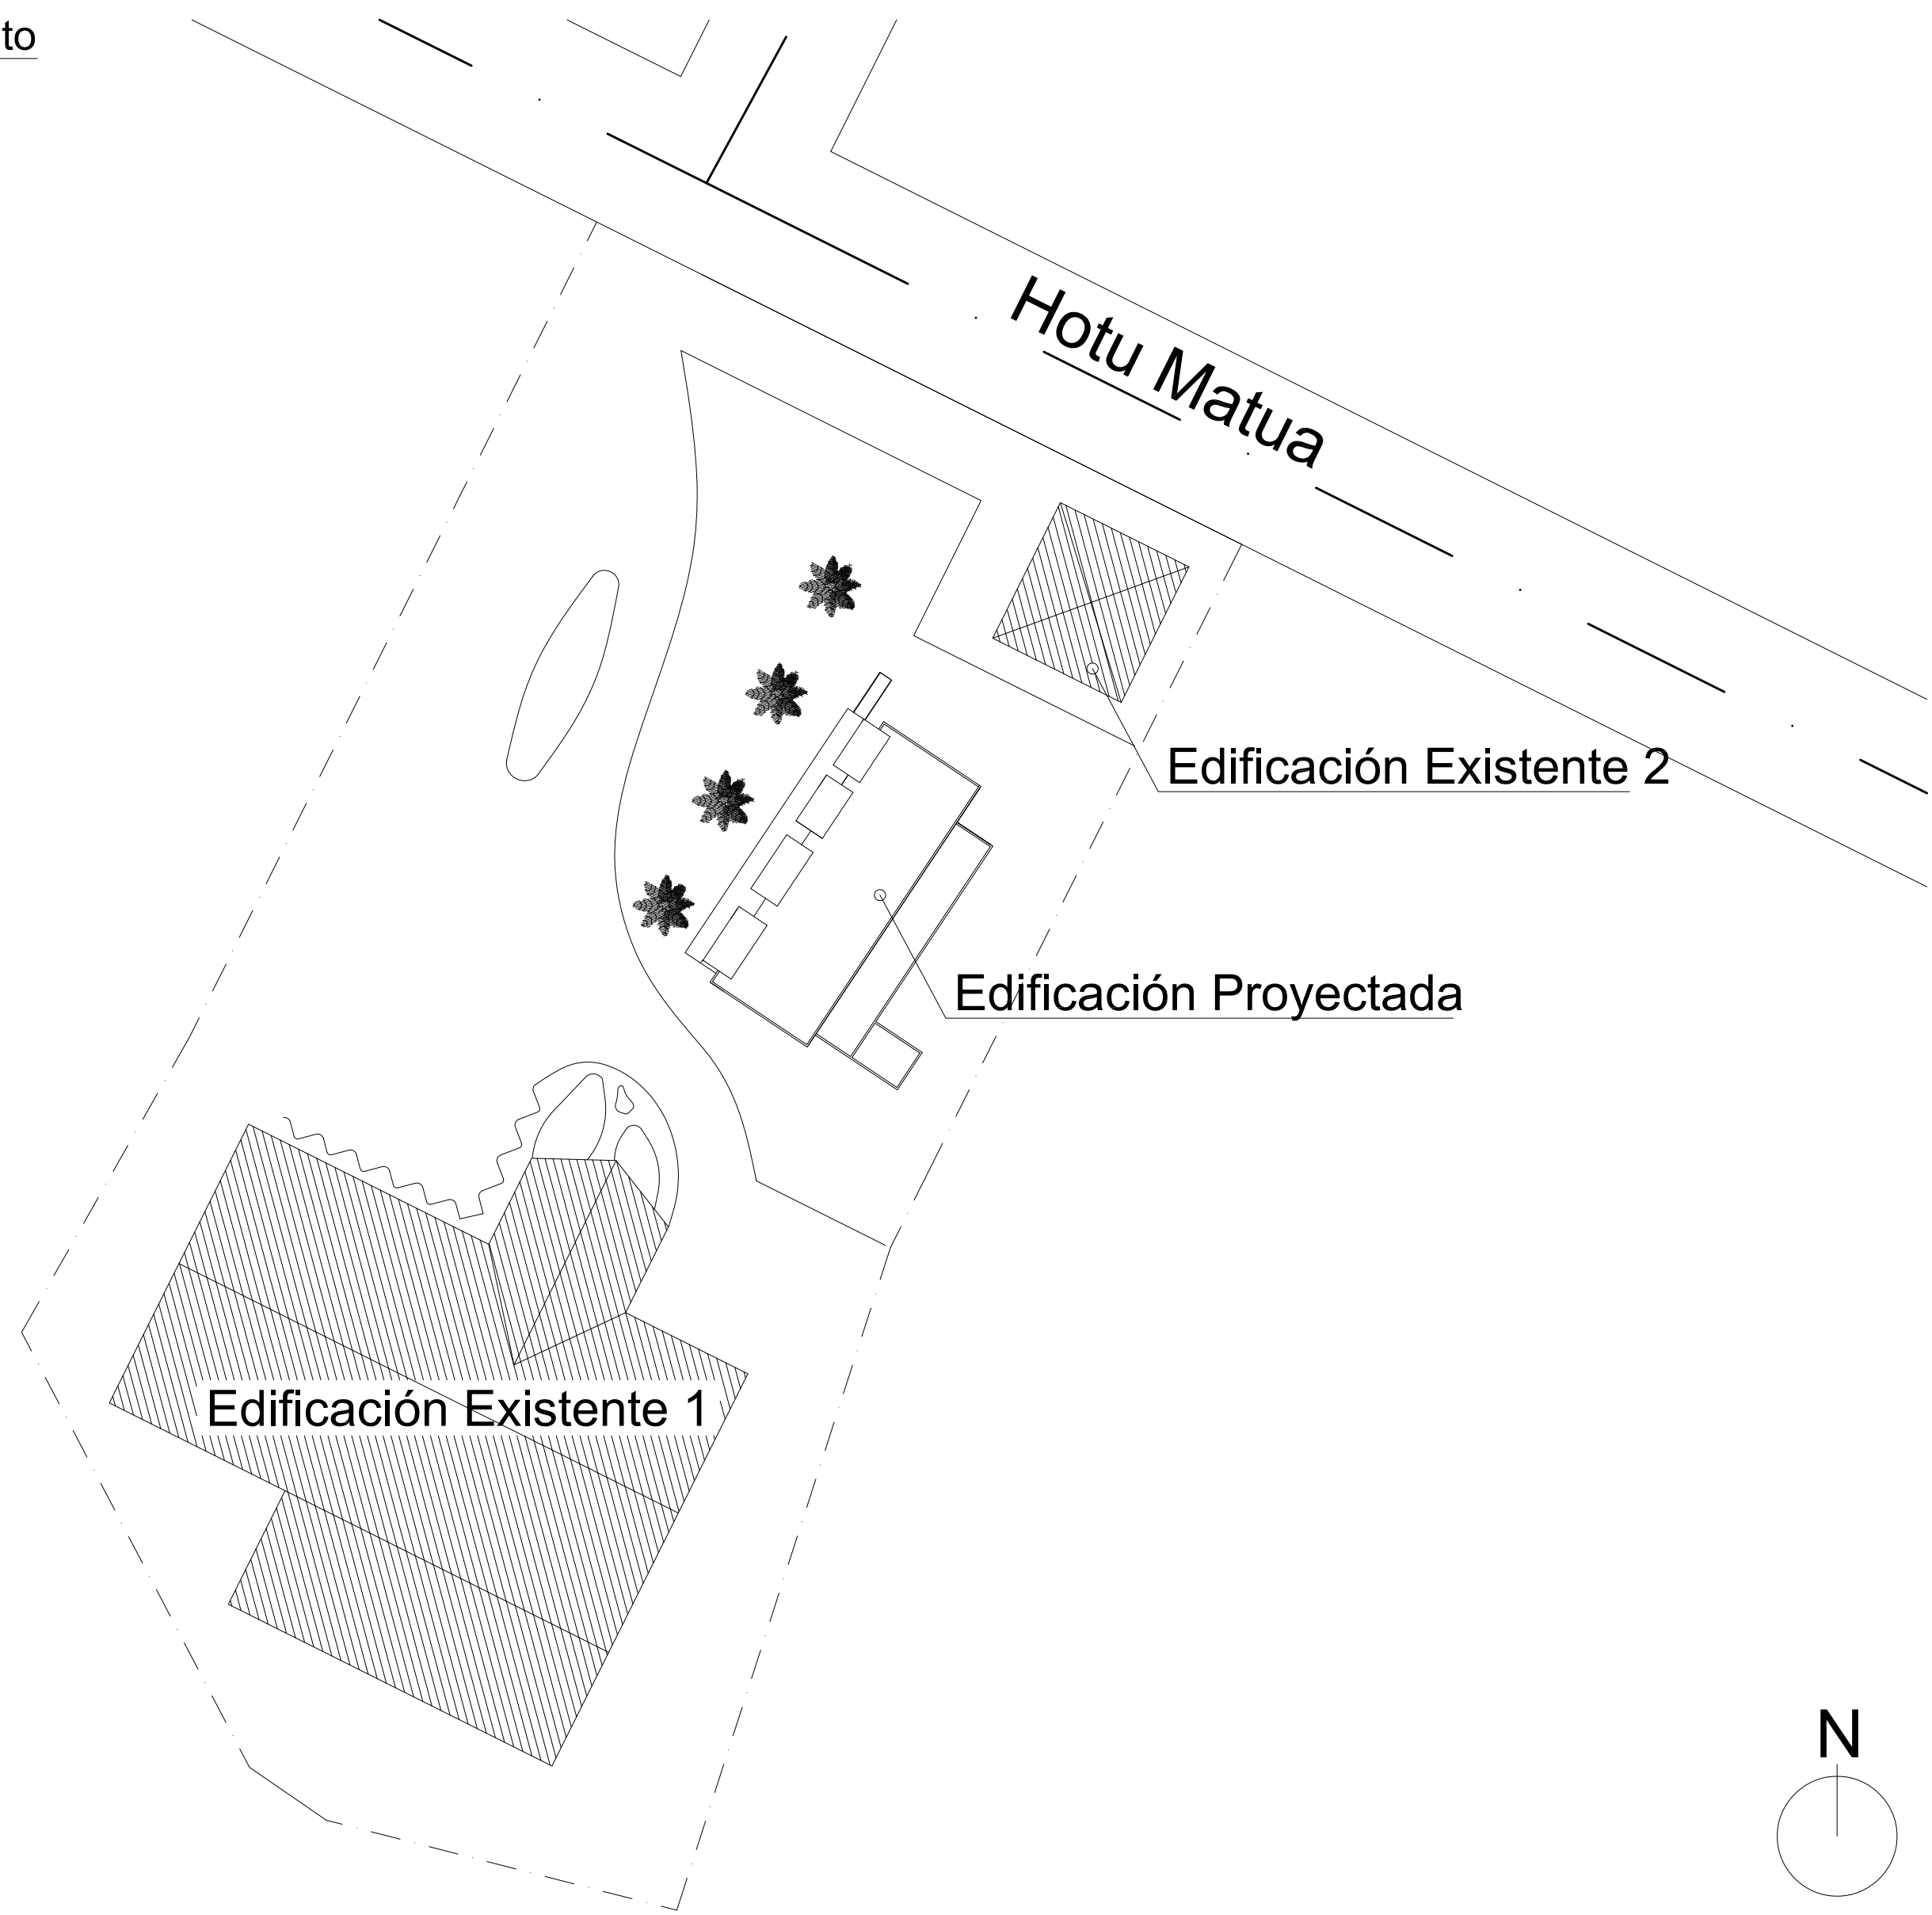

Planta de Situación
Escala 1:200

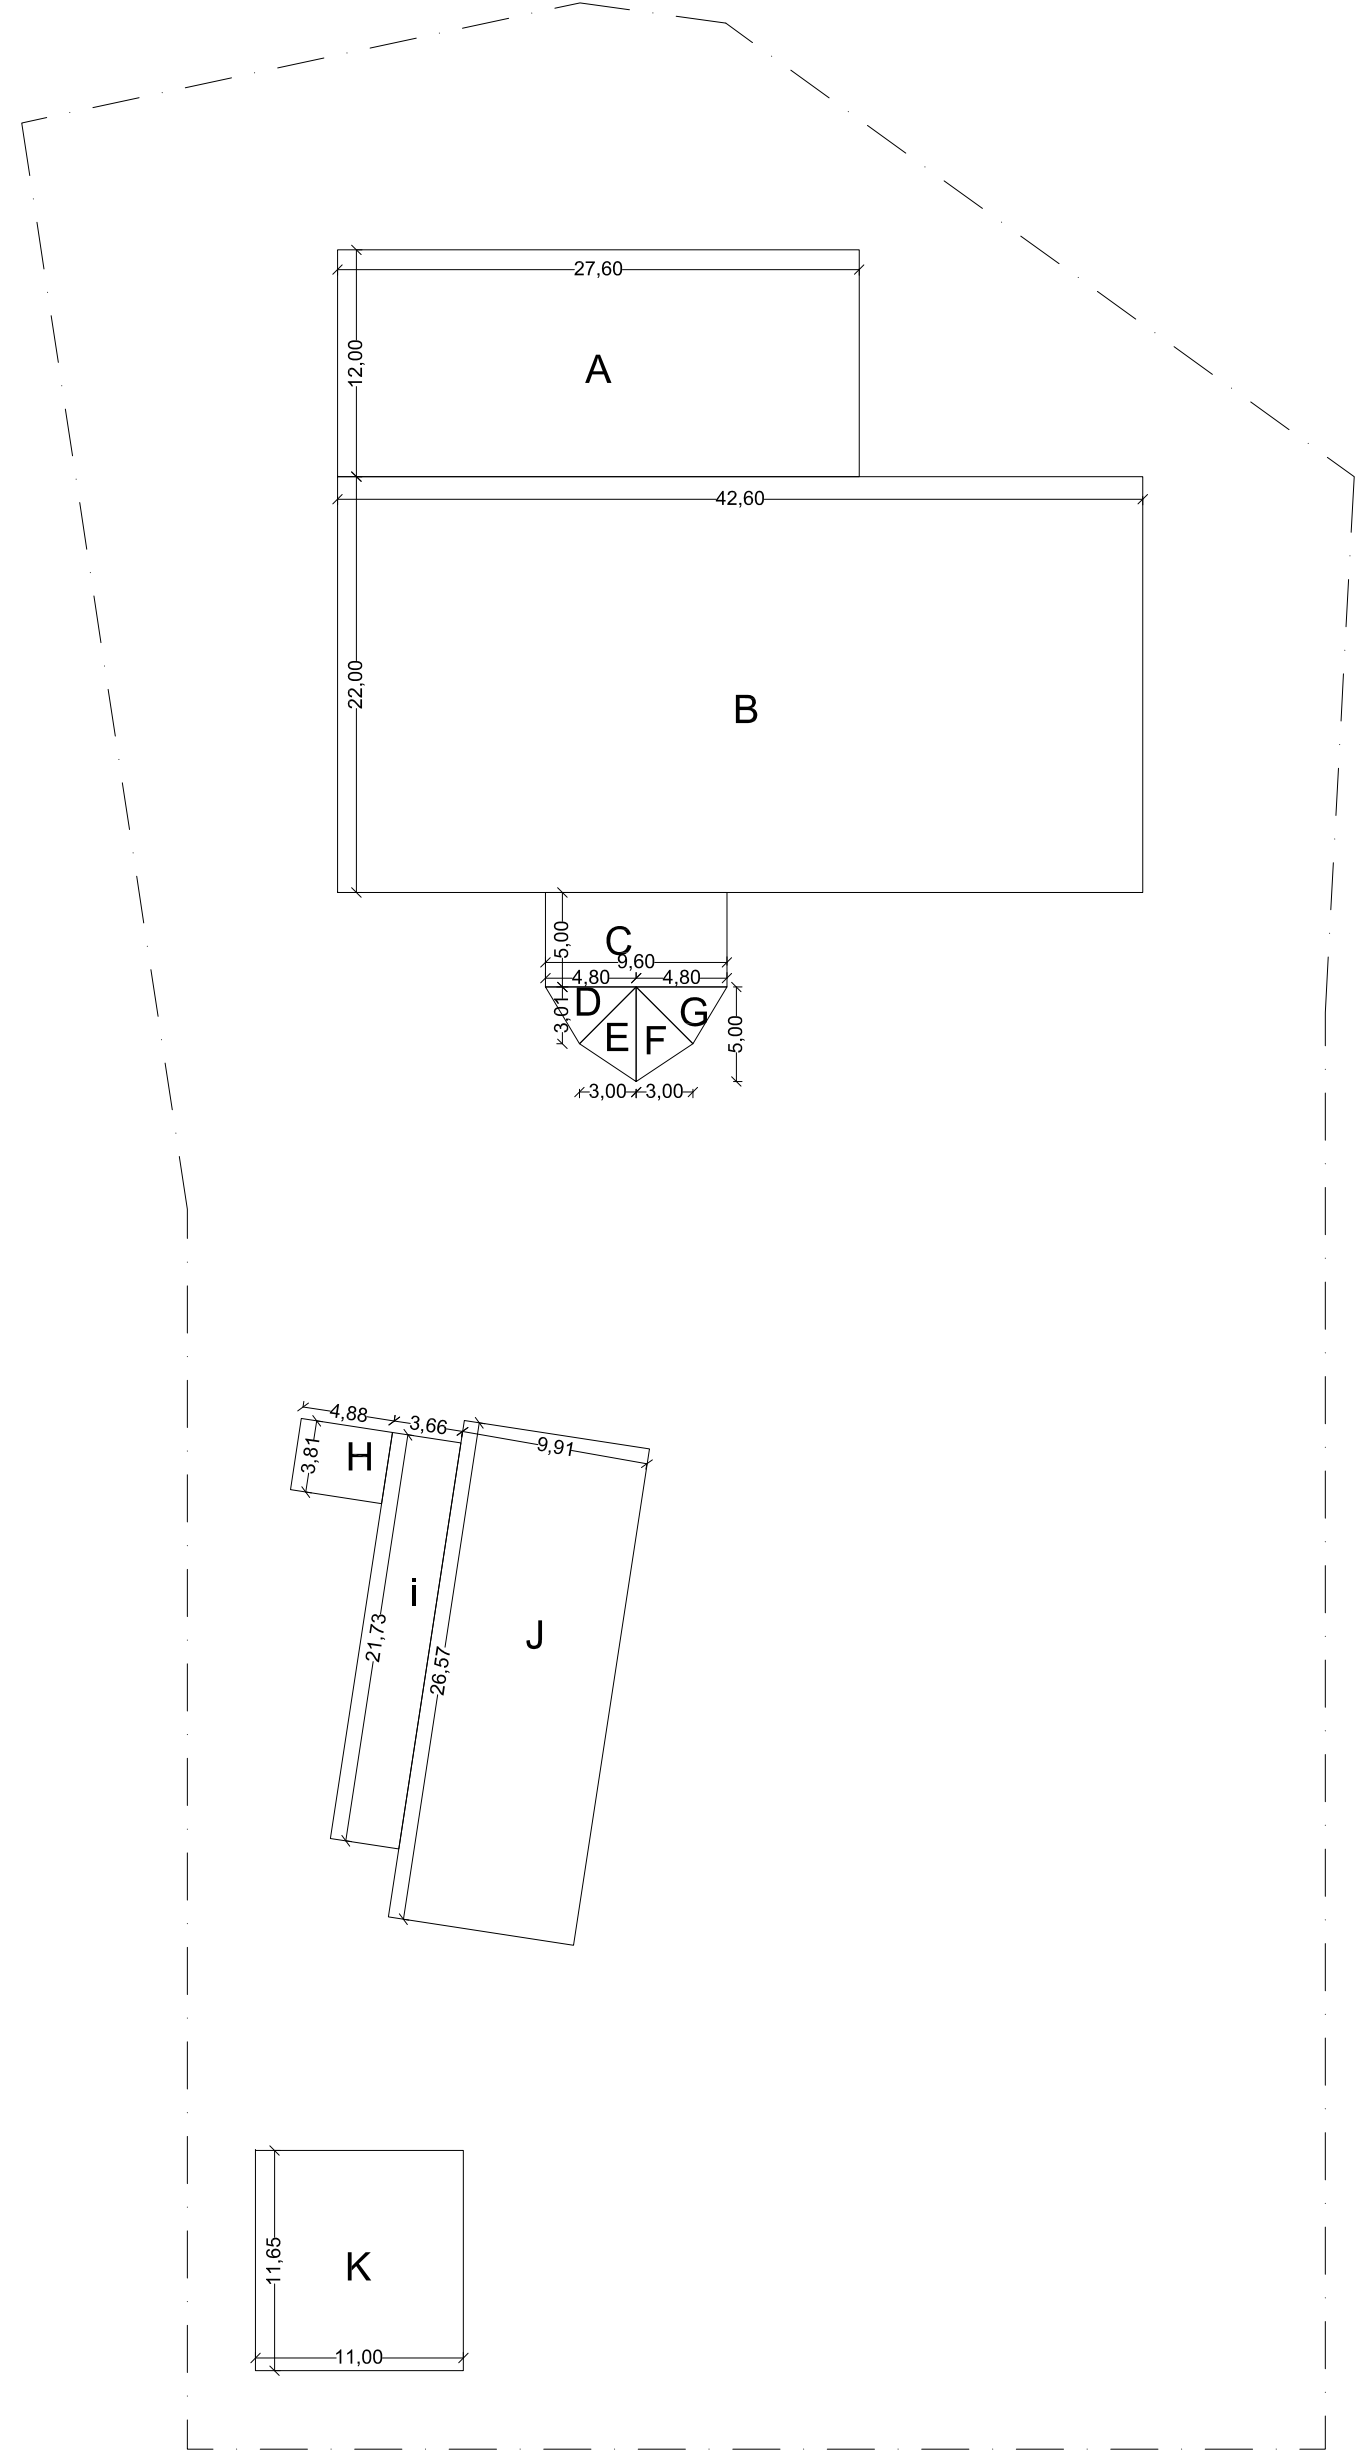

Cuadro de Superficies
Escala 1:500

RESUMEN DE SUPERFICIES	SUP. TOTAL EXISTENTE	SUP. TOTAL PROYECTADA	N° DE PISOS SOBRE N.N.T	
	1475,50	1836,93	1	
SUPERFICIE TOTAL TERRENO	COEF. CONSTRUCTIBILIDAD	1,00	COEF. DE OCUPACION DE SUELO	0,50
	7626,61	OCUPADO	0,19	OCUPADO
		PROYECTADO	0,24	PROYECTADO

CUADRO DE SUPERFICIES				
Existente	Área	Superficie	Destino	m² x Pers
A	27,60	x 12,00	331,20	
B	42,60	x 22,00	937,20	
C	9,60	x 5,00	48,00	
D	3,01	x 4,80	7,22	
E	5,00	x 3,00	7,50	
F	3,00	x 6,00	9,00	
G	4,80	x 3,01	7,22	
K	11,00	x 11,65	128,15	
Subtotal	1475,50			
Proyectada	Área	Superficie	Destino	m² x Pers
H	4,88	x 3,81	18,69	
I	3,84	x 21,73	79,63	
J	9,91	x 26,57	263,31	
Subtotal	361,43			
TOTAL	1836,93			

ESTUDIO CARGA DE OCUPACION				
Área	Superficie	Destino	m² x Pers	Carga
Existente	331,20	Superm.	3	110,40
A	42,60	Superm.	3	312,40
B	937,20	Superm.	3	16,00
C	48,00	Superm.	3	2,41
D	7,22	Superm.	3	2,50
E	7,50	Superm.	3	3,00
F	9,00	Superm.	3	2,41
G	7,22	Comercio	3	42,72
K	128,15	Sala V.	3	491,83
Subtotal	491,83			
Proyectada	Área	Superficie	Destino	m² x Pers
H	18,69	Oficina	10	1,86
I	79,63	Oficina	10	7,95
J	263,31	Oficina	10	26,33
Subtotal	36,14			
TOTAL	1836,93			518,16

CREACIUDAD
ARQUITECTURA


OBRA: PROYECTO
EDIFICIO CChC ISLA DE PASCUA
CNA DE COMPENSACION LOS ANDES

UBICACION: CLIENTE: C.C.A.F. de Los Andes
DIRECCION: Arquitecto P.U.C. - L.C.A. 4373
COMARCA: Providencia 2053 de 1307 F. 244-44-44
ROL: tomanfajardo@creaciudad.cl


ARQUITECTO: Tomás Fajardo Cabello

CONTENIDO:
Plantas de Ubicación
Emplazamiento y Situación
Cuadro de Superficie
Carga Ocupación
Fecha: Dibujo: Escala: Indicada

Lamina: 1 de 4
A1
Escala: Indicada

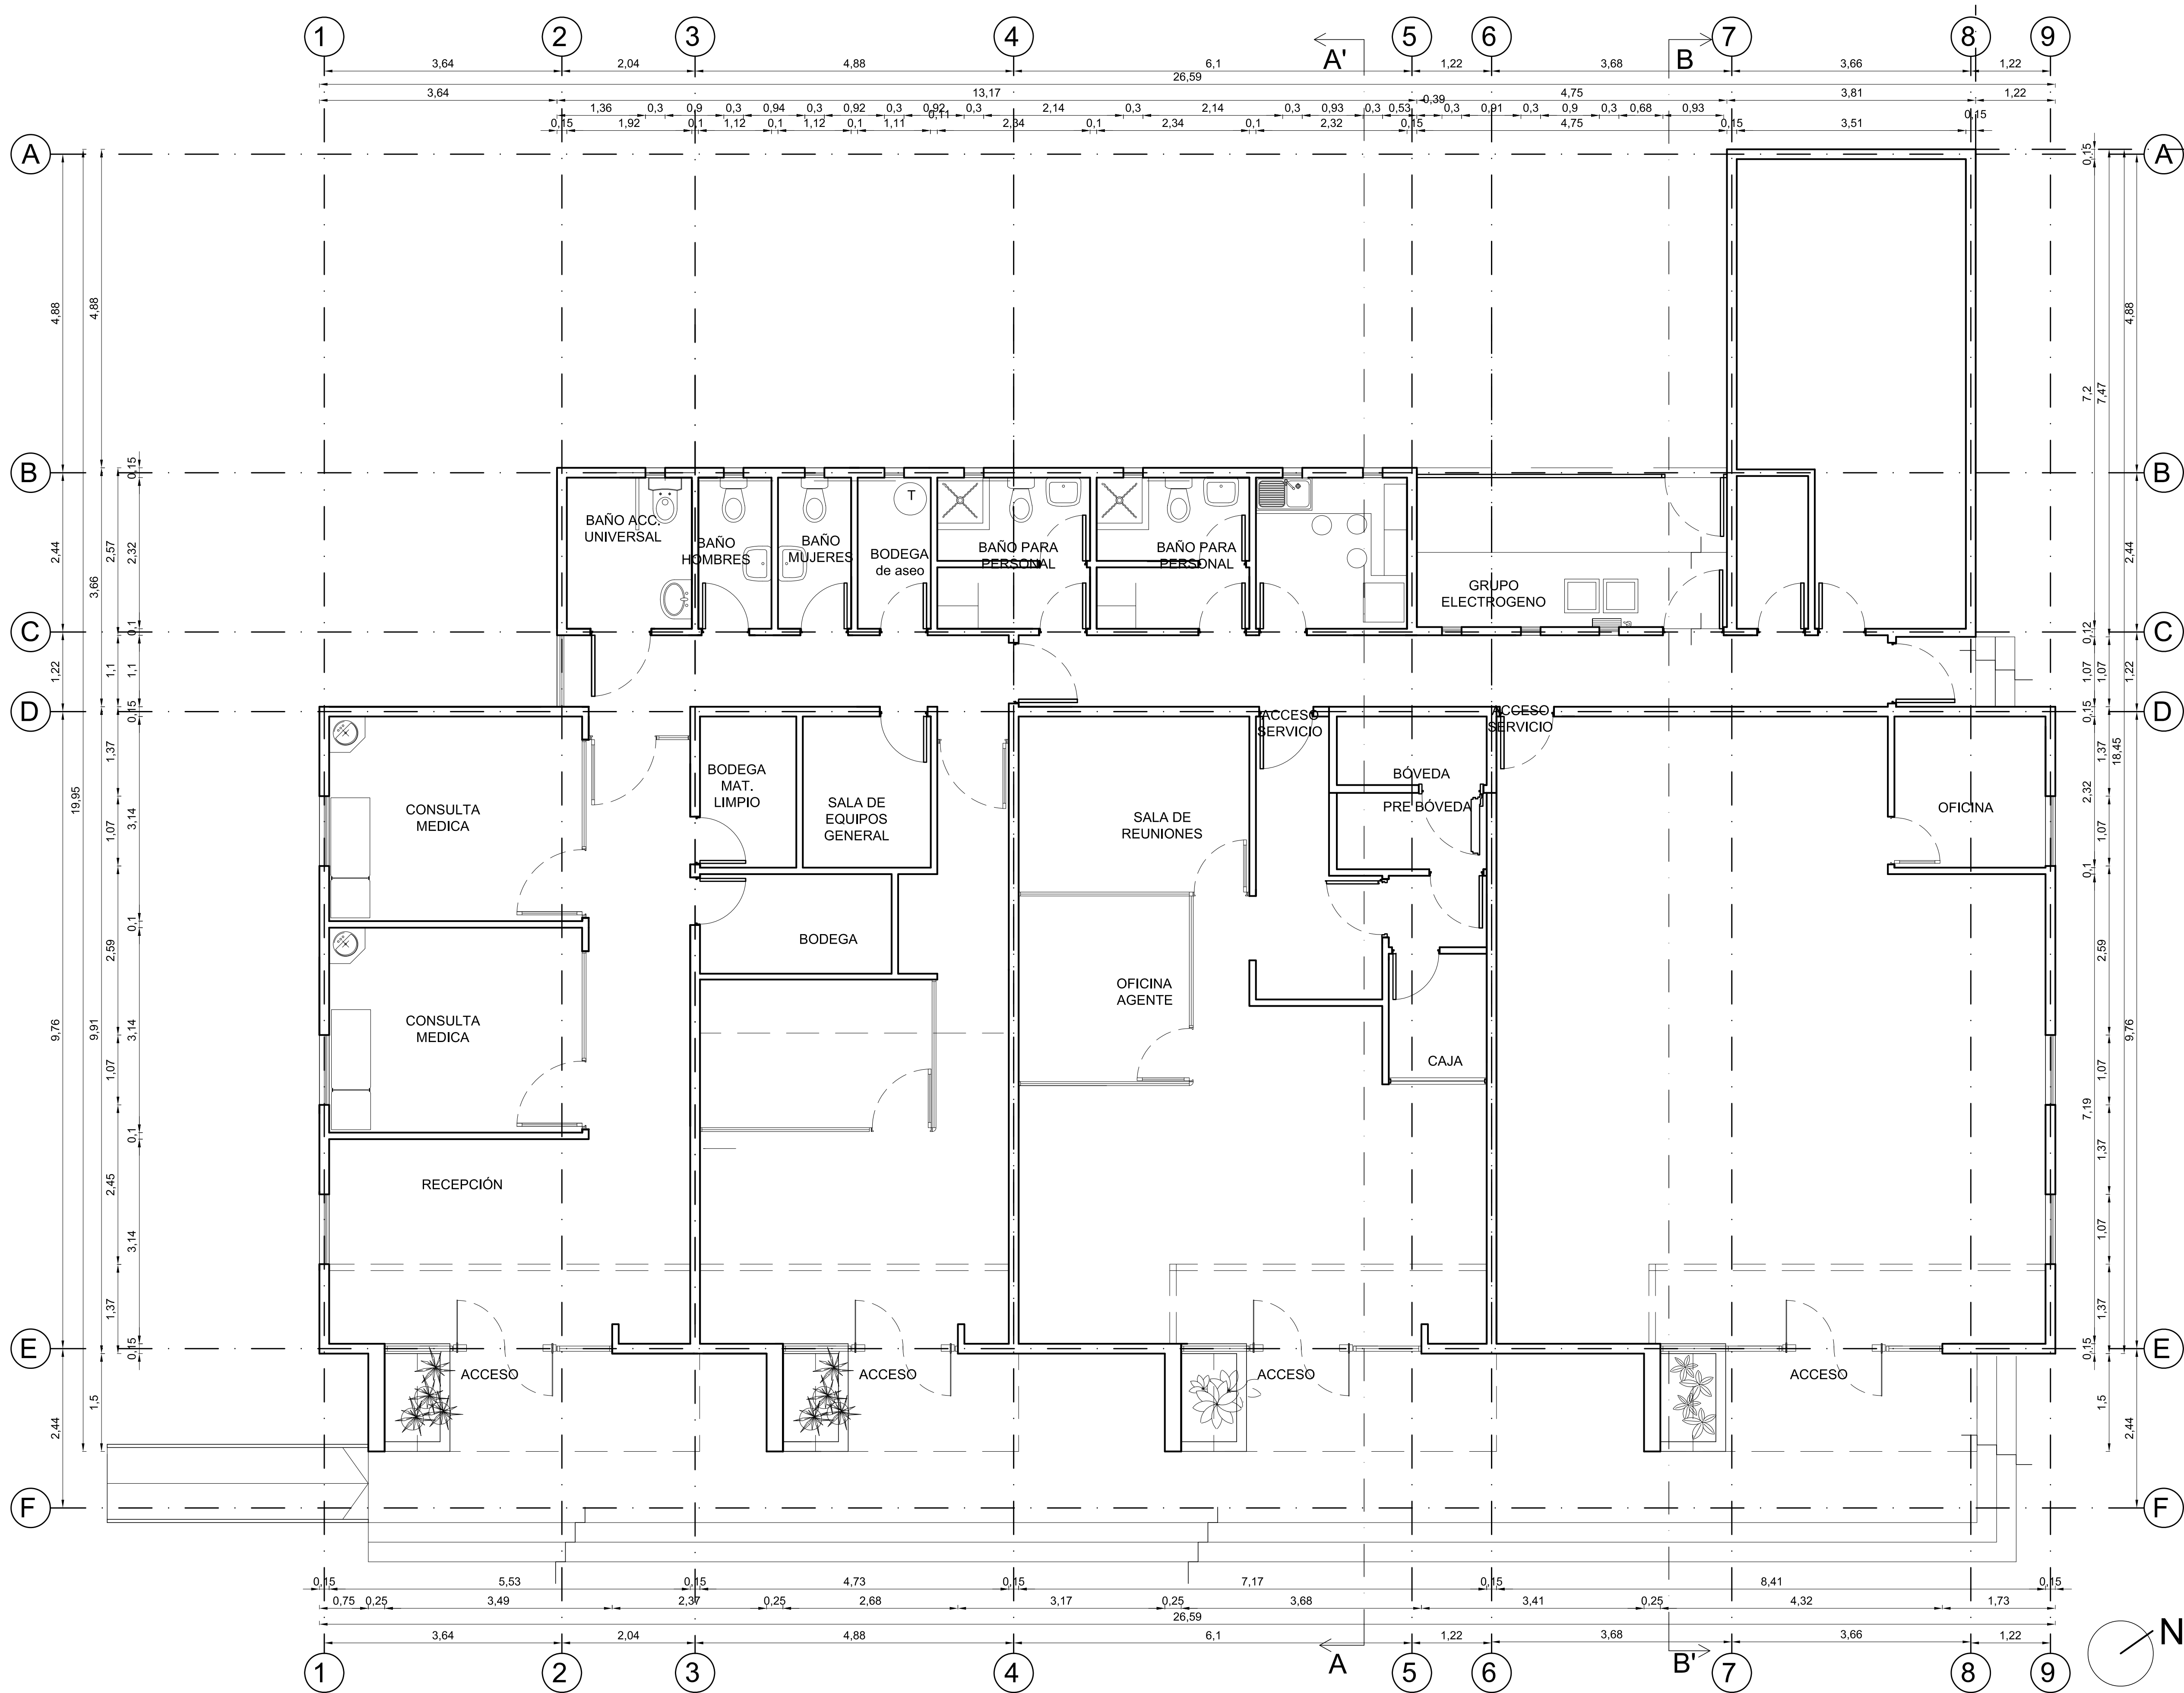


Planta de Arquitectura
Escala 1:50

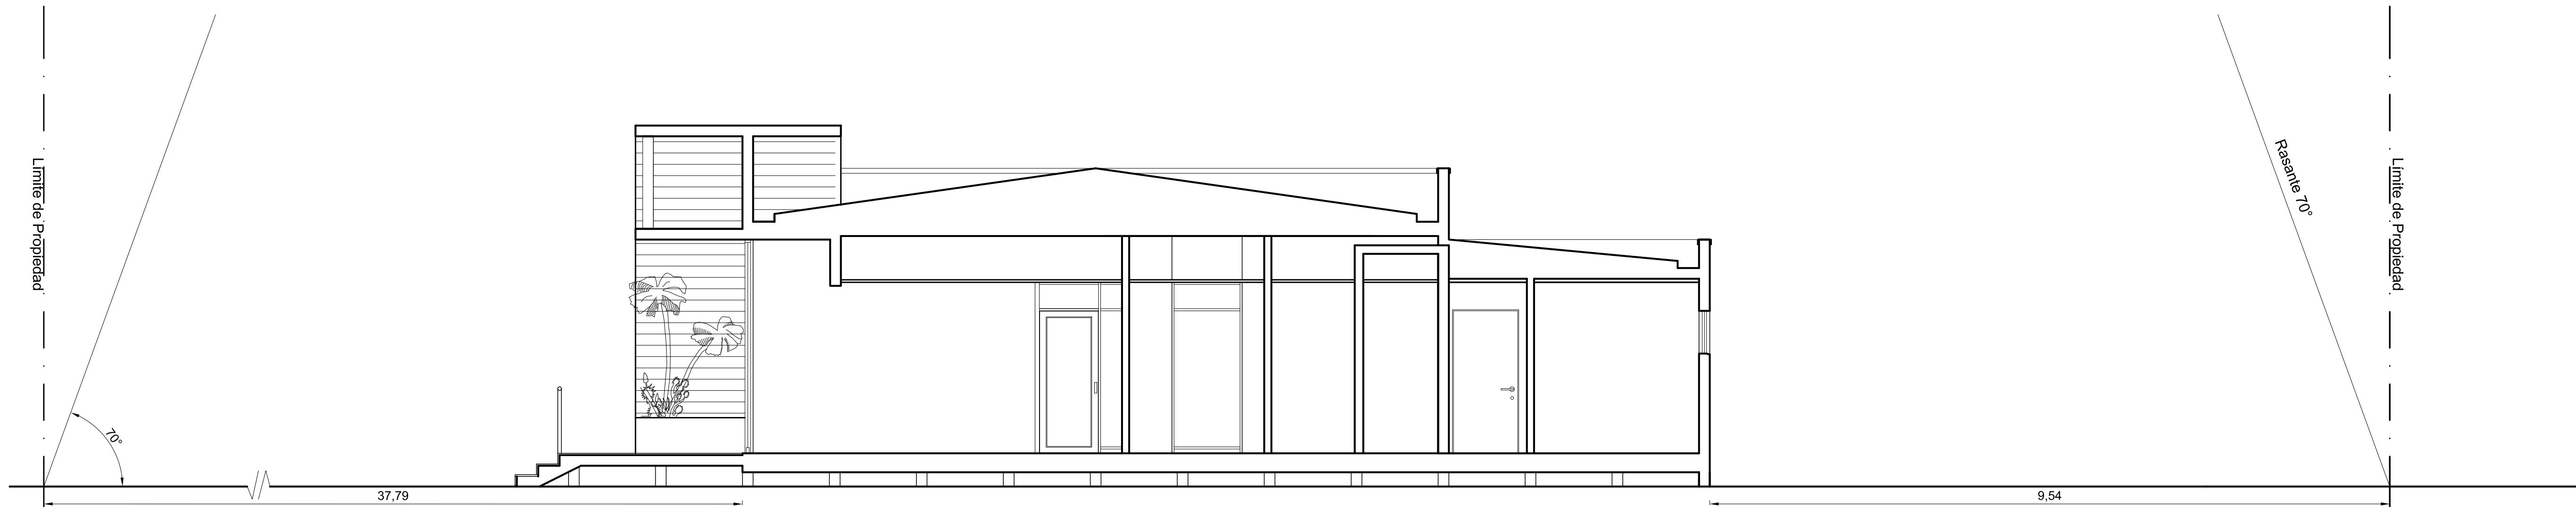


Corte A-A
Escala 1:50

CREACIUDAD ARQUITECTURA		
OBRA: PROYECTO EDIFICIO CCCh ISLA DE PASCUA CAJA DE COMPENSACION LOS ANDES		
UBICACION:	CLIENTE:	ARQUITECTO:
	C.C.A.F. de Los Andes	Tomás Fajardo Cabello
	DIRECCION: Arquitecto P.U.C. - L.C.A. 4373	Arquitecto P.U.C. - L.C.A. 4373
	COMANA: Providencia 2053 del 1307 F. 244 44 44	COMANA: Providencia 2053 del 1307 F. 244 44 44
	ROL: ROL	ROL
CONTENIDO: Planta Proyecto de Arquitectura Corte A-A	Lamina: 2 de 4	
Fecha:	Dibujo:	A2 Escala: Indicada

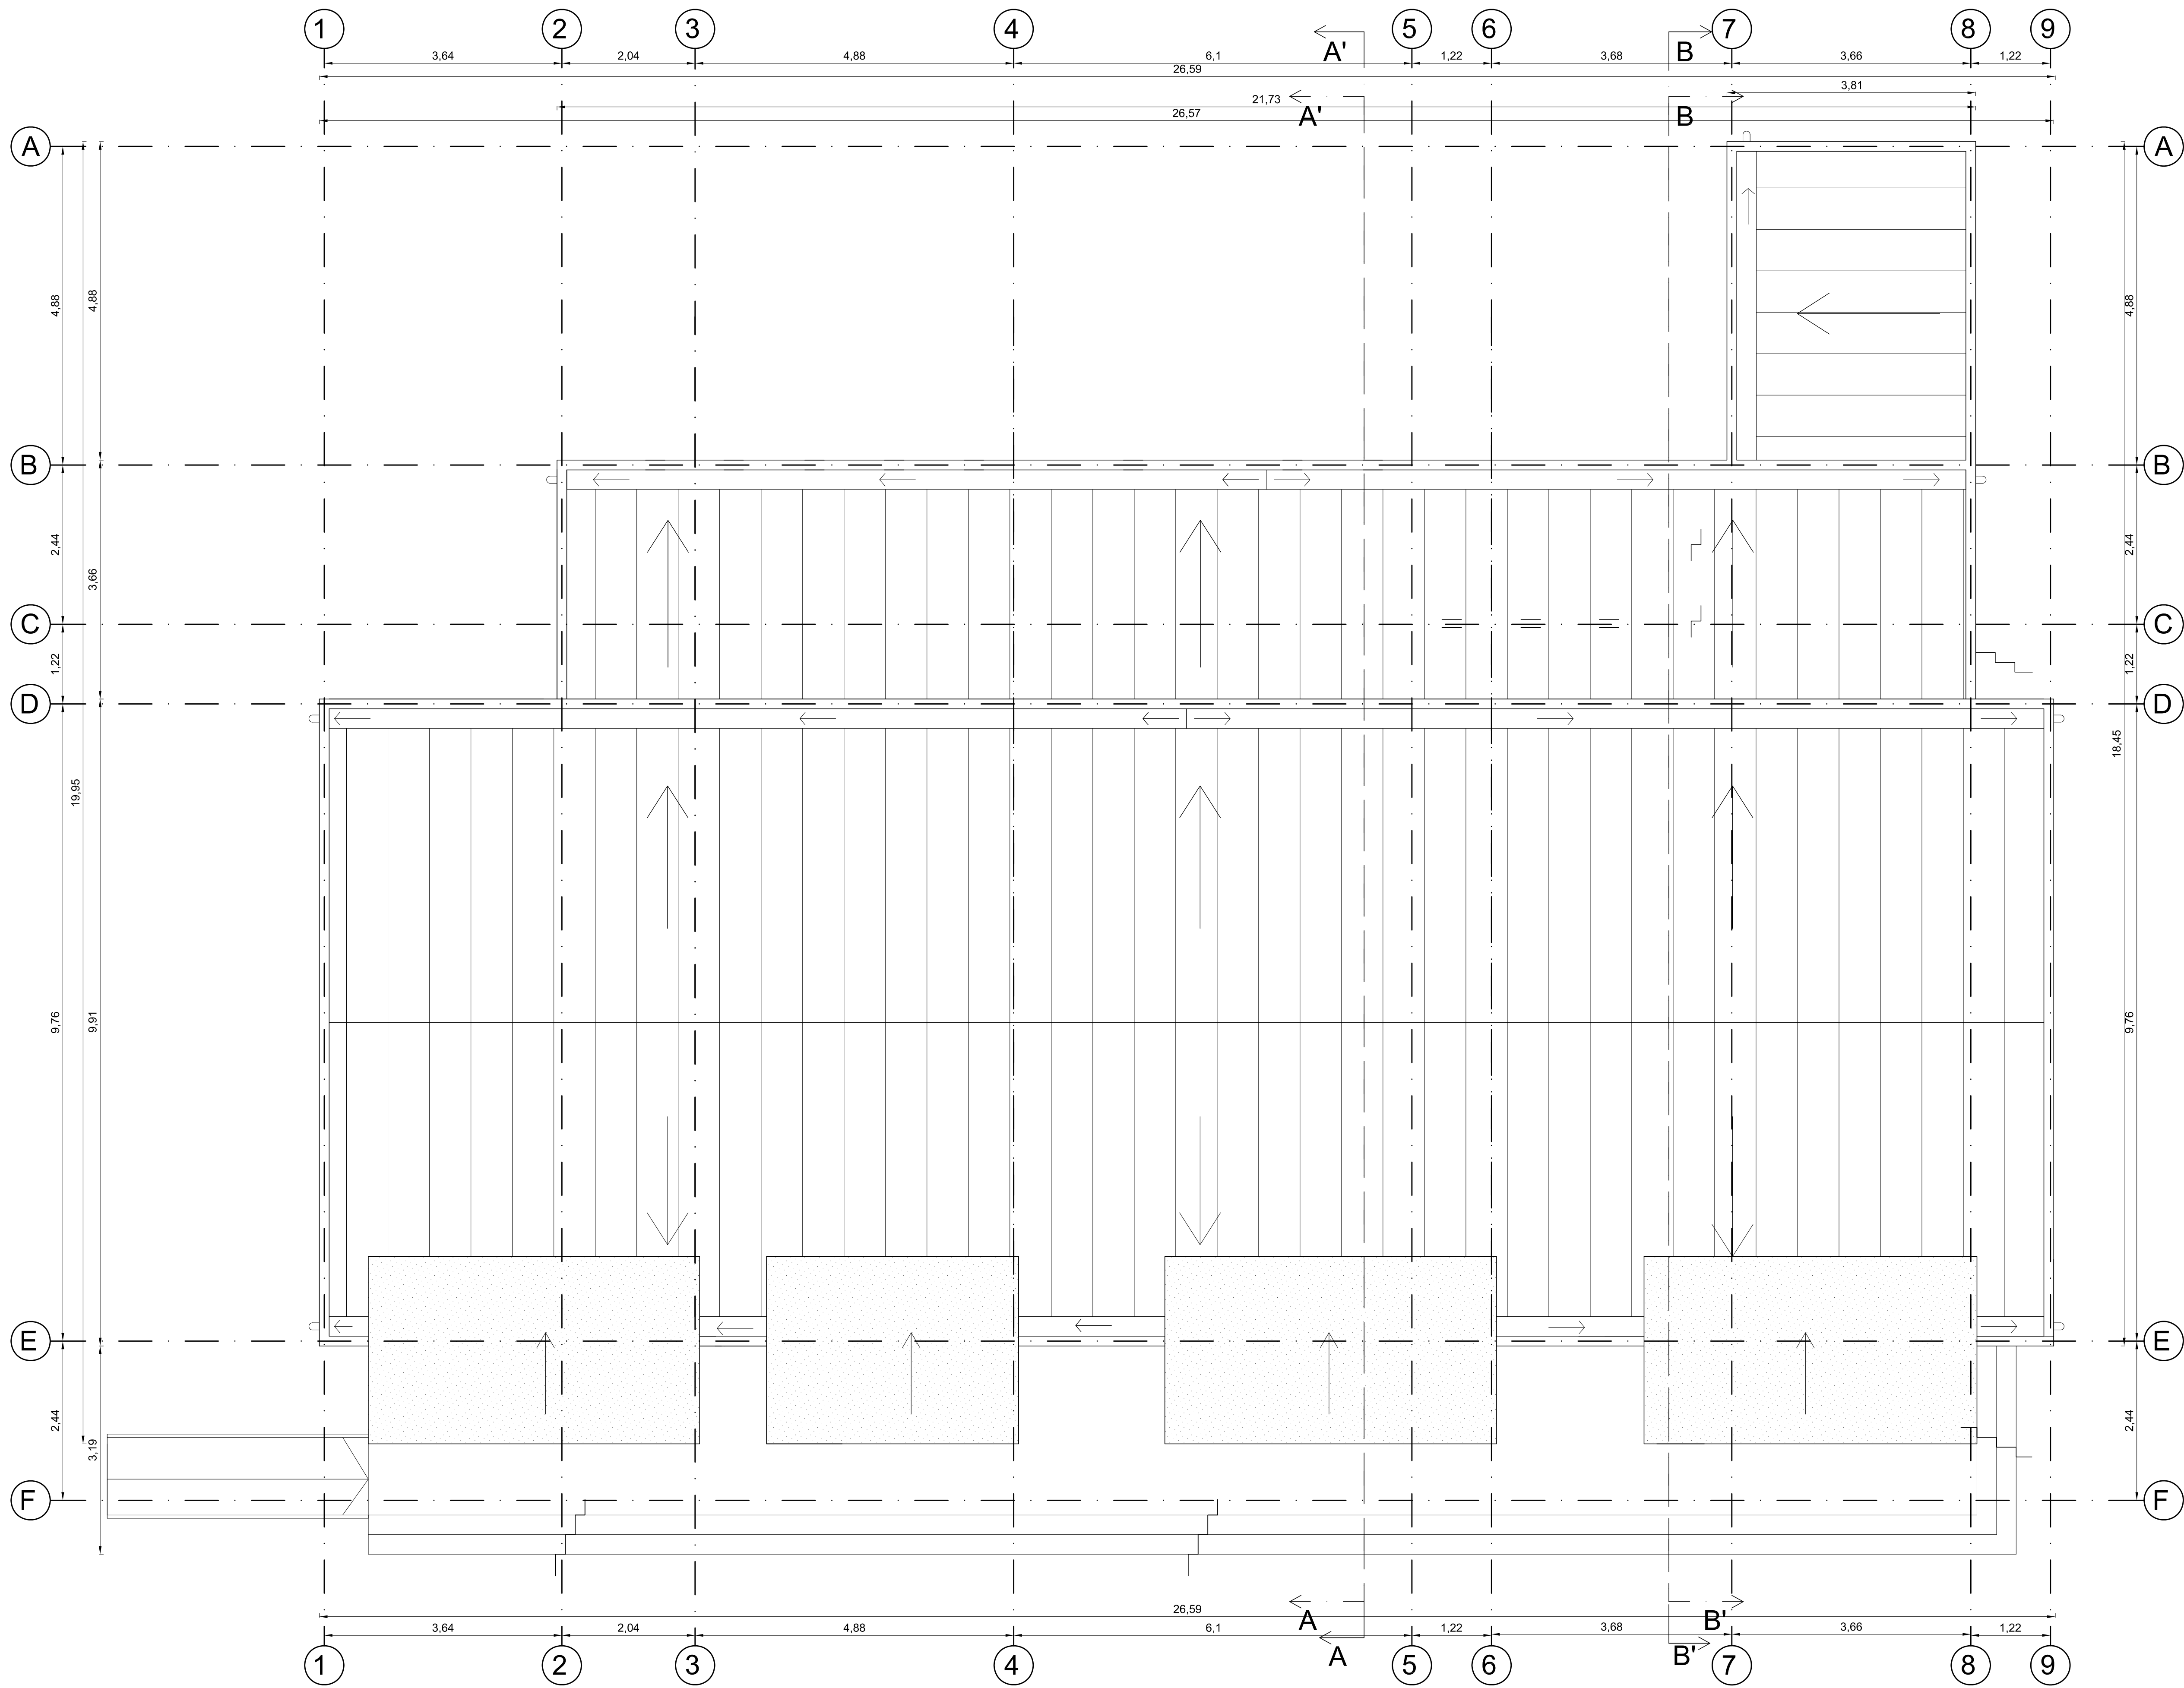


Planta de Arquitectura
Escala 1:50

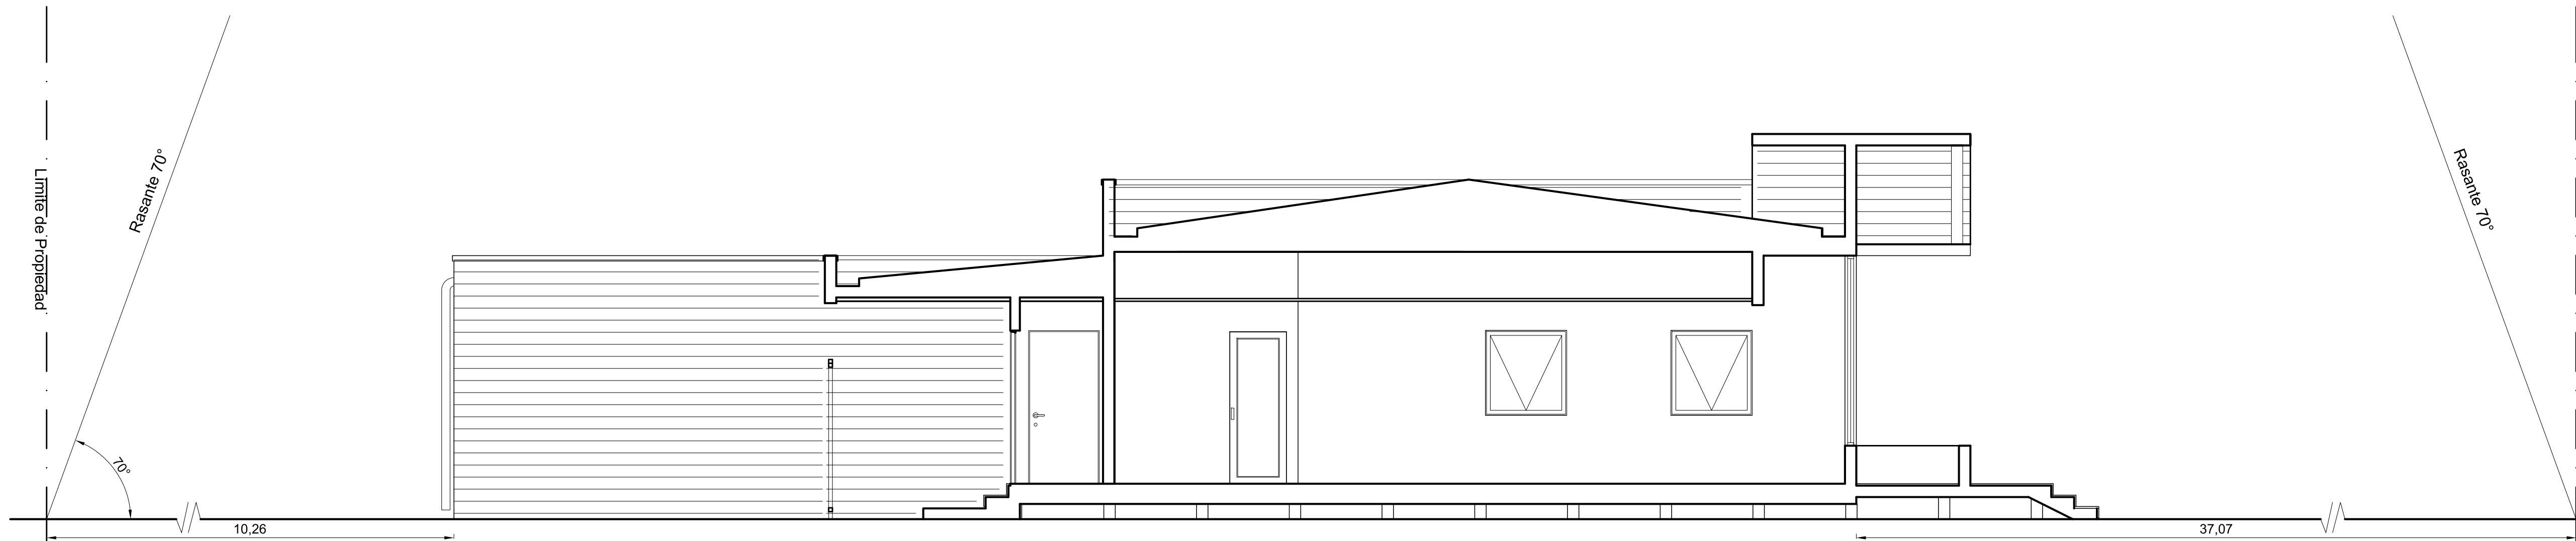


Corte B-B
Escala 1:50


CREACIUDAD ARQUITECTURA		
OBRA: PROYECTO EDIFICIO CCCh ISLA DE PASCUA CAJA DE COMPENSACION LOS ANDES		
UBICACION:	CLIENTE:	ARQUITECTO:
	C.C.A.F. de Los Andes	Tomás Fajardo Cabello
	DIRECCION: Arquitecto P.U.C. - L.C.A. 4373	Arquitecto P.U.C. - L.C.A. 4373
	COMUNA: Providencia 2053 of. 1307 F. 244 44 44	tomafajardo@creaciudad.cl
CONTENIDO: Planta de techos Corte B-B		Lamina: 3 de 4
Fecha:		Dibujo:
		Escala: Indicada

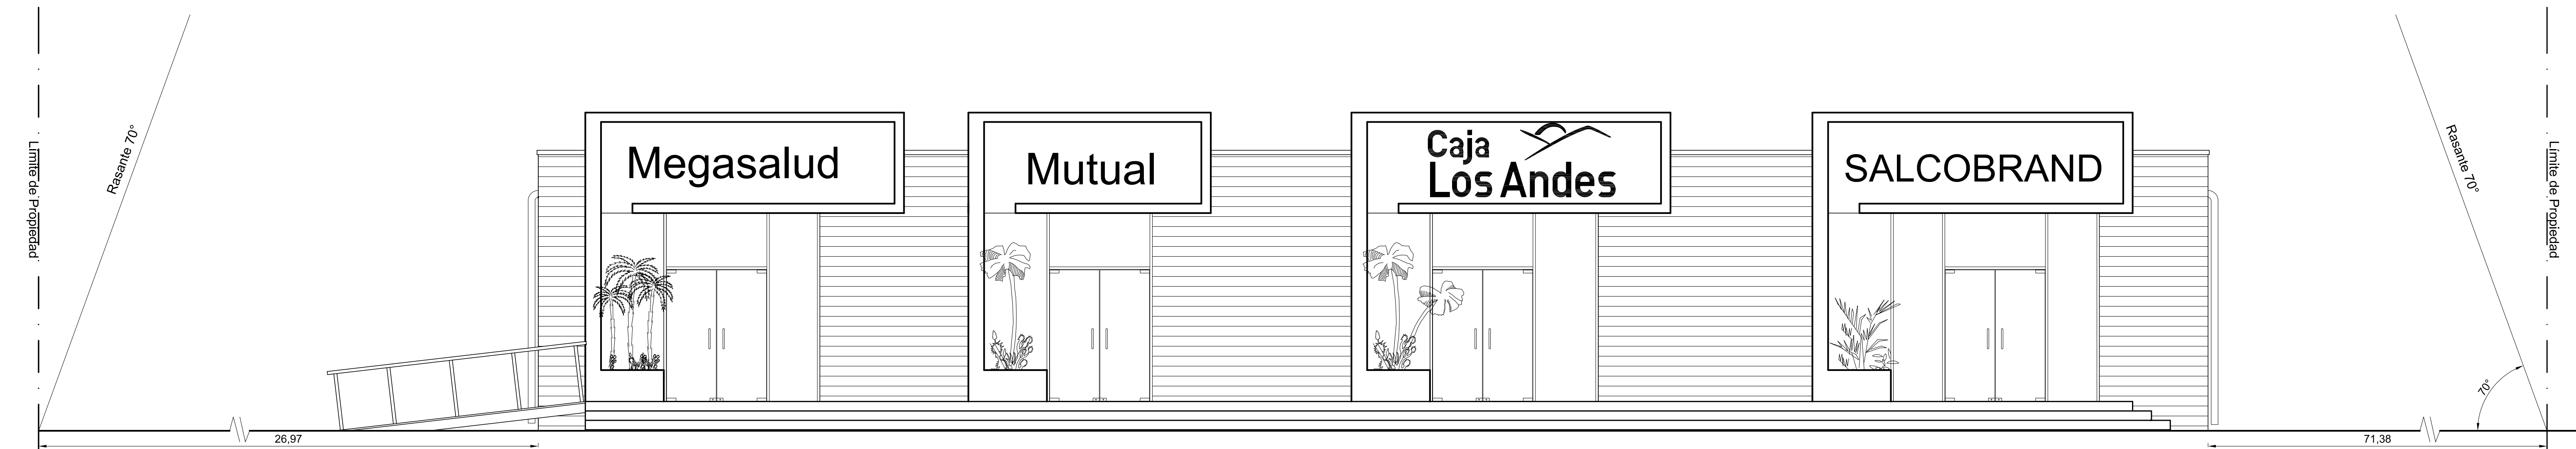


Elevación Este
Escala 1:50

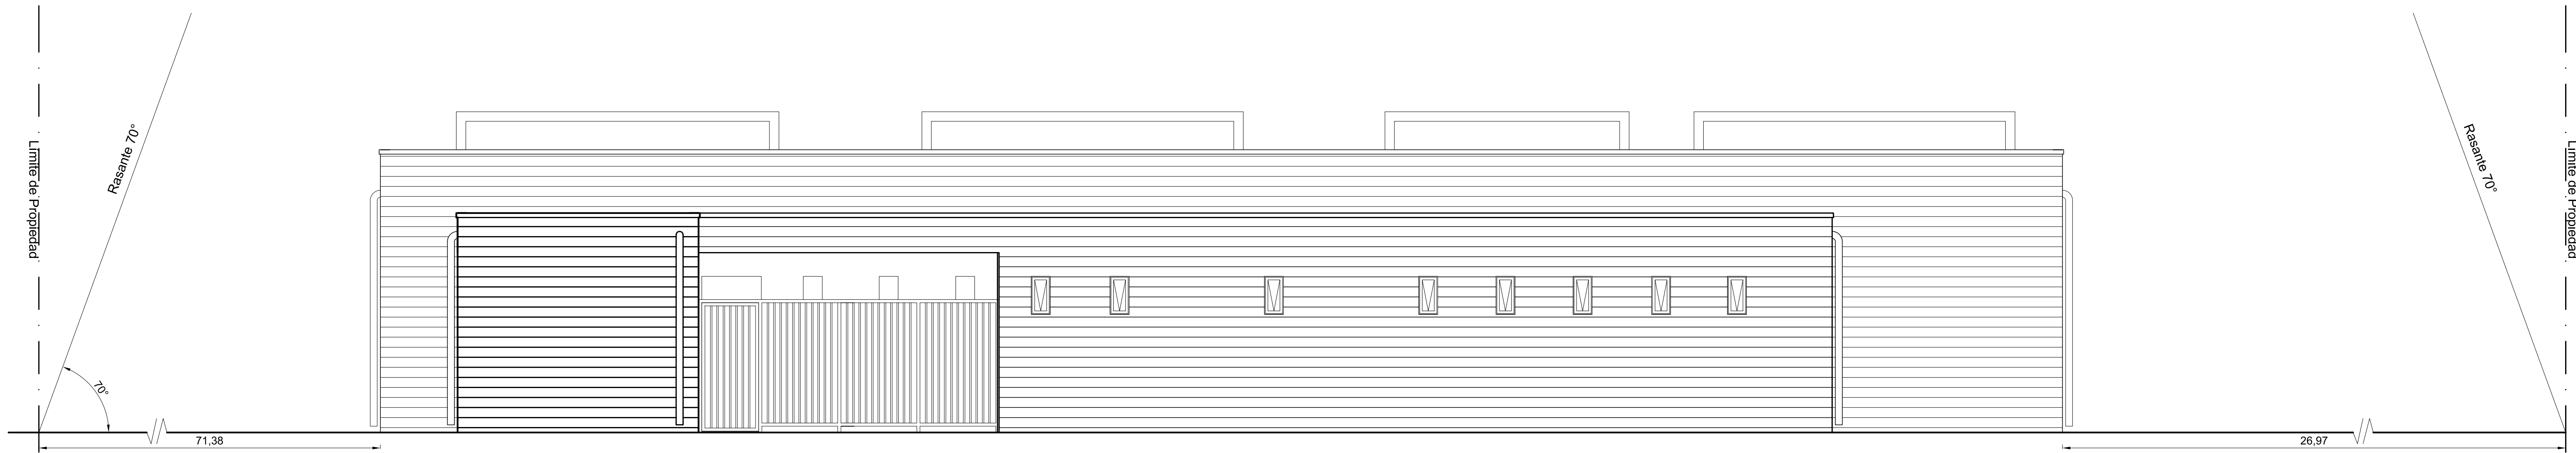

Elevación Oeste
Escala 1:50

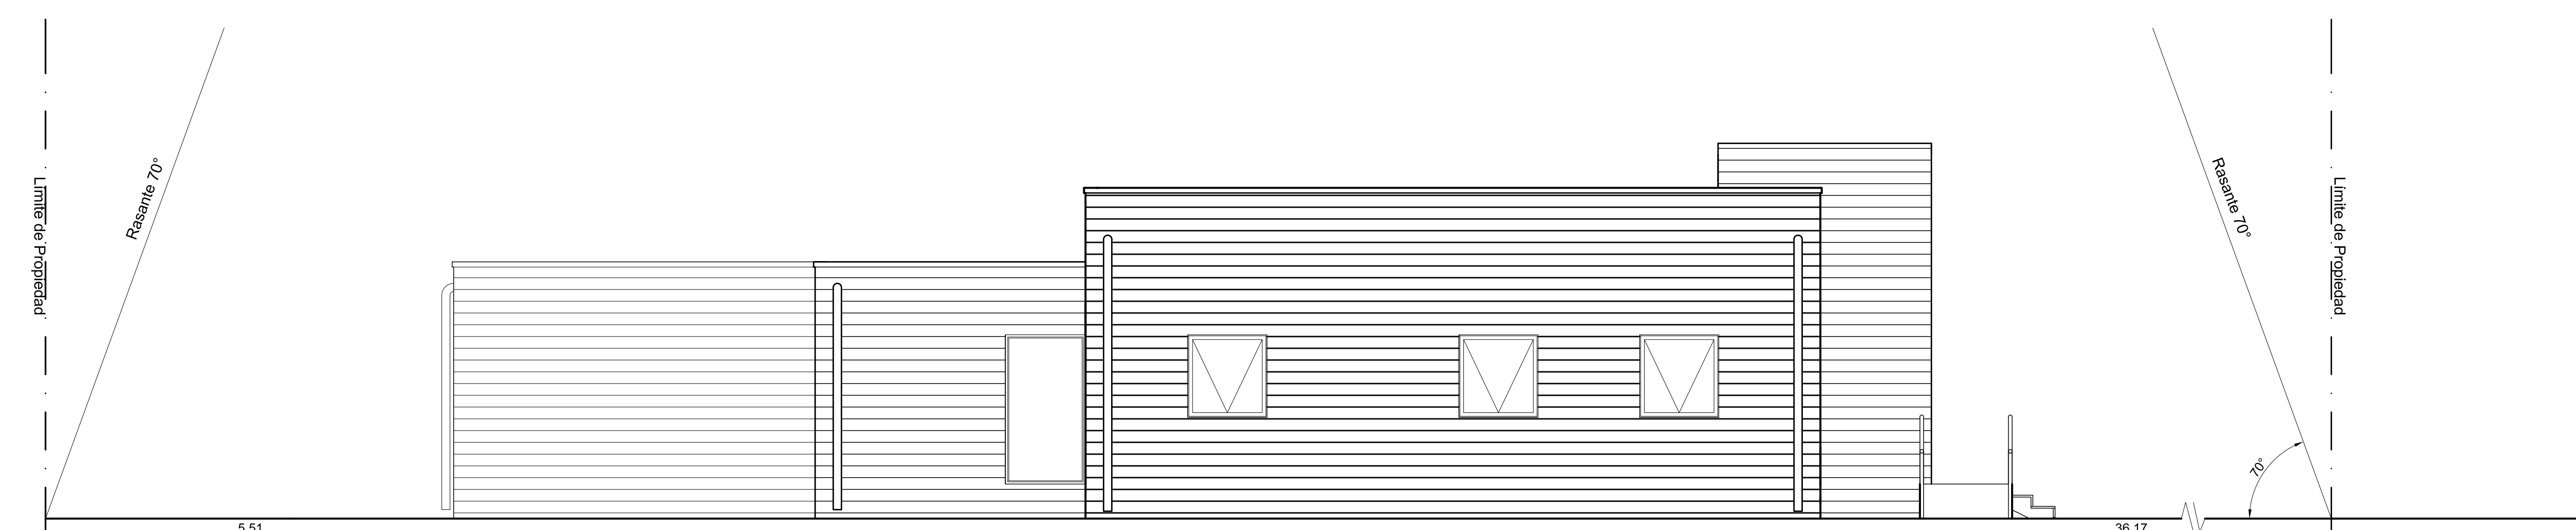

Elevación Sur
Escala 1:50

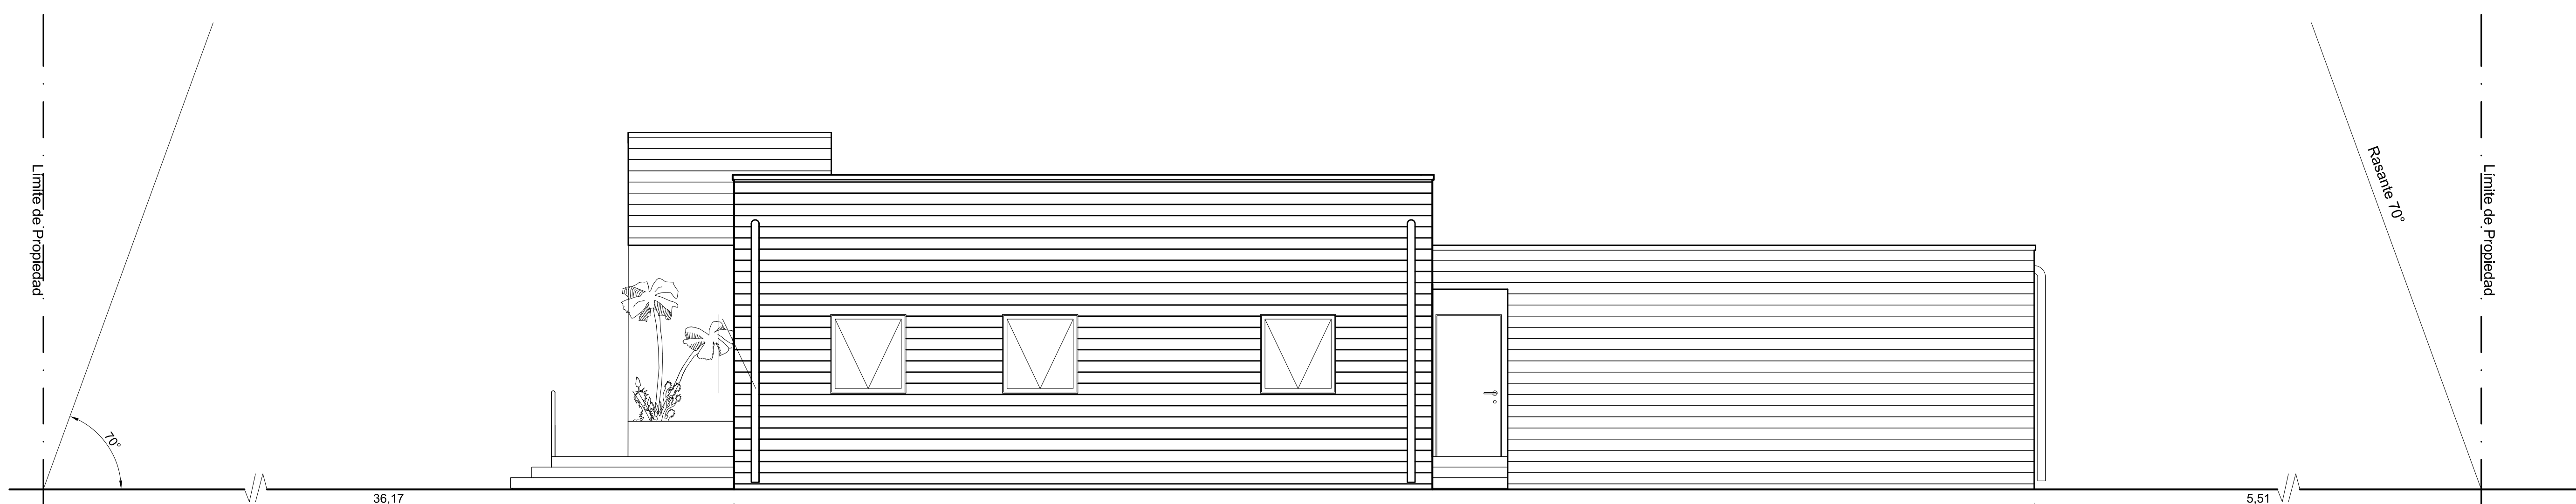

Elevación Norte
Escala 1:50

CREACIUDAD ARQUITECTURA		
OBRA: PROYECTO EDIFICIO CCbC ISLA DE PASCUA CAJA DE COMPENSACION LOS ANDES		
UBICACION:	CLIENTE:	ARQUITECTO:
	C.C.A.F. de Los Andes	Tomás Fajardo Cabello
	DIRECCION: Arquitecto P.L.L.C. - L.C.A. 4373	Arquitecto P.L.L.C. - L.C.A. 4373
	COMUNA: Providencia 2953 of. 1307 F.F. 244 44 44	Providencia 2953 of. 1307 F.F. 244 44 44
	ROL:	tomafajardo@cccbol.cl
CONTENIDO: Elevaciones	Lamina: 4 de 4 A4 Escala: Indicada	
Fecha:	Dibujo:	