



NOMBRE PROYECTO:

CENTRO RECREACIONAL BEAUCHEFF



Juana de Arco 2012, oficina 31, Providencia
+562 2946 1389 / info@ccciudad.cl

DIRECCIÓN CENTRO:

Calle Beaucheff N° 3500, Pedro Aguirre Cerda

ROL SII: 2791 - 1

PROPIETARIO:

CAJA DE COMPLENSACIÓN DE LOS ANDES

CONTENIDO LAMINA:

	NOMBRE	FECHA
DIB	JMA	12/08/2022
REV		
ESC	INDICADAS	

Lamina: 01 de 08

A01

CONTENIDO LAMINA:
Plano de Emplazamiento

FIRMA PROPIETARIO / REPRESENTANTE LEGAL

C.C.A.F. de Los Andes
FIRMA ARQUITECTO

Tomás Fajardo Cabello
Arquitecto PUC - I.C.A. 8373
tomASFajardo@cfajardo.cl

FIRMA REVISOR MUNICIPAL

D.O.M. Municipalidad


CODIGO:
CRB - 2022 - RCRB

VERSIONES			
	NOMBRE	FECHA	EDICION
DIB	JMA	18-08-22	1.0
EDI			
EDI			
EDI			
EDI			
EDI			
EDI			
EDI			
EDI			
EDI			


OBRA:
CENTRO RECREACIONAL BEAUCHEFF
CAJA DE COMPENSACION LOS ANDES

DIRECCION : Beaucheff n°3500
COMUNA : Pedro Aguirre Cerda
ROL : 2971 - 1


	NOMBRE	FECHA	Lamina: 02 de 08
DIB	JMA	18-08-22	A02
REV	TFC	08-22	
ESC	INDICADAS		

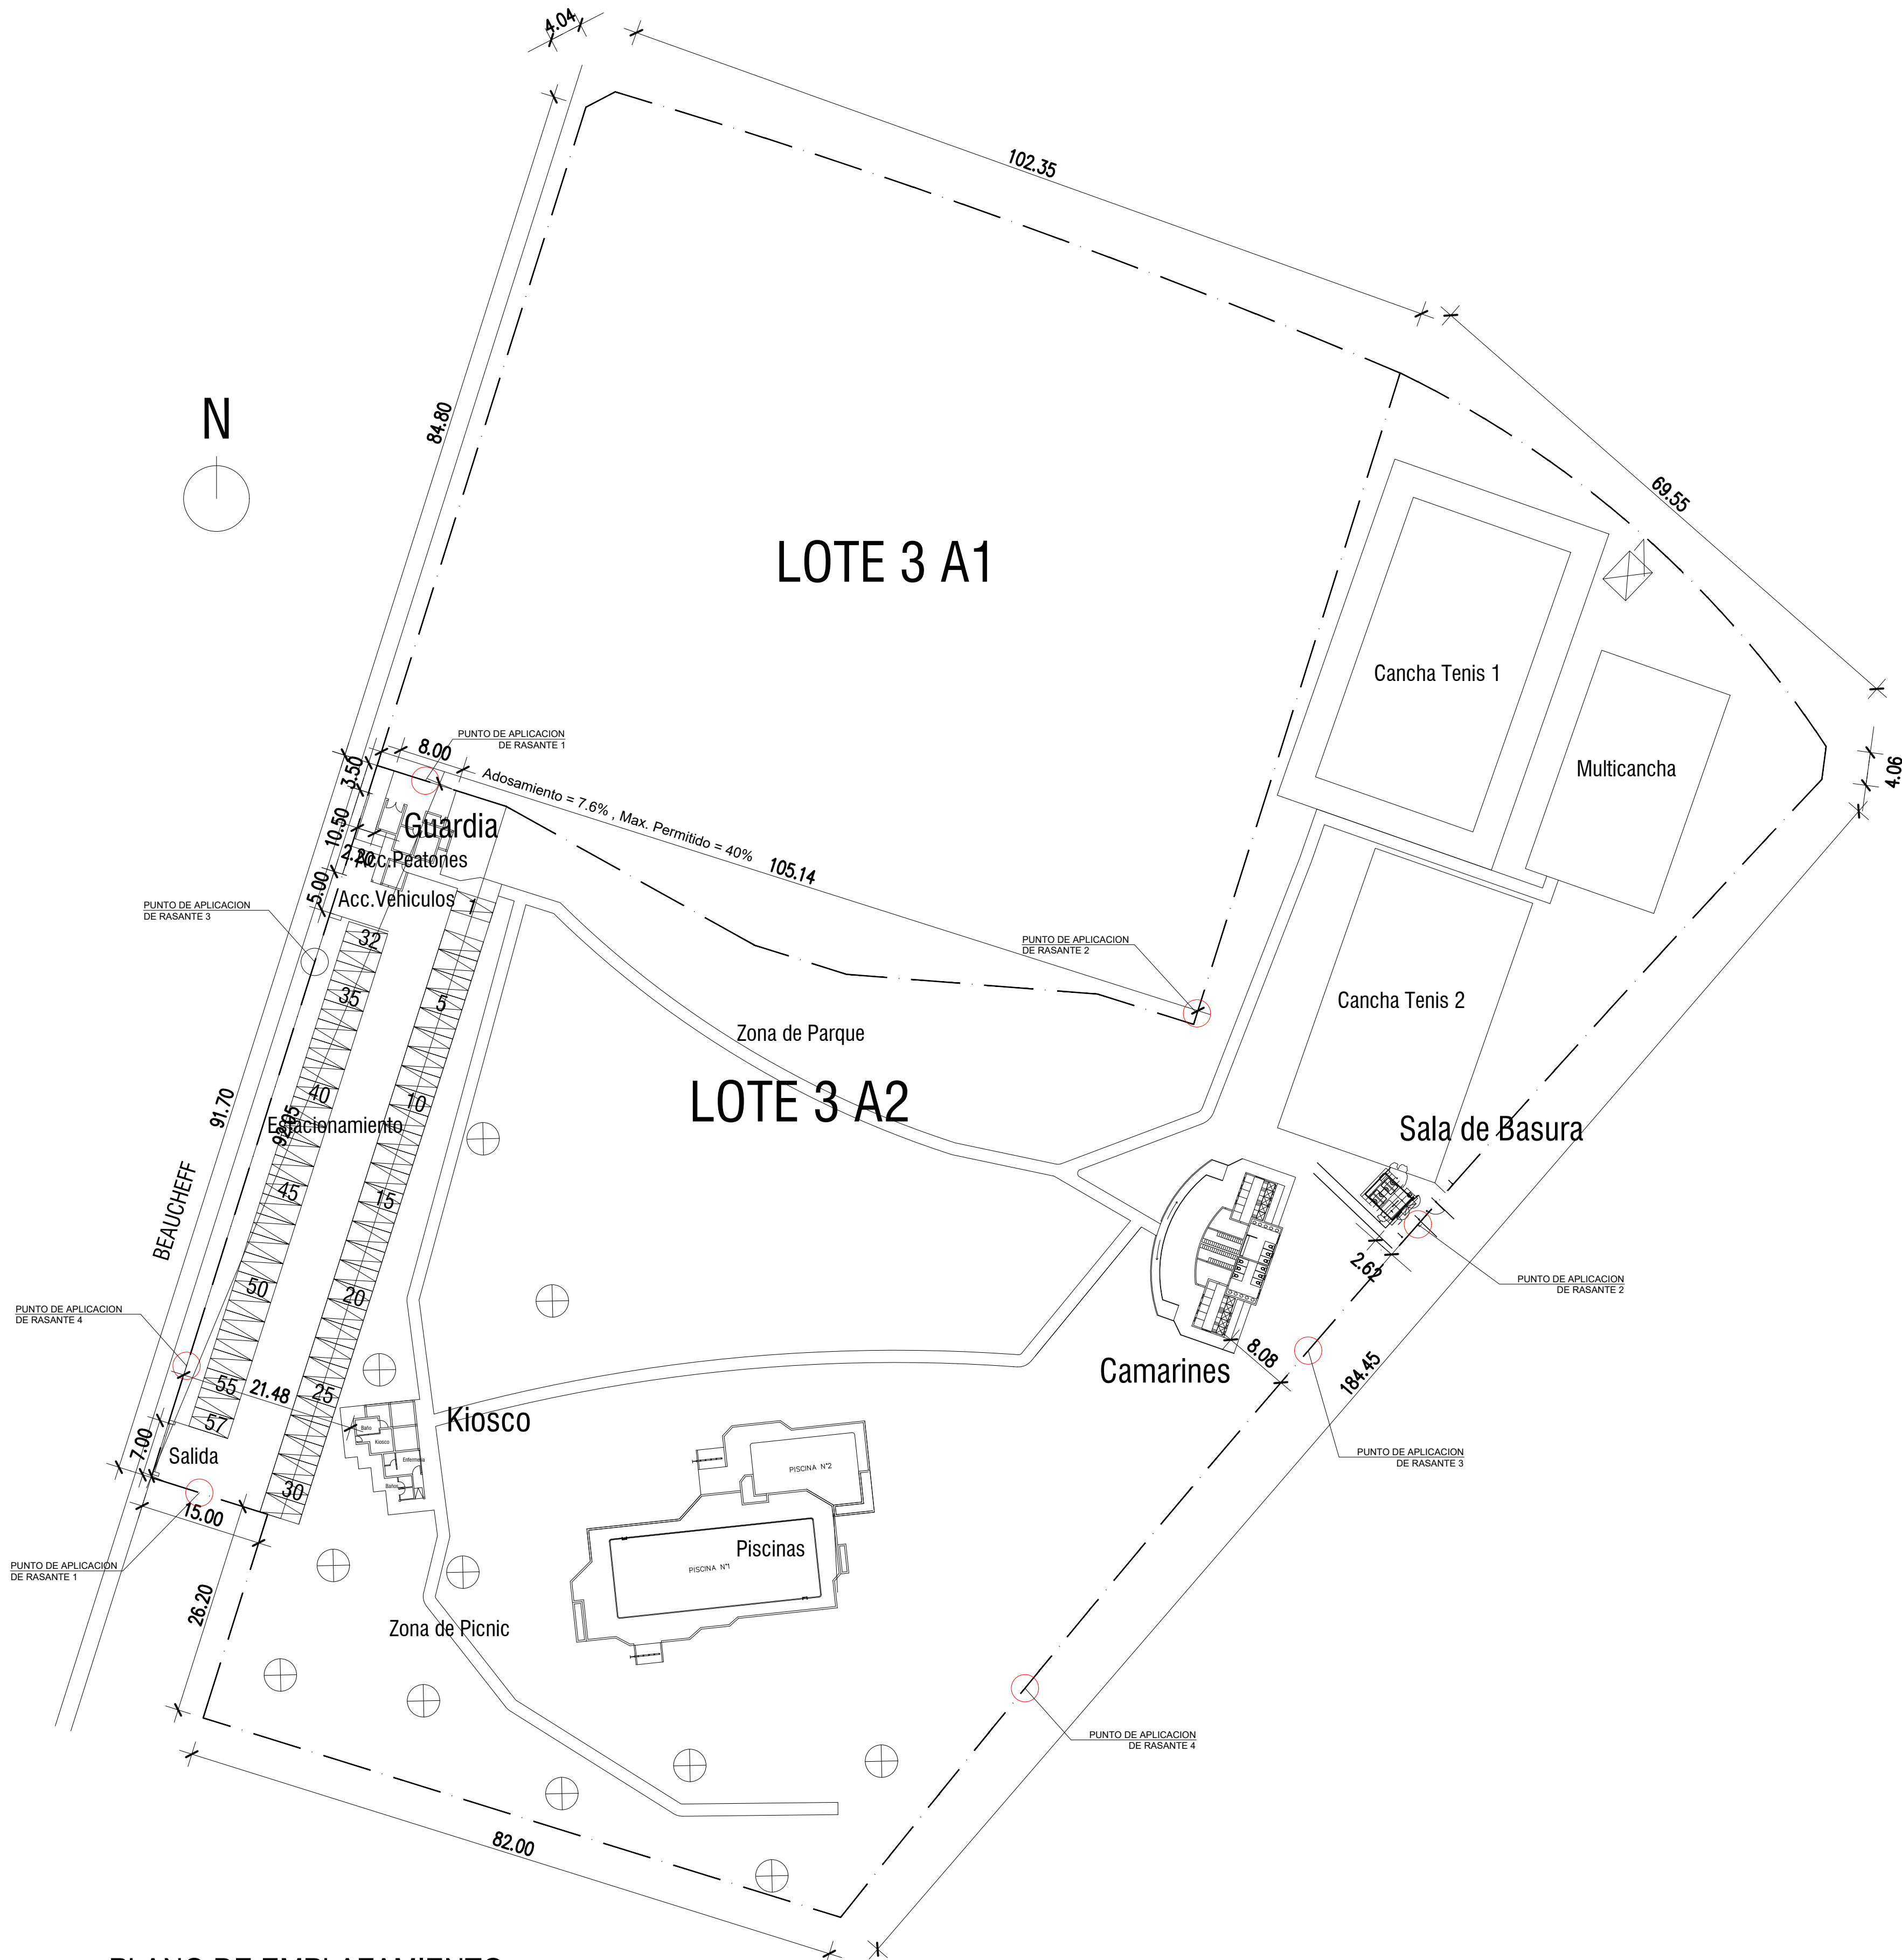


PLANO DE EMPLAZAMIENTO
Esc. 1:2000

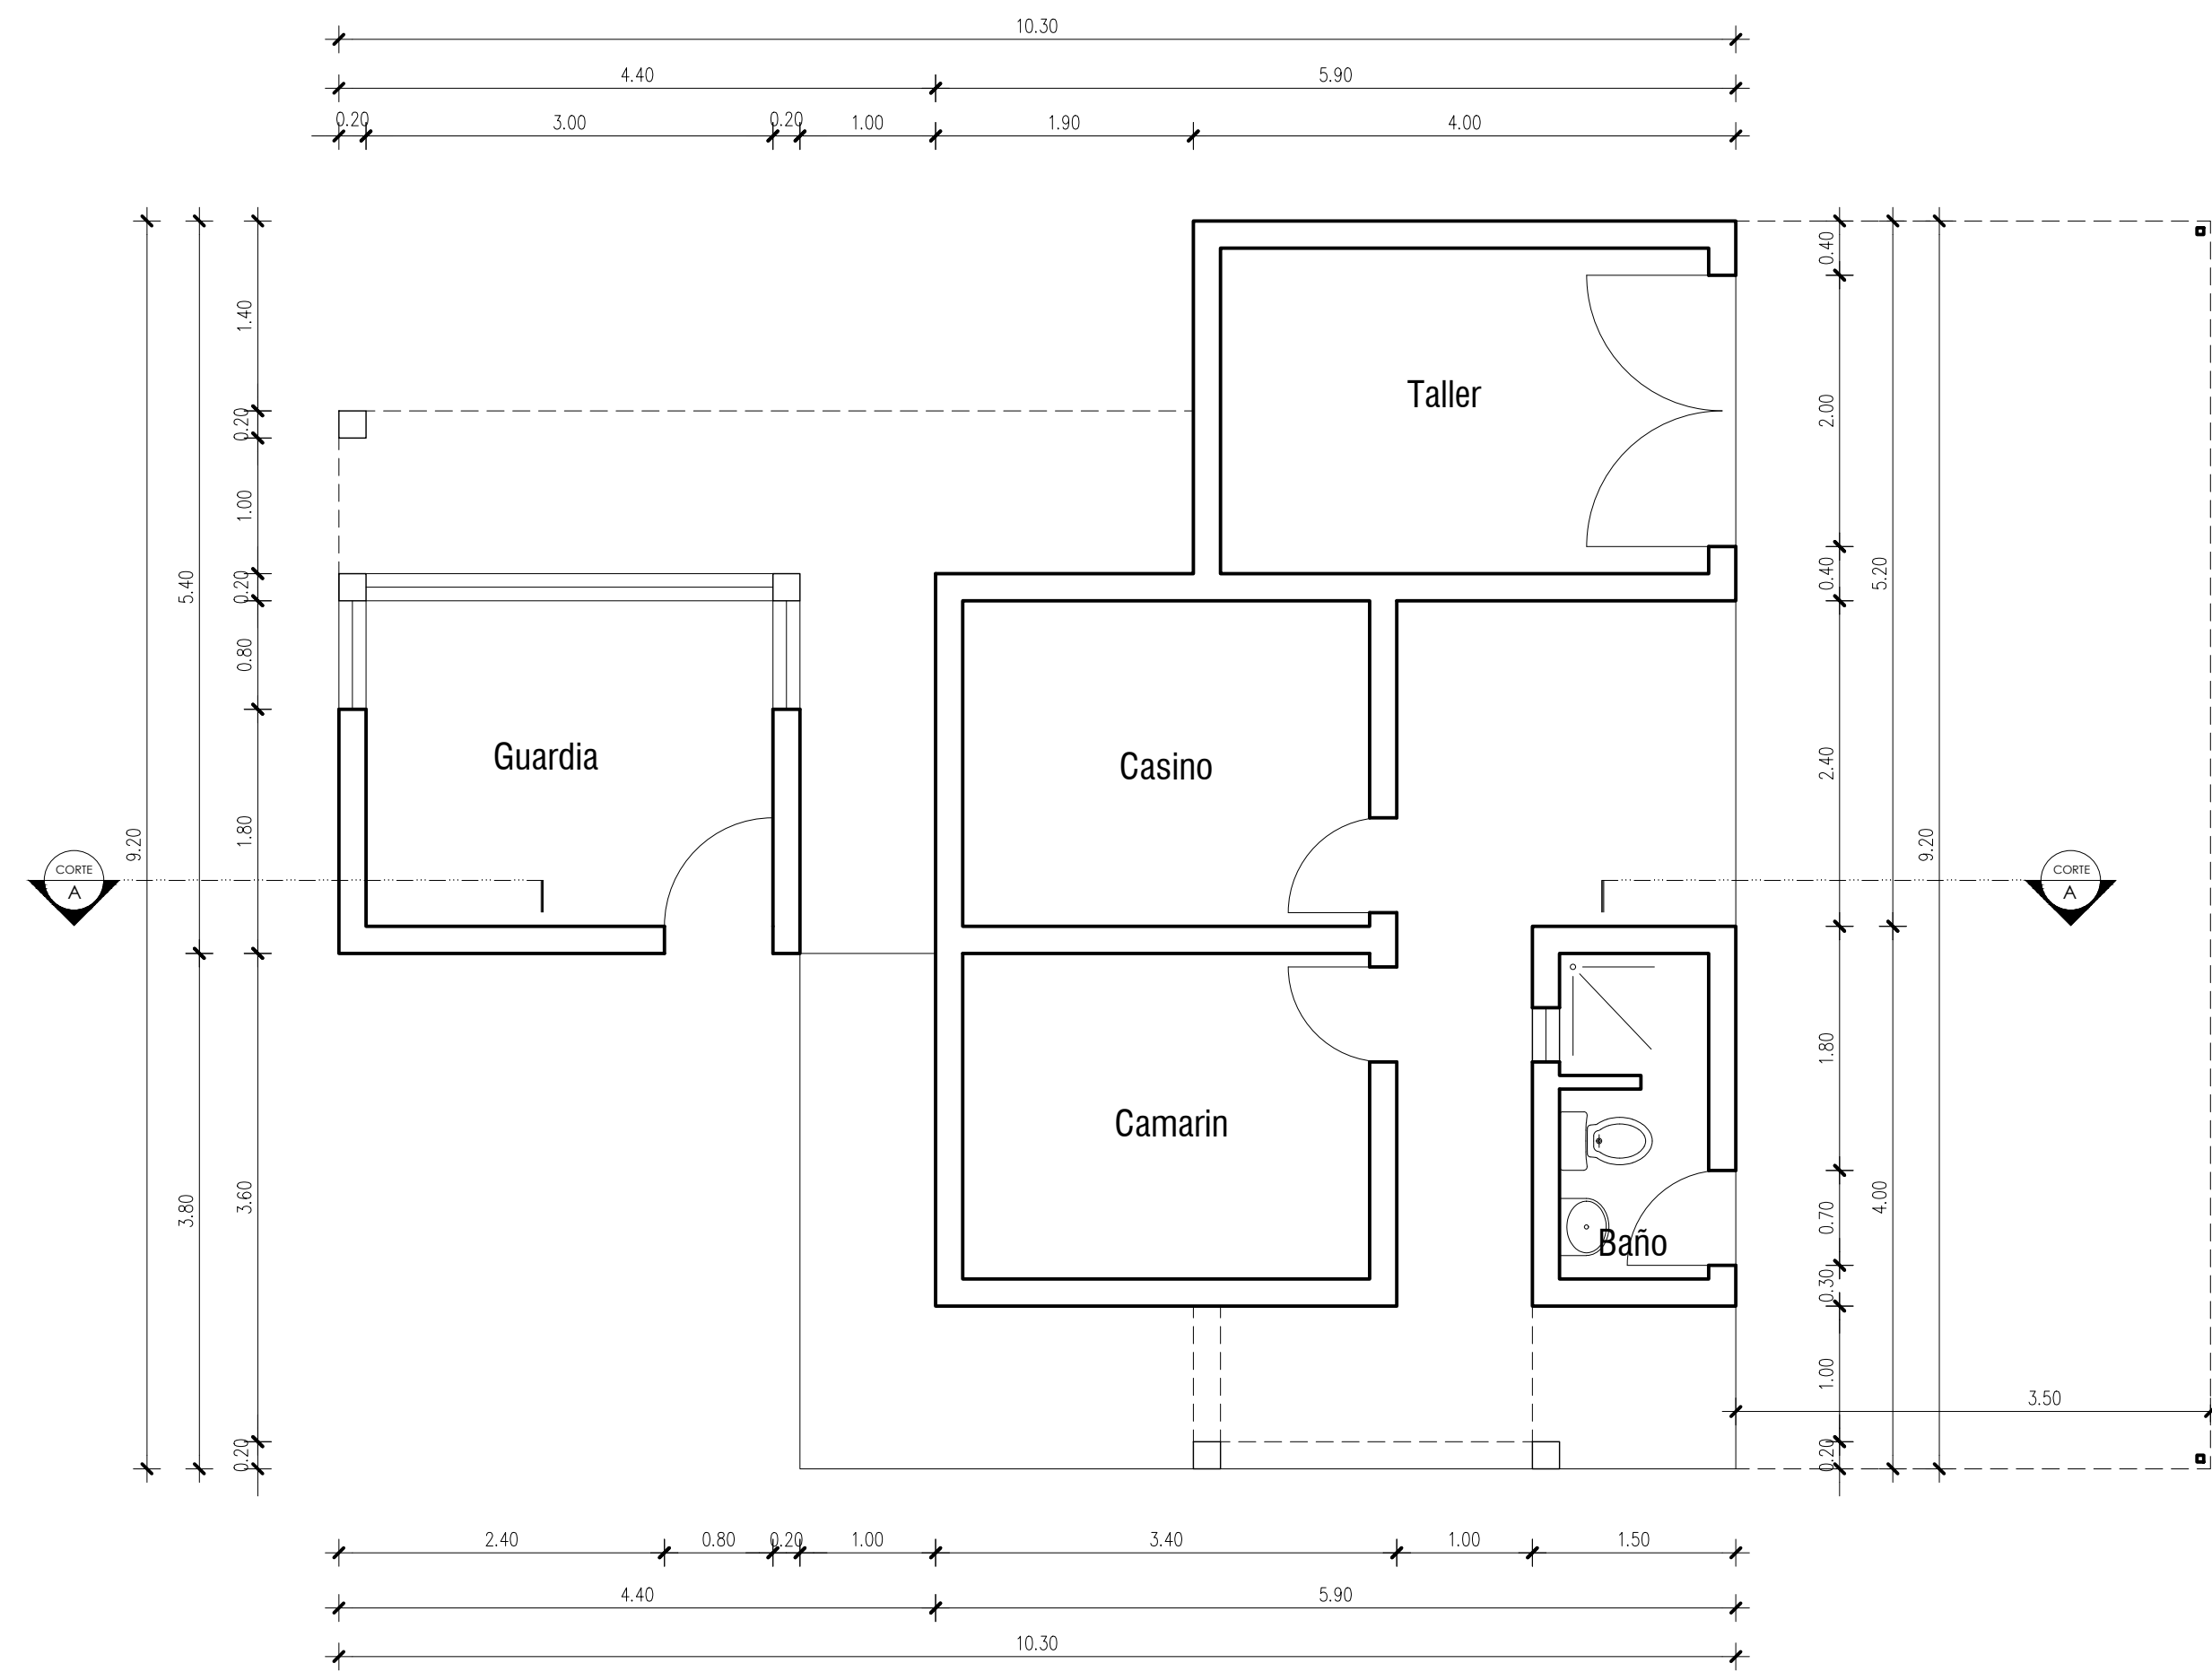


Planta de Acceso
Esc. 1:50

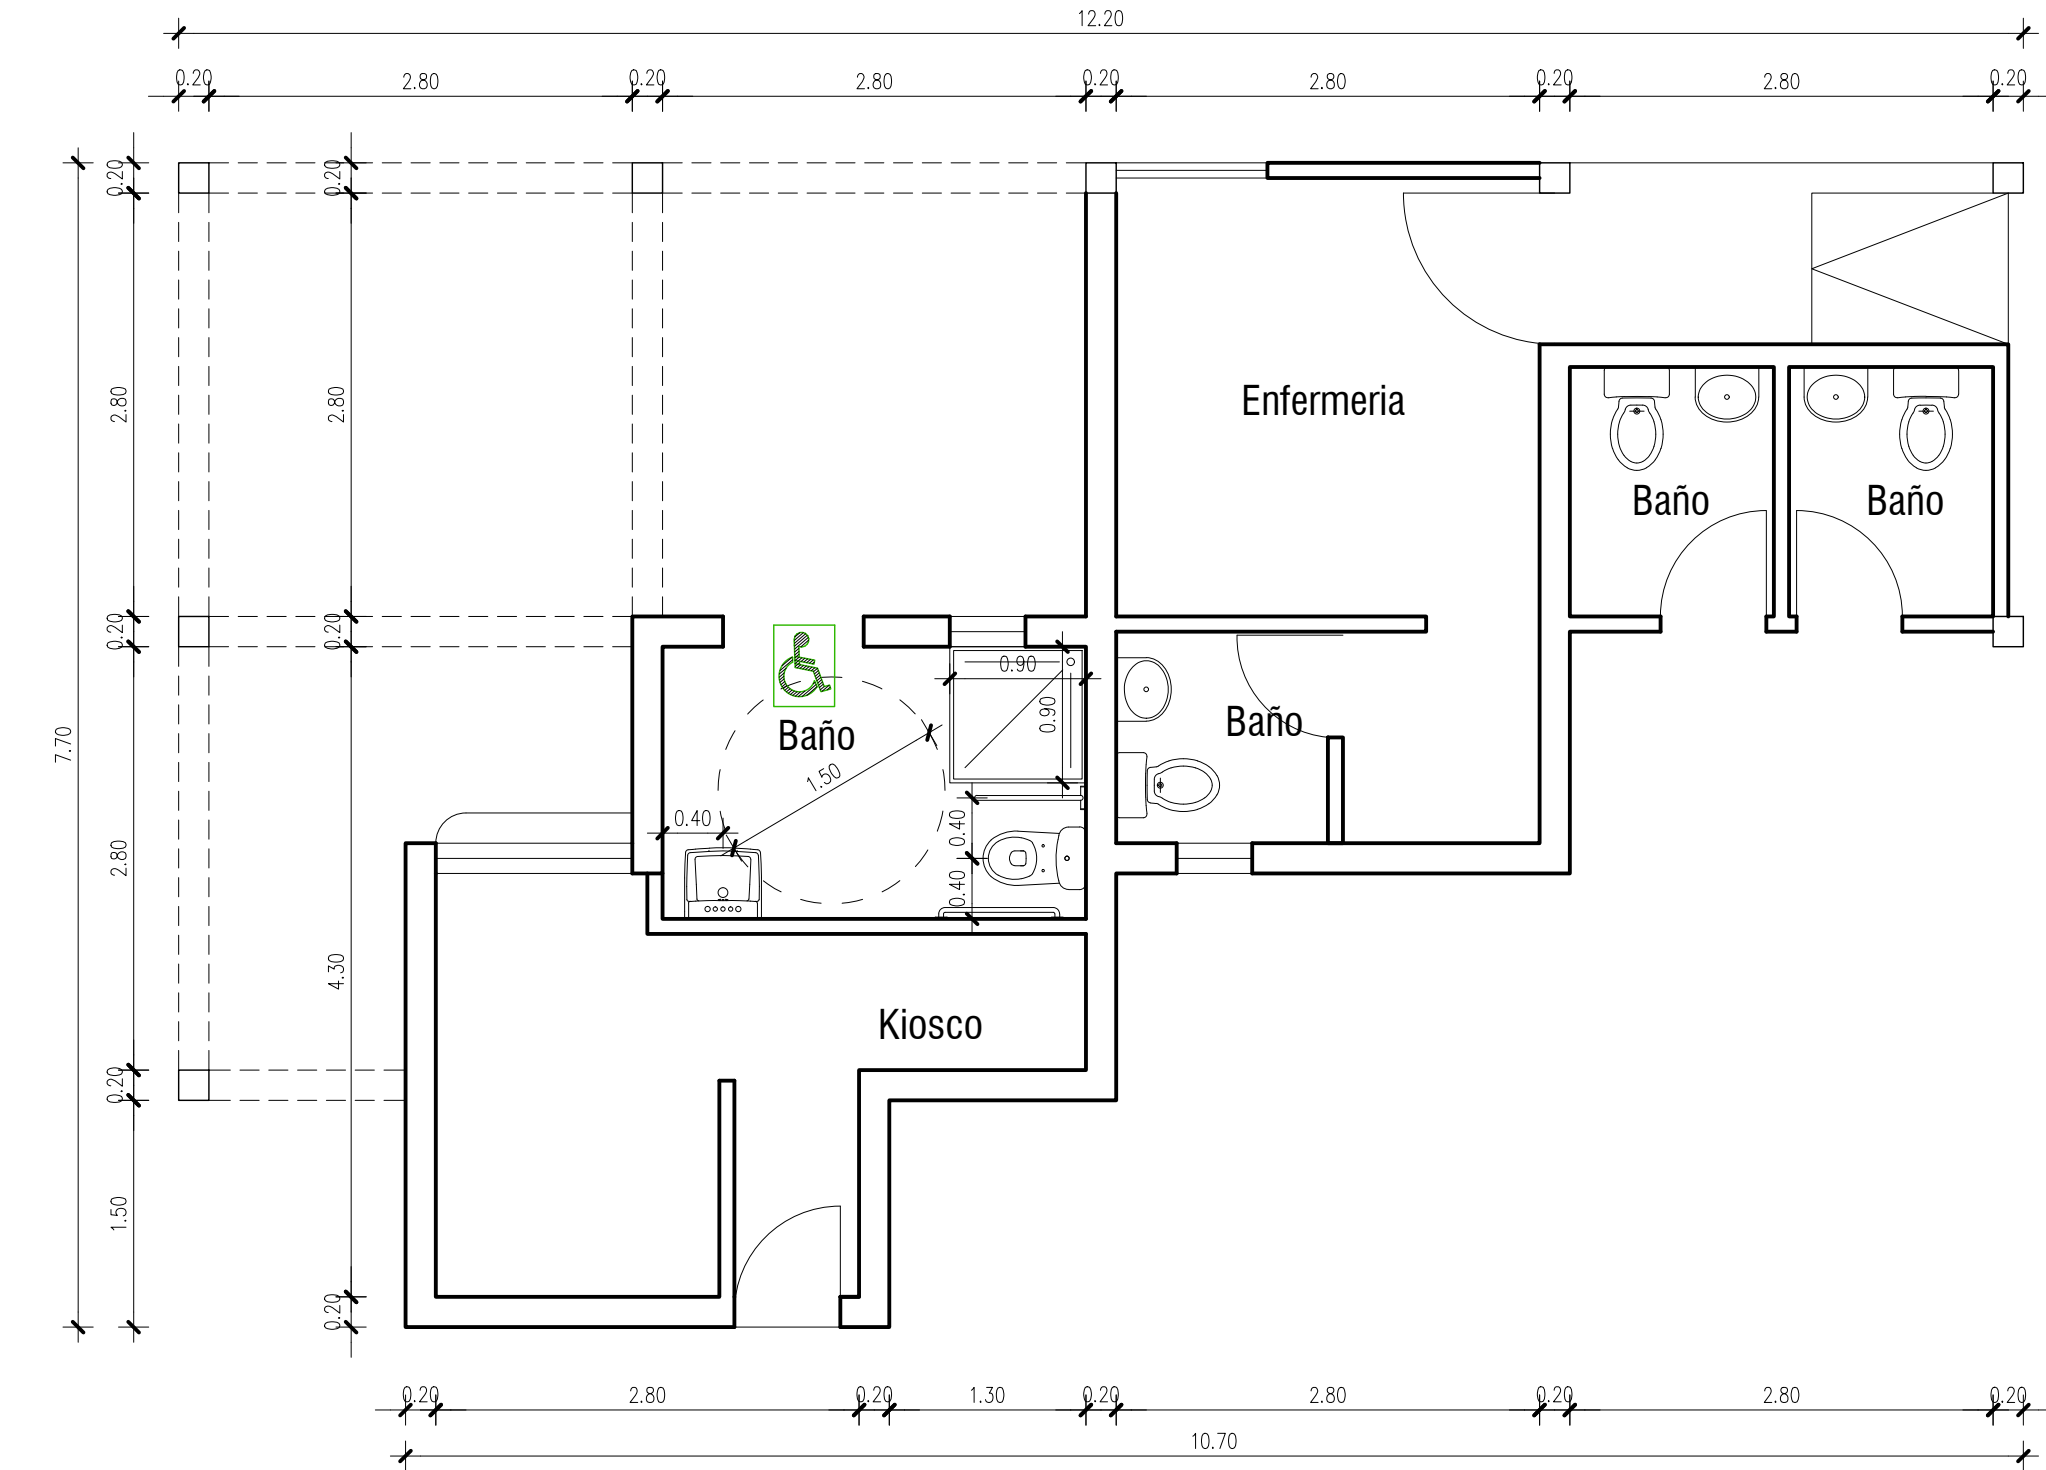

Planta de Kiosco / Enfermeria
Esc. 1:50

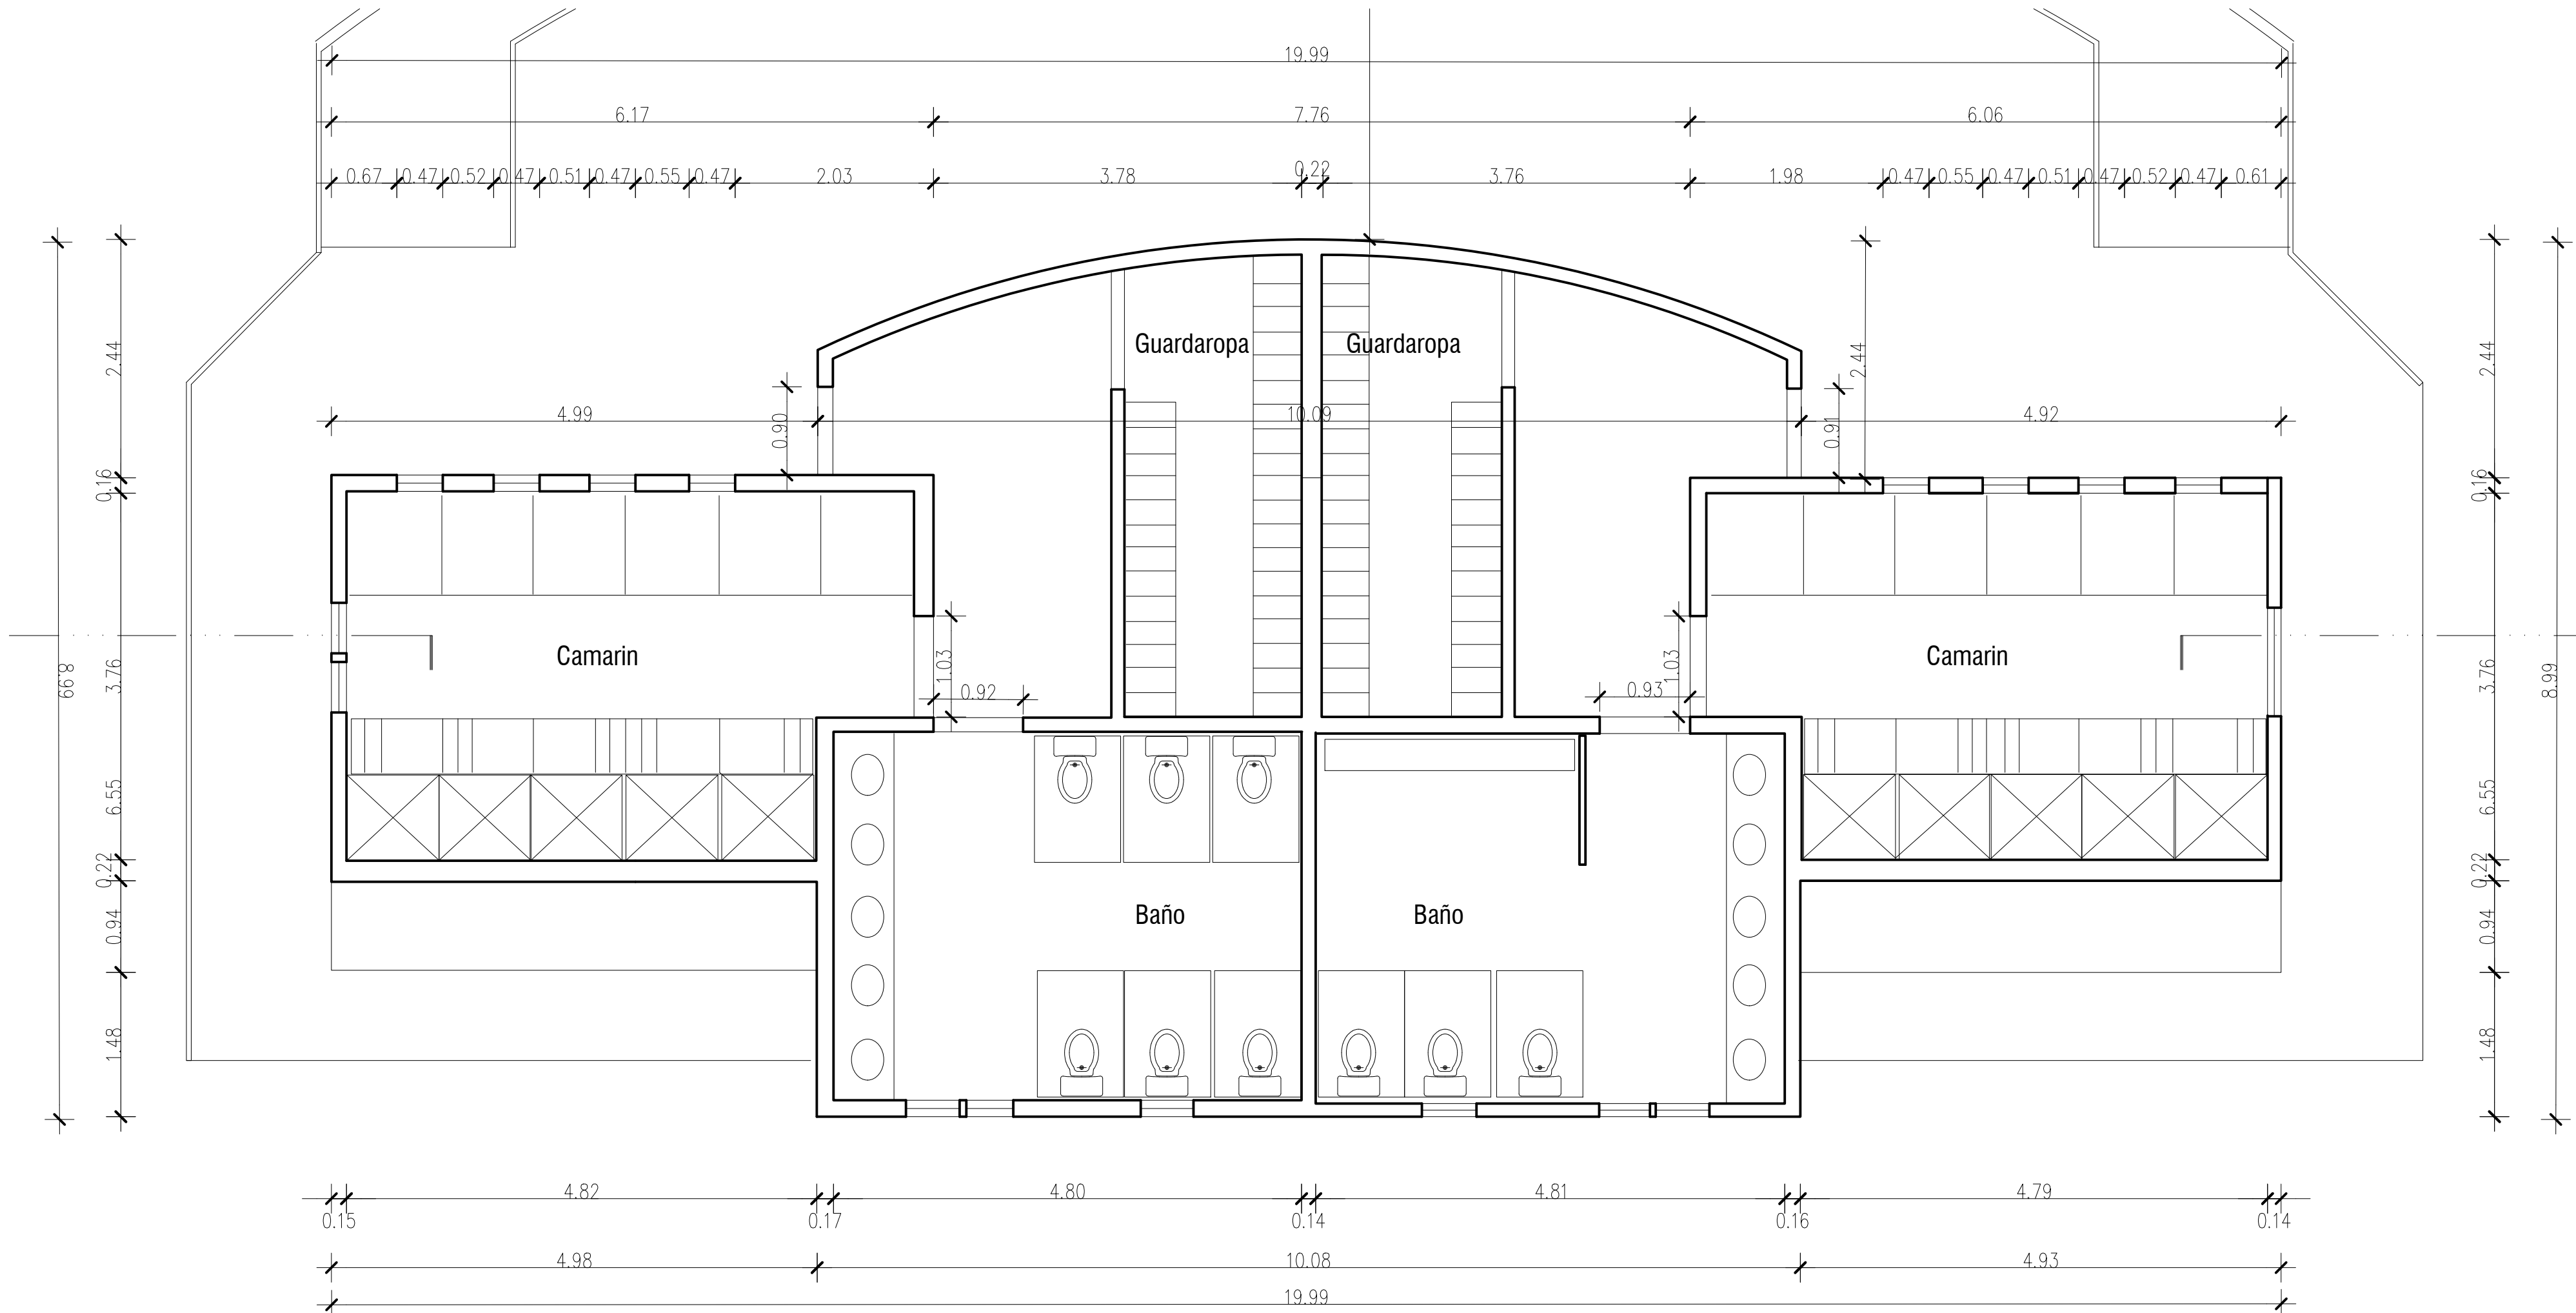

Planta de Camarines
Esc. 1:50

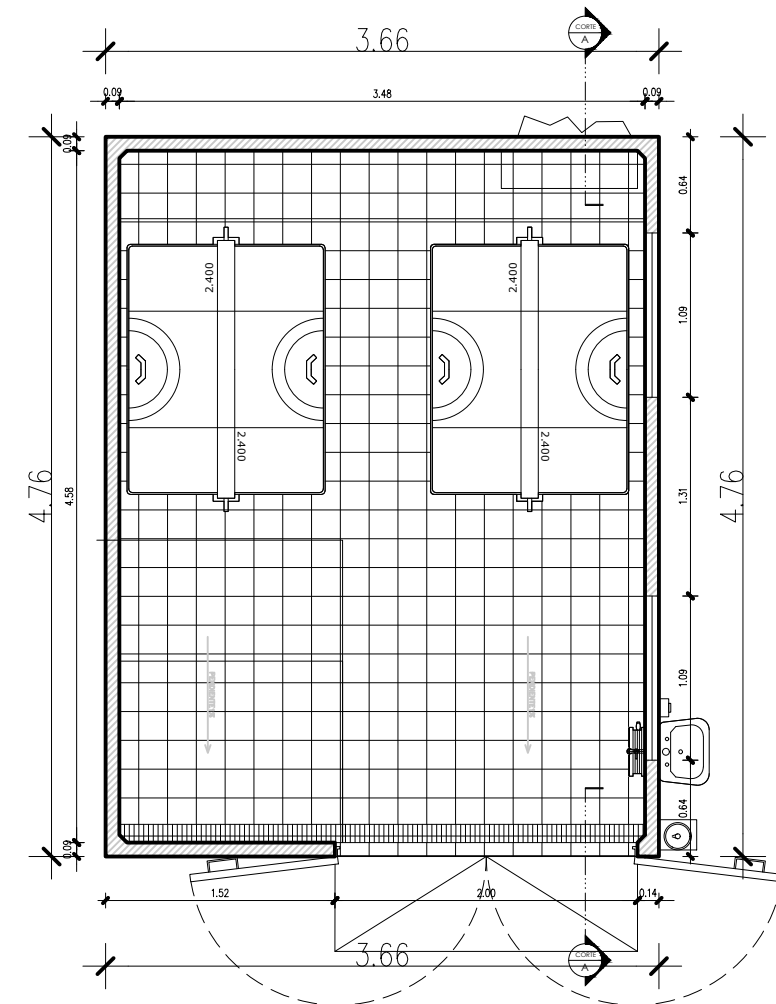

Planta de S. de Basura
Esc. 1:50

CONTENIDO LAMINA:
Plantas

FIRMA PROPIETARIO / REPRESENTANTE LEGAL

C.C.A.F. de Los Andes

FIRMA ARQUITECTO

Tomás Fajardo Cabello
Arquitecto PUC - I.C.A. 8373
tomASFajardo@cfajardo.cl

FIRMA REVISOR MUNICIPAL

D.O.M. Municipalidad

CODIGO:
CRB - 2022 - RCRB

VERSIONES			
	NOMBRE	FECHA	EDICION
DIB	JMA	18-08-22	1.0
EDI			
EDI			
EDI			
EDI			
EDI			
EDI			
EDI			
EDI			


OBRA:
**CENTRO
RECREACIONAL
BEAUCHEFF**

CAJA DE COMPENSACION LOS ANDES


DIRECCION : Beaucheff n°3500
COMUNA : Pedro Aguirre Cerda
ROL : 2971 - 1

	NOMBRE	FECHA	Lamina: 03 de 08
DIB	JMA	18-08-22	
REV	TFC	08-22	
ESC	INDICADAS		


A03

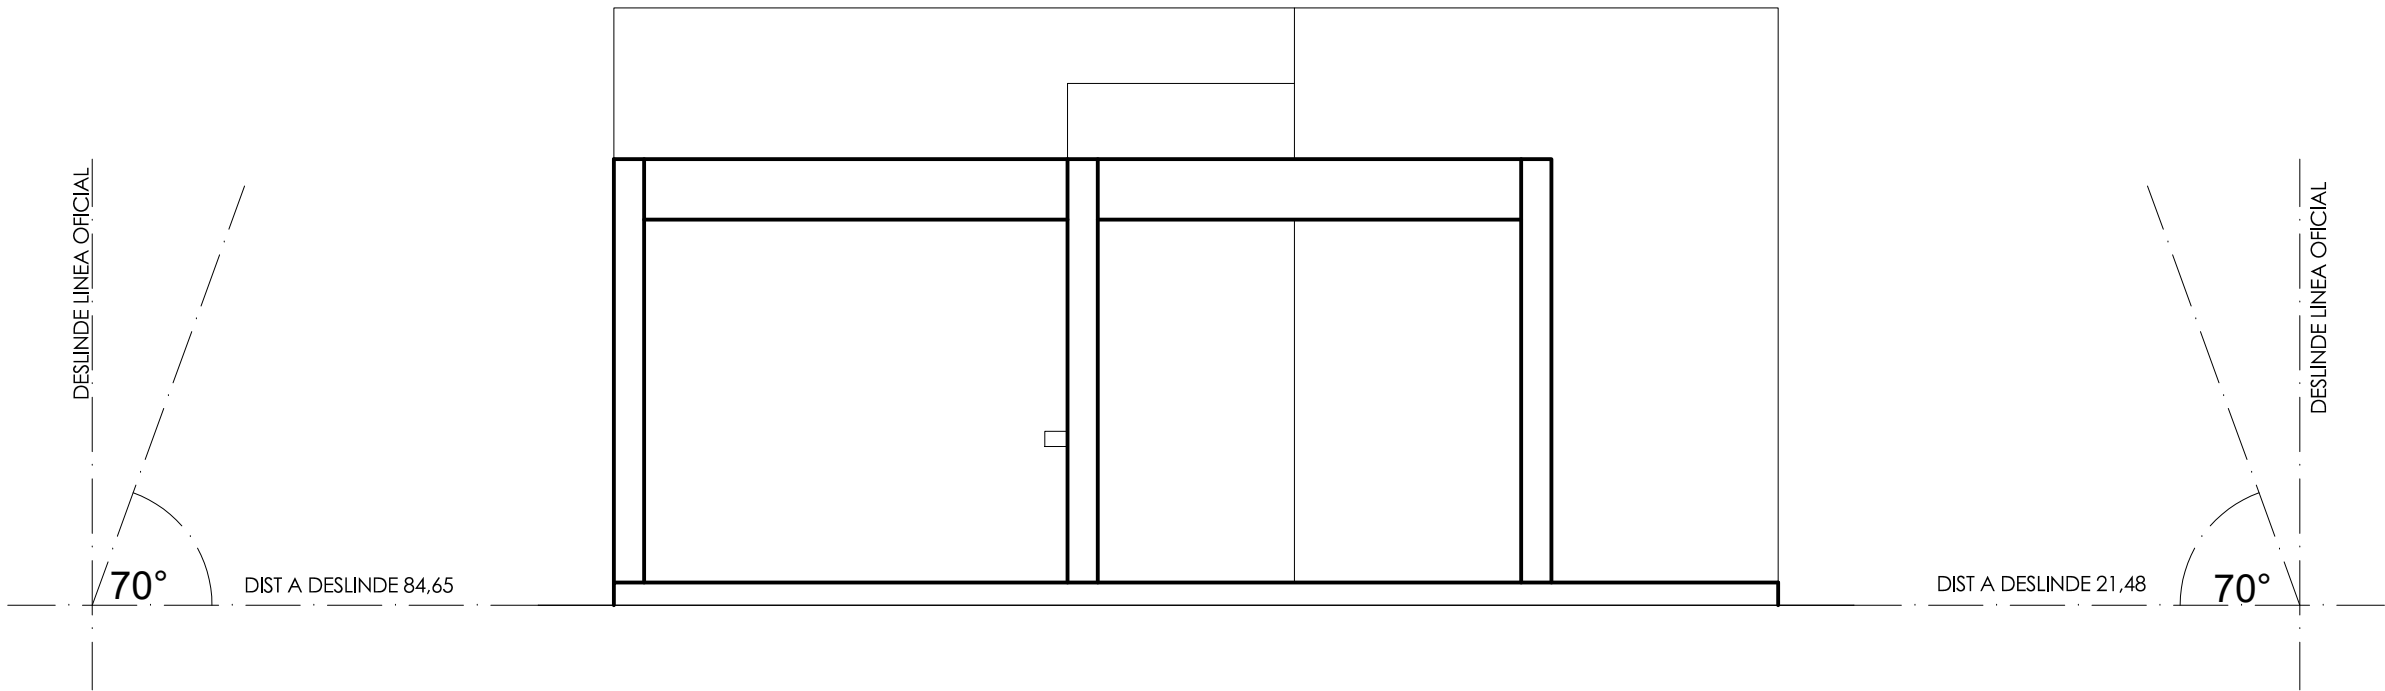


Acceso, Elevación Norte
Esc. 1:50

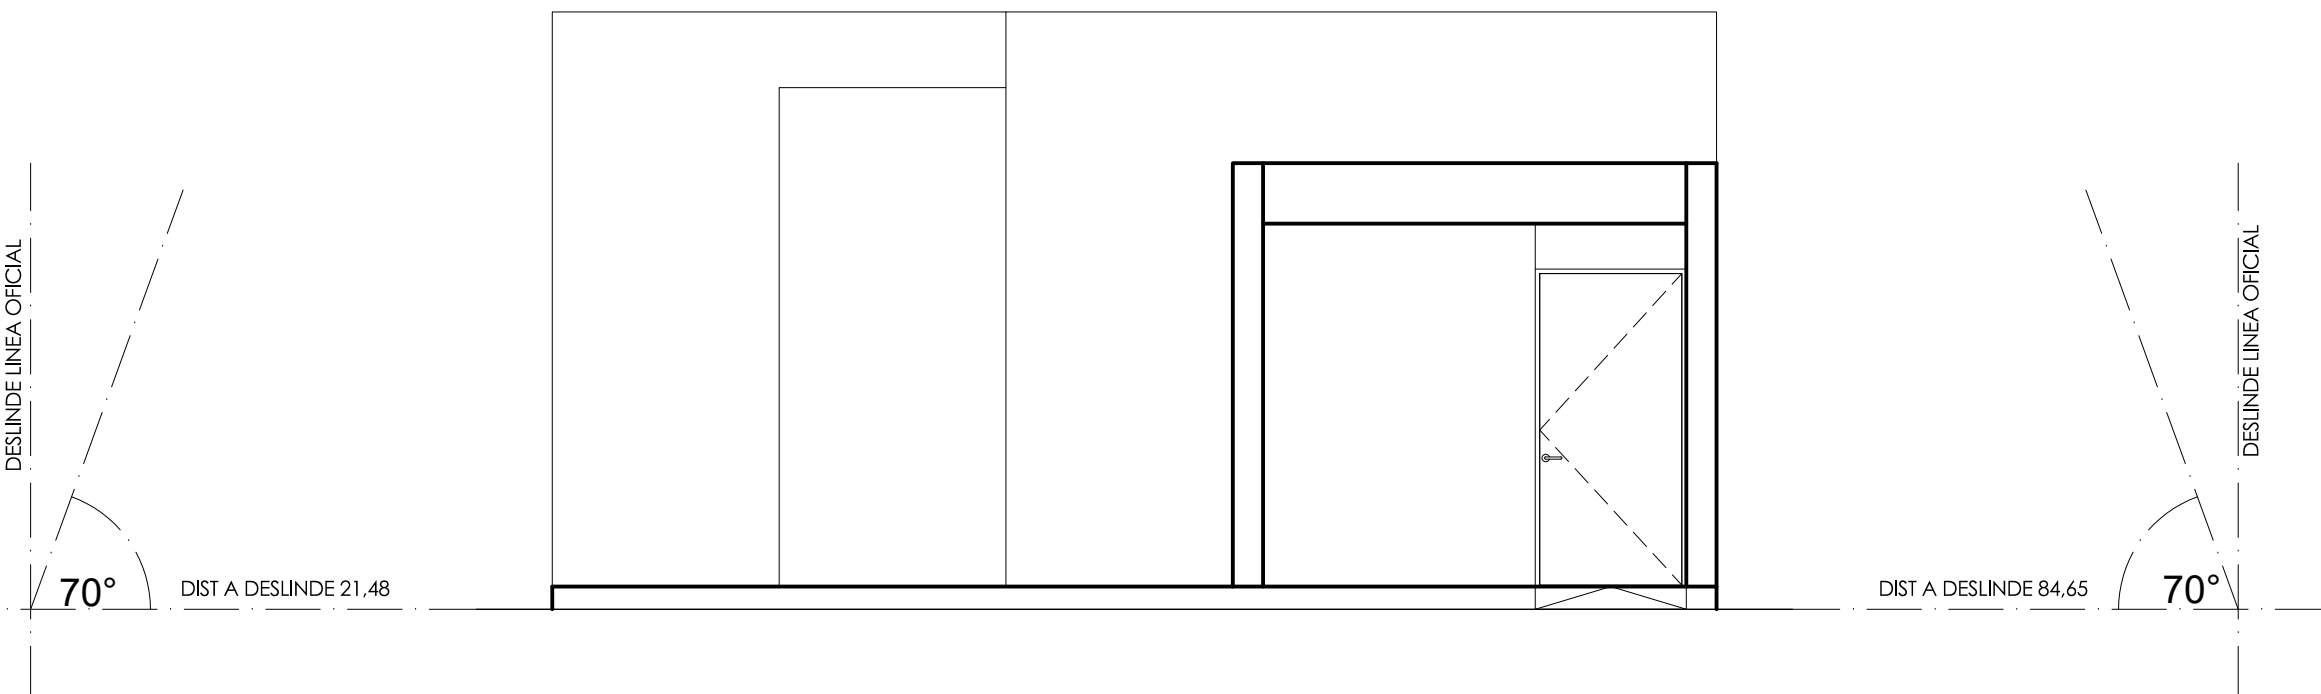


Acceso, Elevación Sur
Esc. 1:50

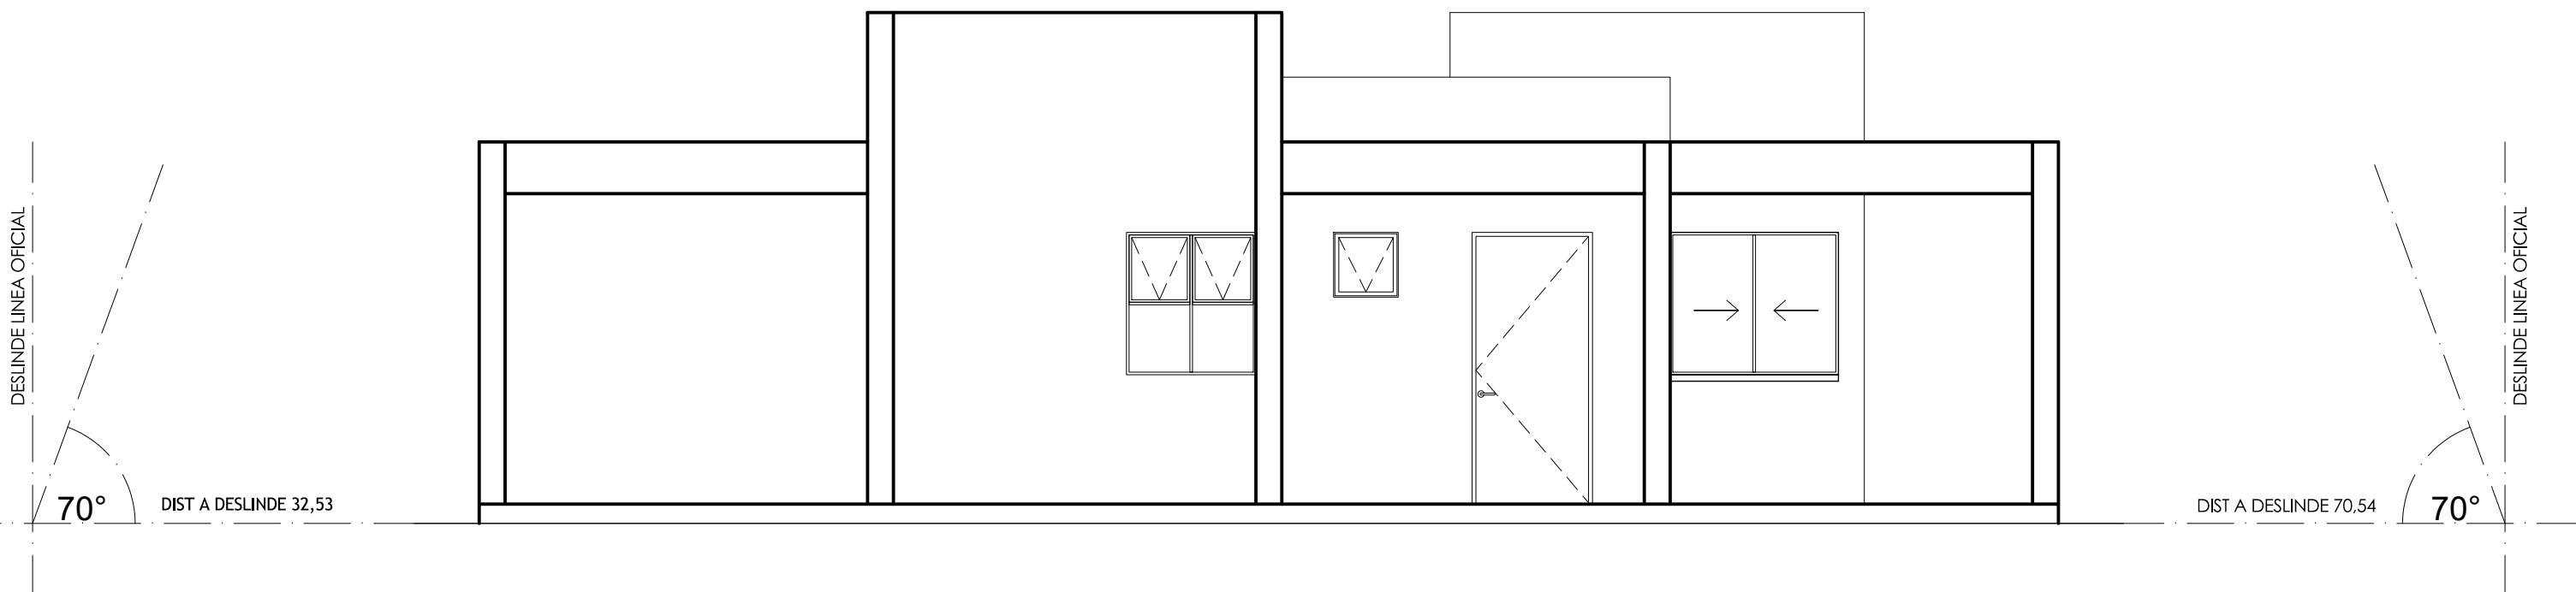


Acceso, Elevación Oriente
Esc. 1:50

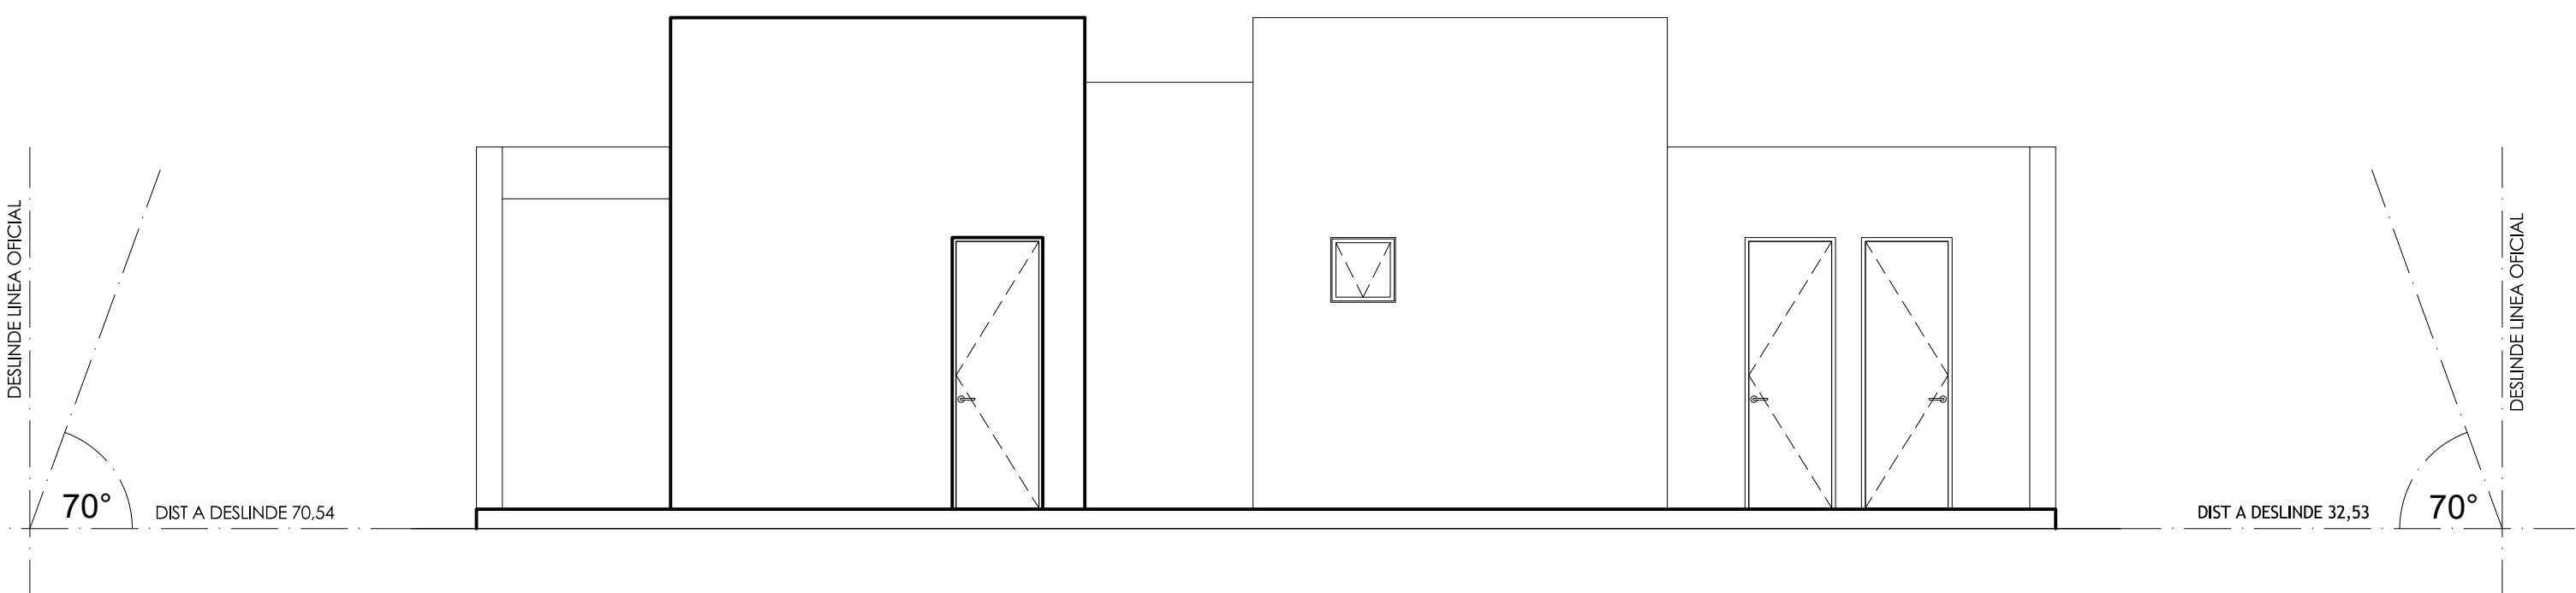


Acceso, Elevación Poniente
Esc. 1:50

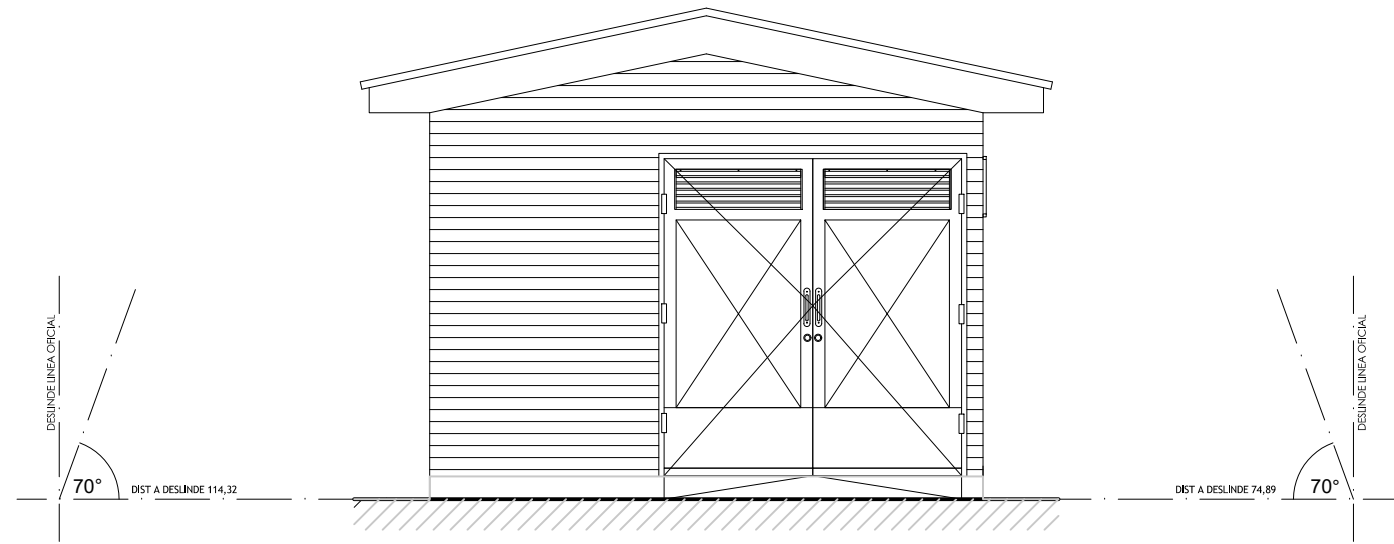

S. Basura, Elevación Oriente
Esc. 1:50

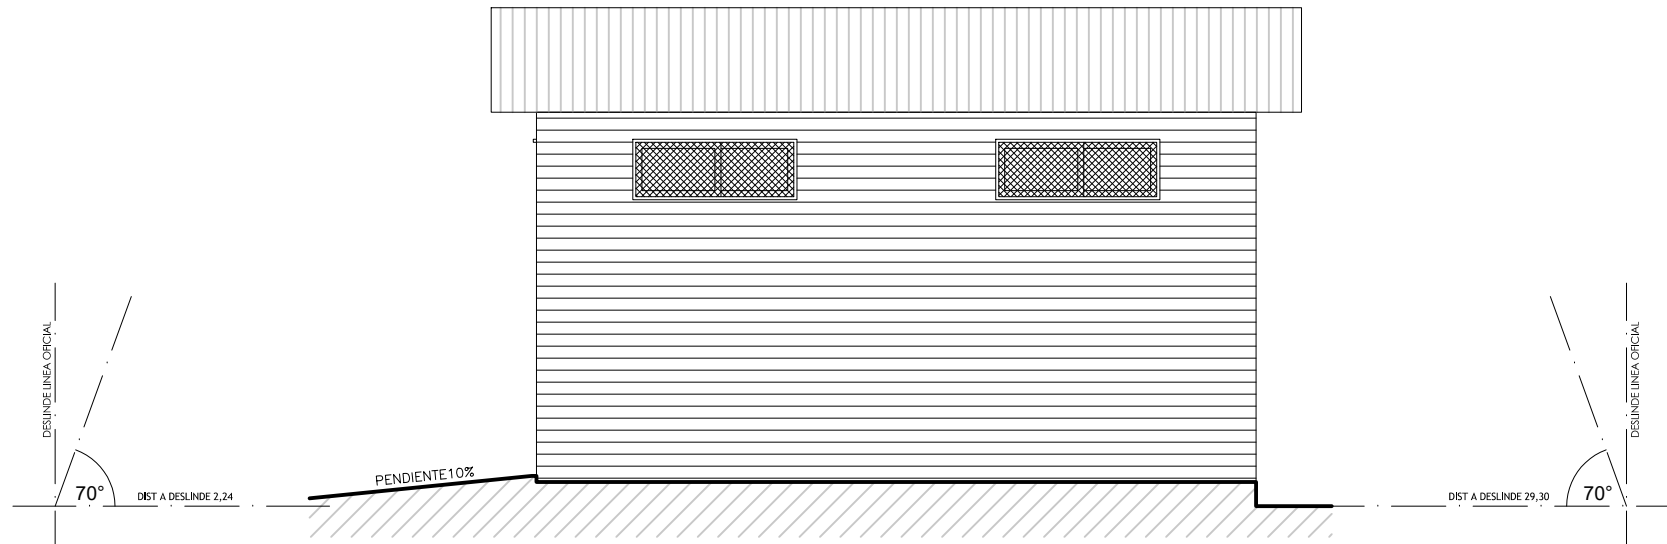

S. Basura, Elevación Norte
Esc. 1:50

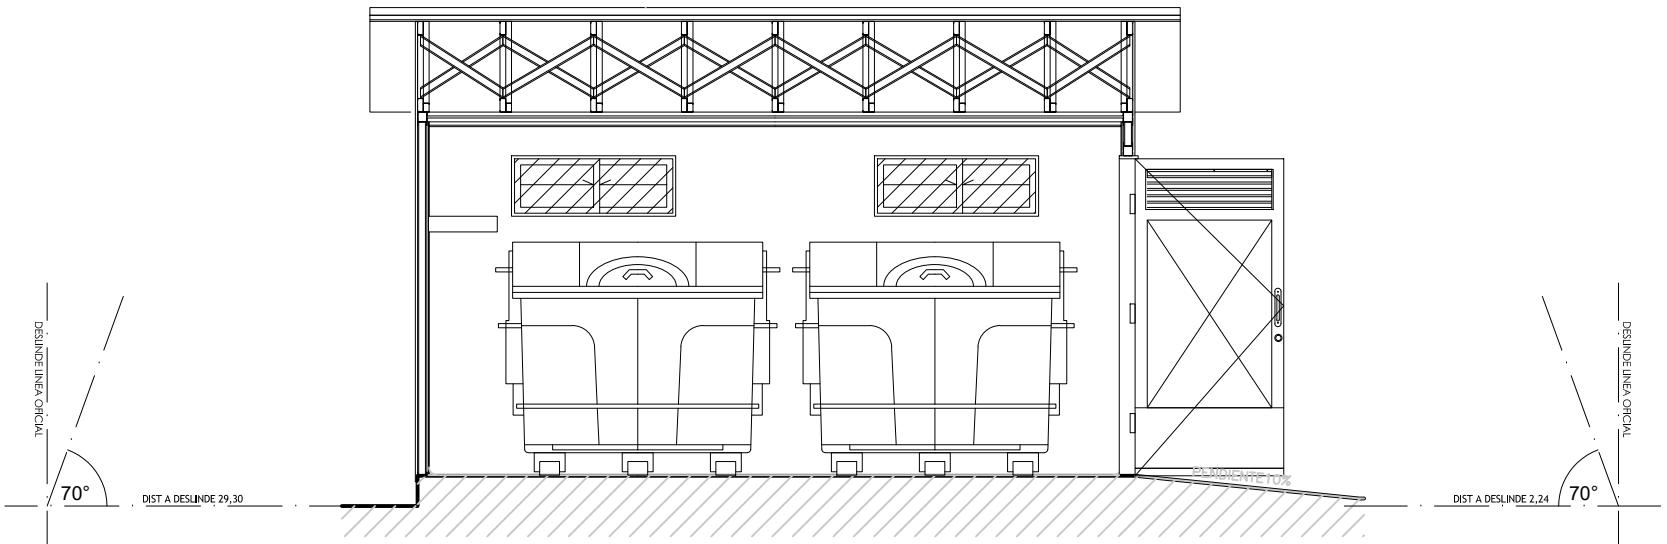

S. Basura, Corte B-B
Esc. 1:50

CONTENIDO LAMINA:
Elevaciones Acceso y Sala de Basura

FIRMA PROPIETARIO / REPRESENTANTE LEGAL

C.C.A.F. de Los Andes

FIRMA ARQUITECTO

Tomás Fajardo Cabello
Arquitecto PUC - I.C.A. 8373
tomASFajardo@cfajardo.cl

FIRMA REVISOR MUNICIPAL

D.O.M. Municipalidad


CODIGO:
CRB - 2022 - RCRB

VERSIONES			
	NOMBRE	FECHA	EDICION
DIB	JMA	18-08-22	1.0
EDI			
EDI			
EDI			
EDI			
EDI			
EDI			
EDI			
EDI			


OBRA:
**CENTRO
RECREACIONAL
BEAUCHEFF**
CAJA DE COMPENSACION LOS ANDES

DIRECCION : Beaucheff n°3500
COMUNA : Pedro Aguirre Cerda
ROL : 2971 - 1


	NOMBRE	FECHA	Lamina: 04 de 08
DIB	JMA	18-08-22	A04
REV	TFC	08-22	
ESC	INDICADAS		

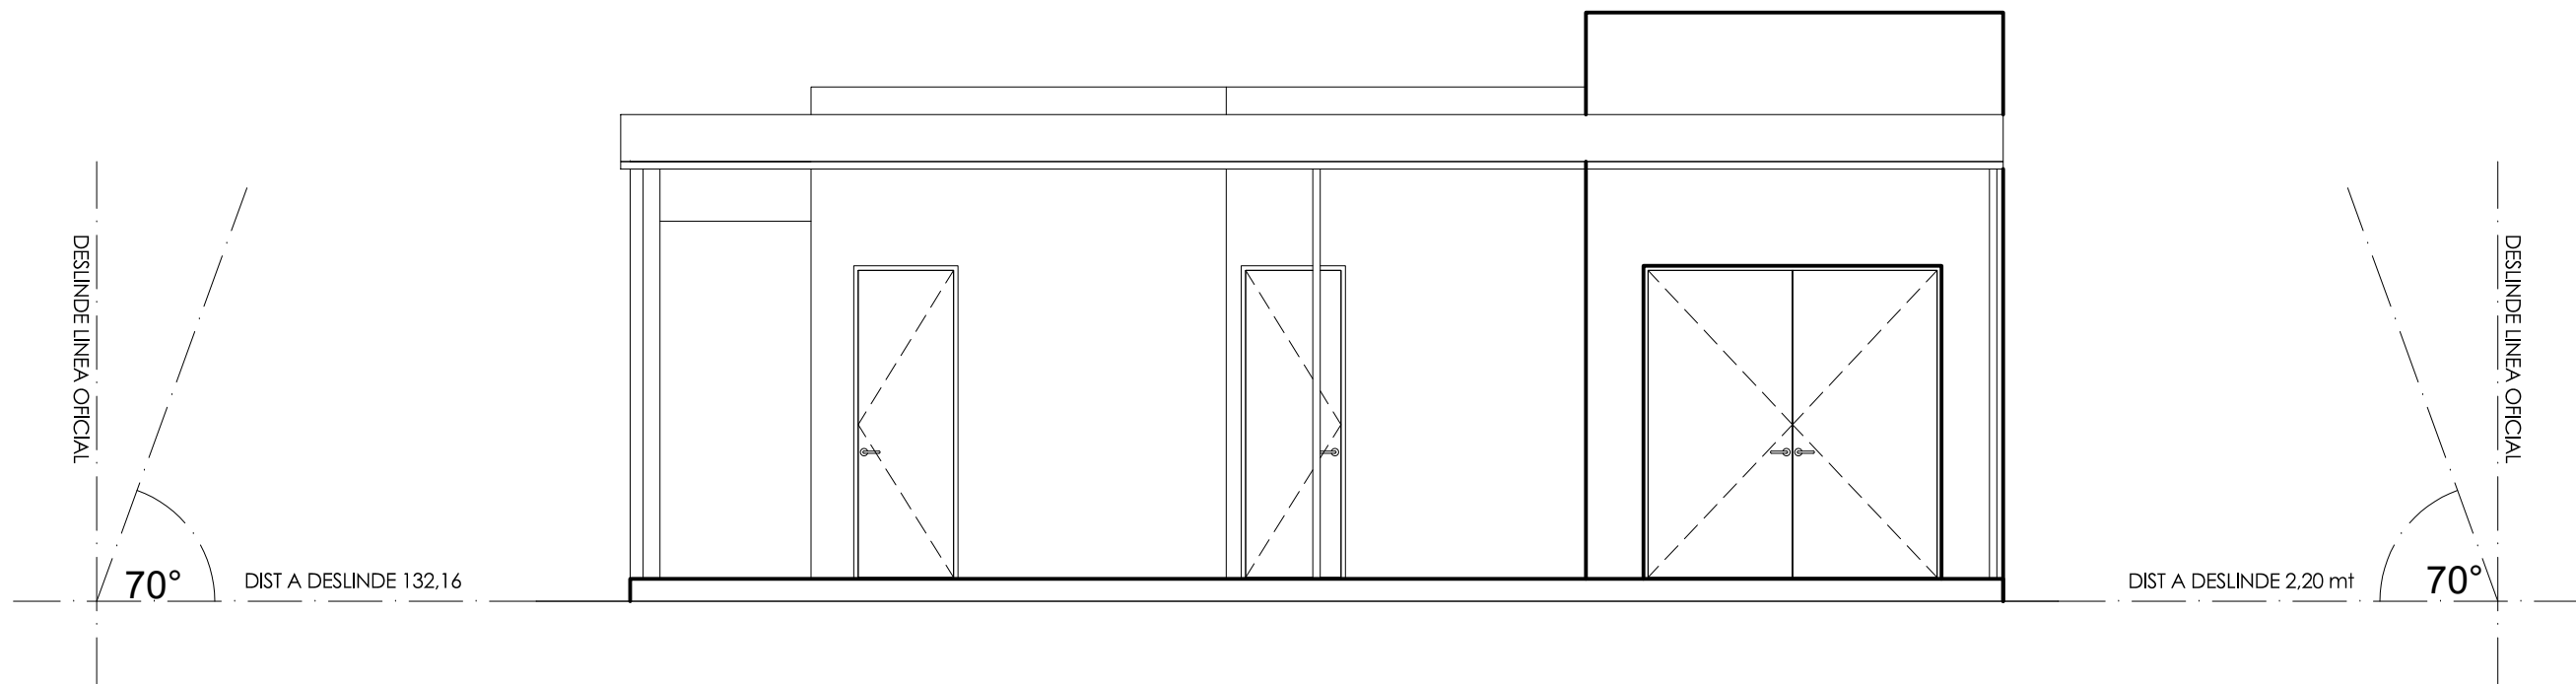


Kiosco / Enfermería, Elevación Norte
Esc. 1:50

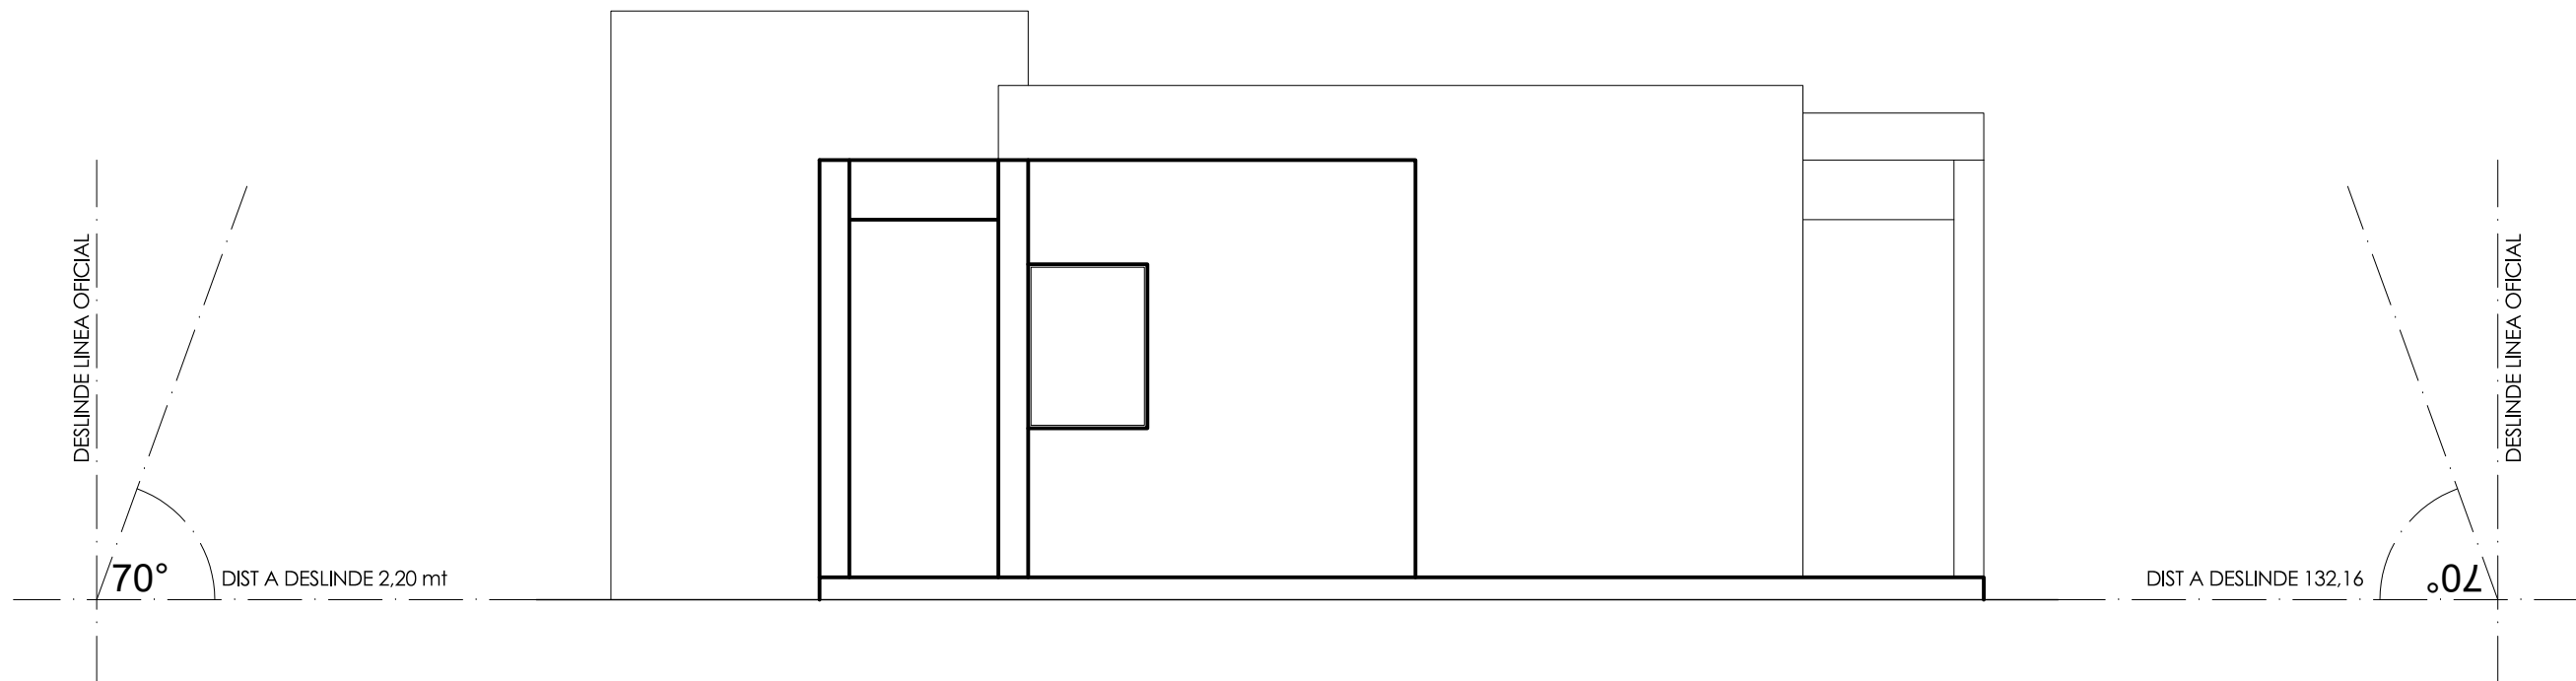

Kiosco / Enfermería, Elevación Sur
Esc. 1:50

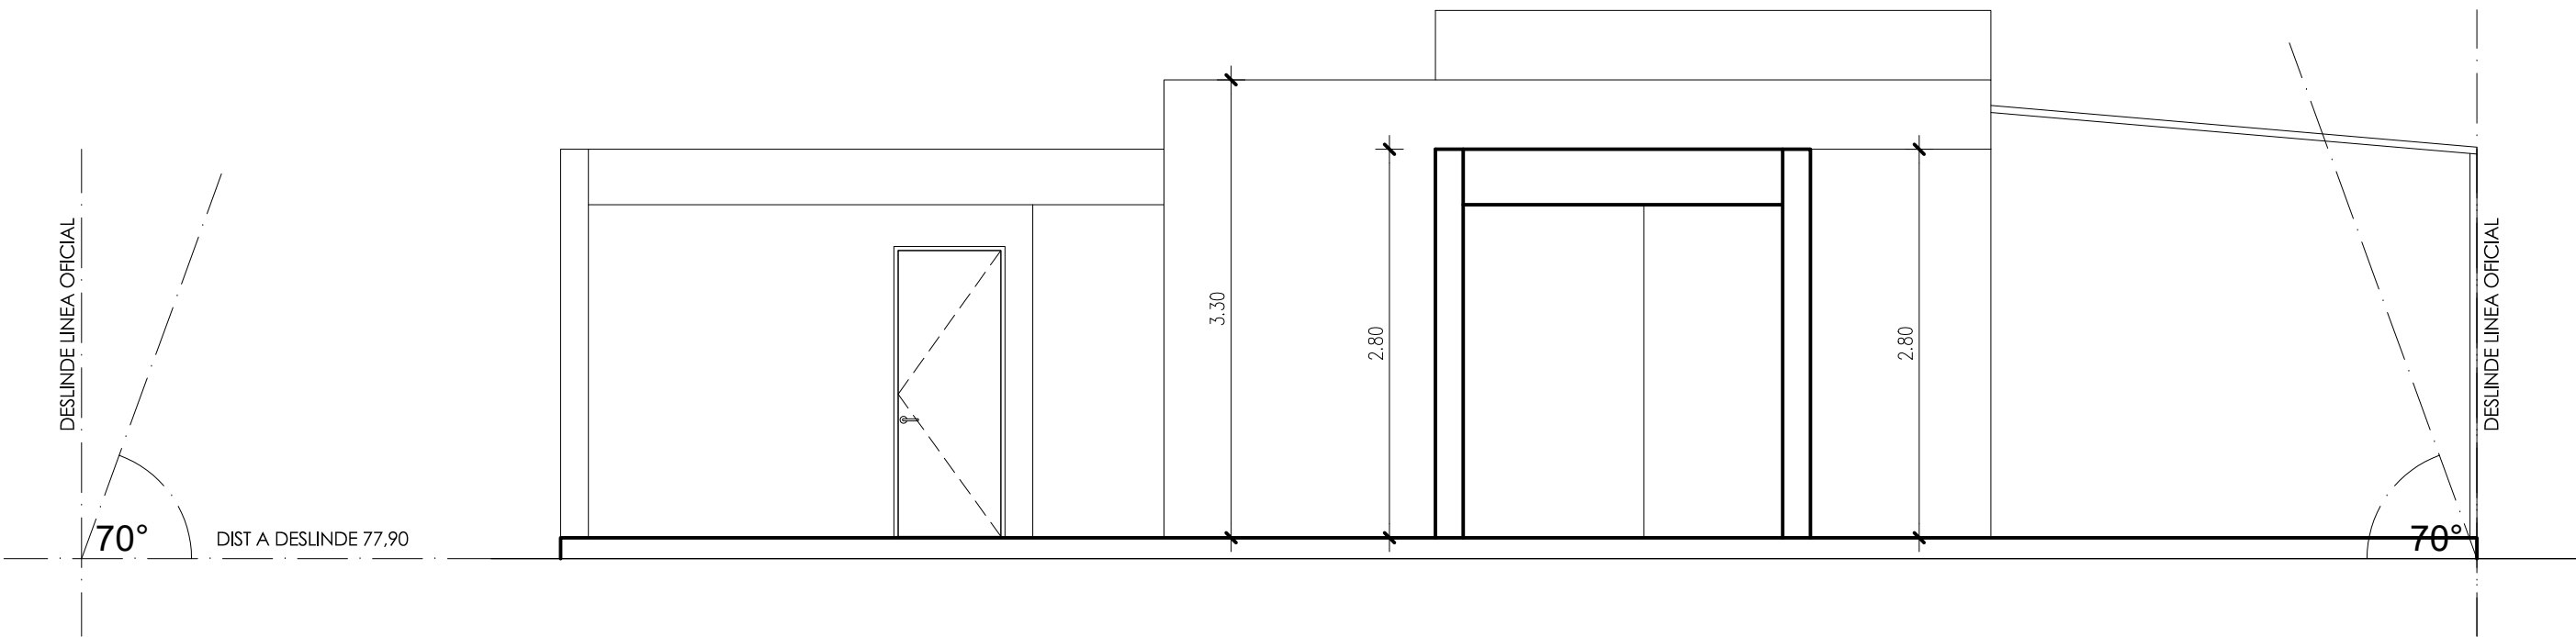

Kiosco / Enfermería, Elevación Oriente
Esc. 1:50

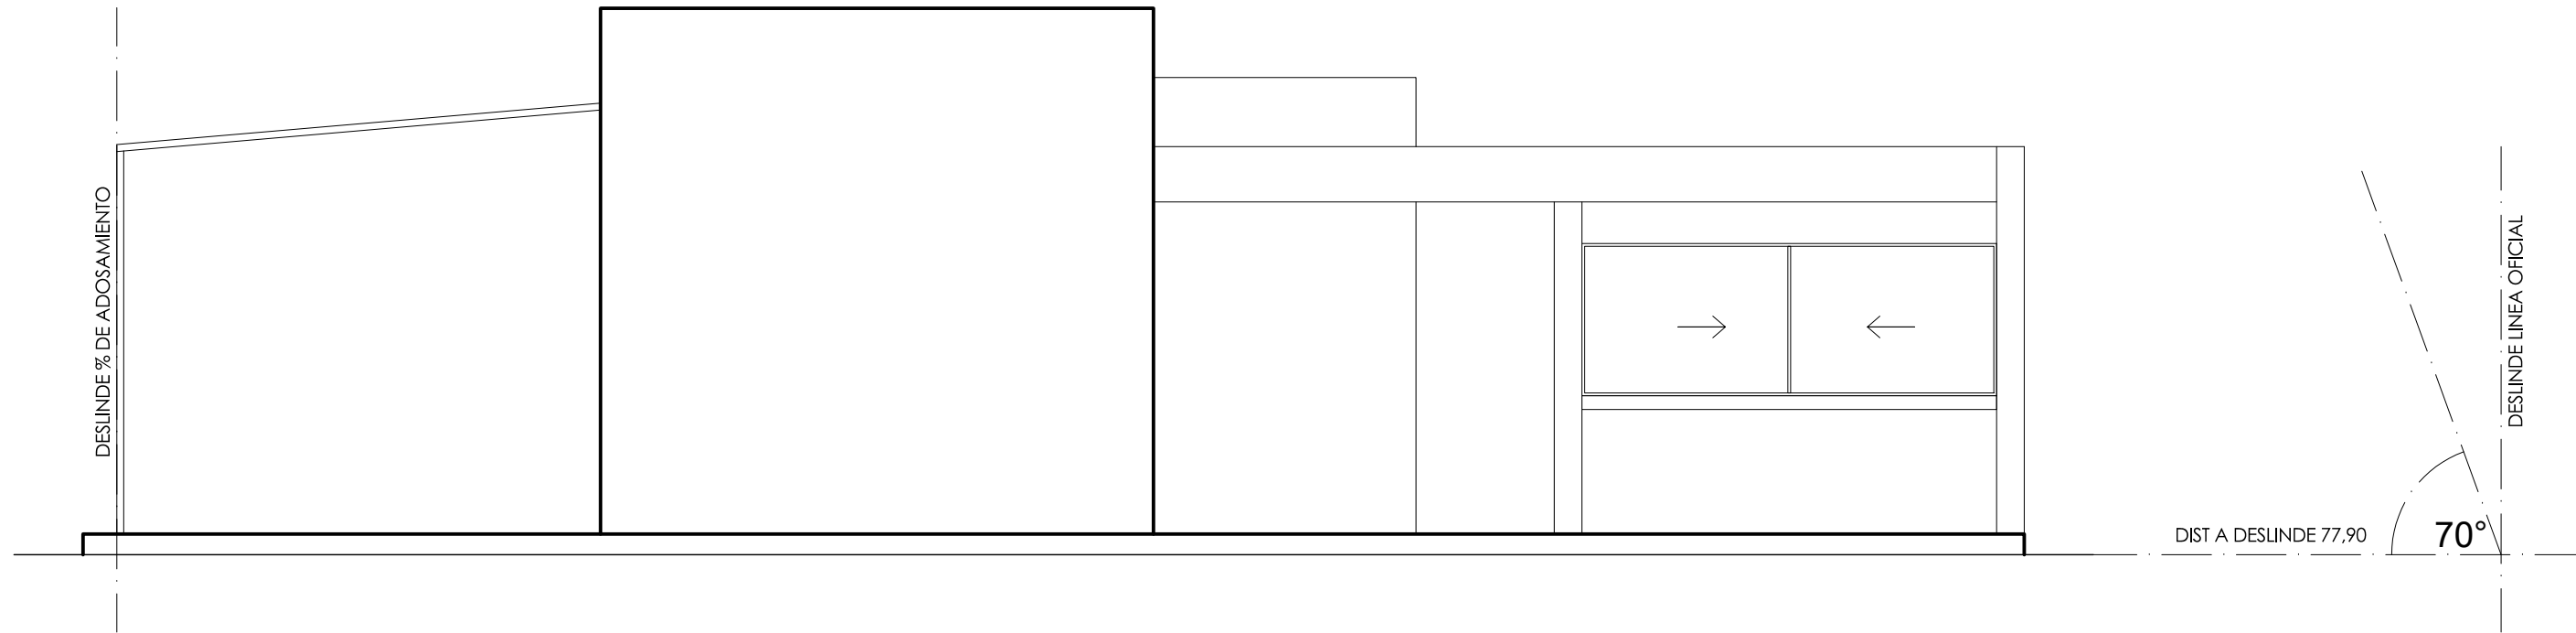

Kiosco / Enfermería, Elevación Poniente
Esc. 1:50

CONTENIDO LAMINA:
Elevaciones Kiosco / Enfermería

FIRMA PROPIETARIO / REPRESENTANTE LEGAL

C.C.A.F. de Los Andes
FIRMA ARQUITECTO

Tomás Fajardo Cabello
Arquitecto PUC - I.C.A. 8373
tomASFajardo@cfajardo.cl

FIRMA REVISOR MUNICIPAL

D.O.M. Municipalidad

CODIGO:
CRB - 2022 - RCRB


VERSIONES			
	NOMBRE	FECHA	EDICION
DIB	JMA	18-08-22	1.0
EDI			
EDI			
EDI			
EDI			
EDI			
EDI			
EDI			
EDI			
EDI			

OBRA:
CENTRO RECREACIONAL BEAUCHEFF
CAJA DE COMPENSACION LOS ANDES


DIRECCION : Beaucheff n°3500
COMUNA : Pedro Aguirre Cerda
ROL : 2971 - 1

	NOMBRE	FECHA	Lamina: 05 de 08
DIB	JMA	18-08-22	A05
REV	TFC	08-22	
ESC	INDICADAS		


CONTENIDO LAMINA:
Elevaciones

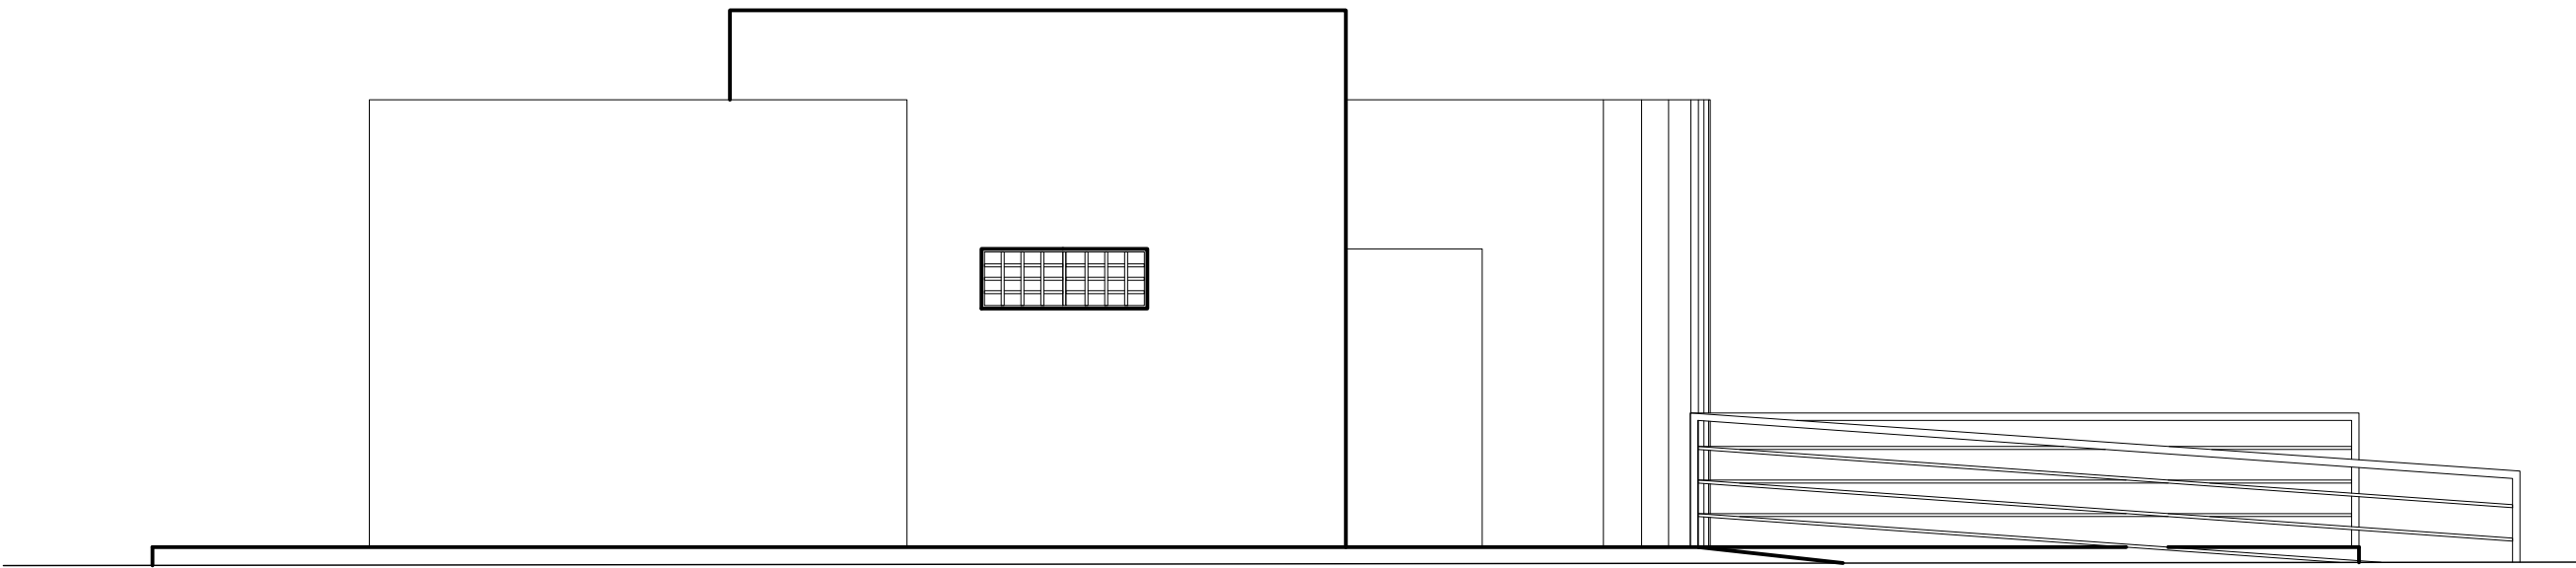


Camarines, Elevación Norte
Esc. 1:500

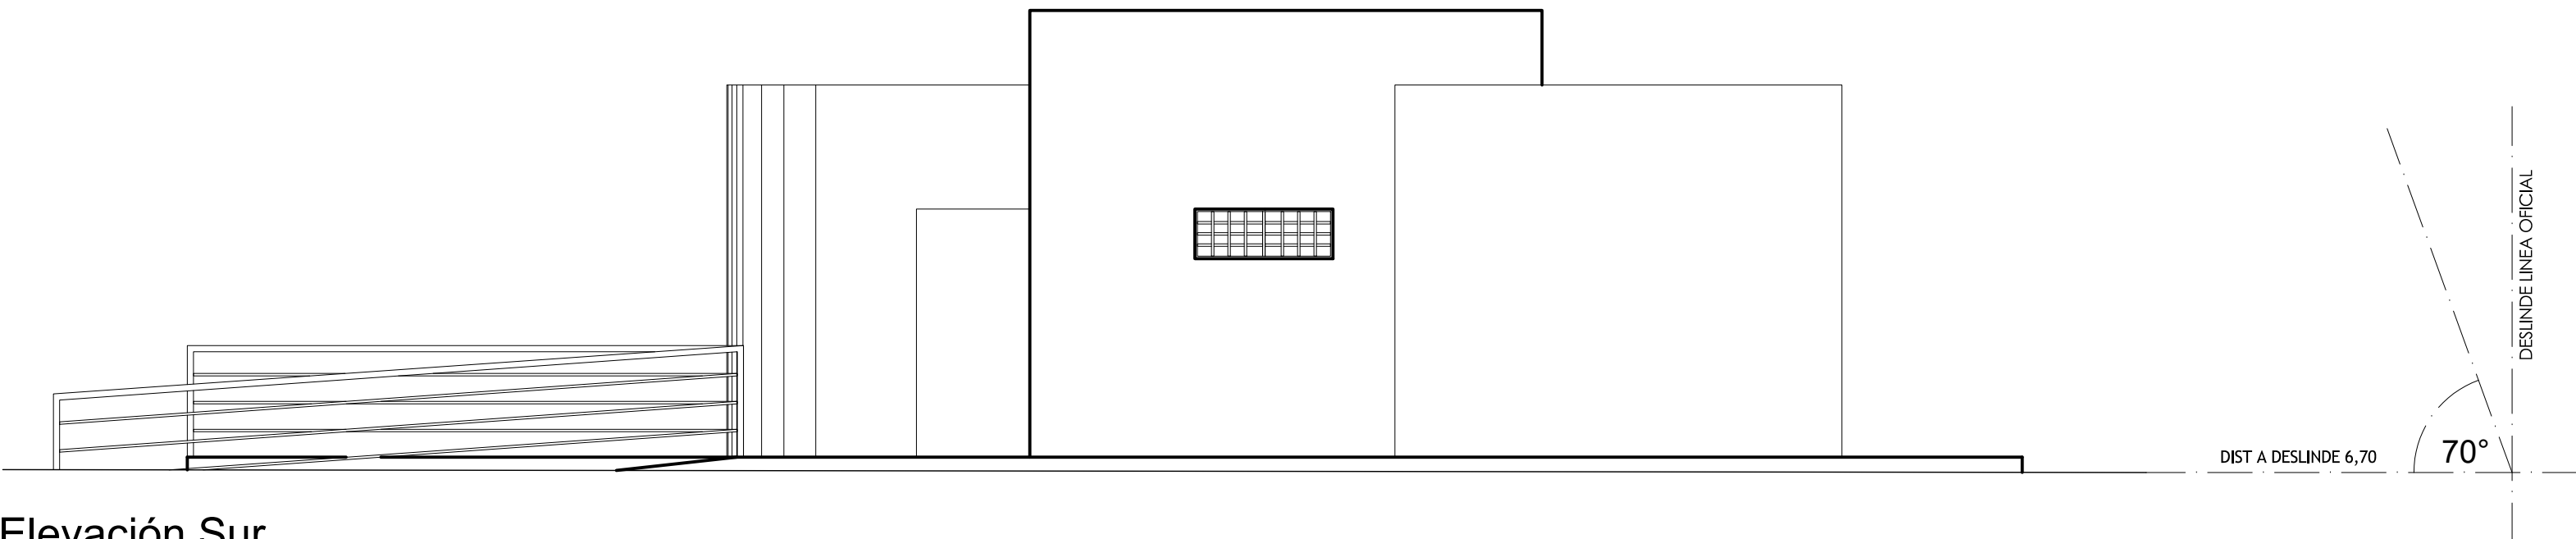


Camarines, Elevación Sur
Esc. 1:500

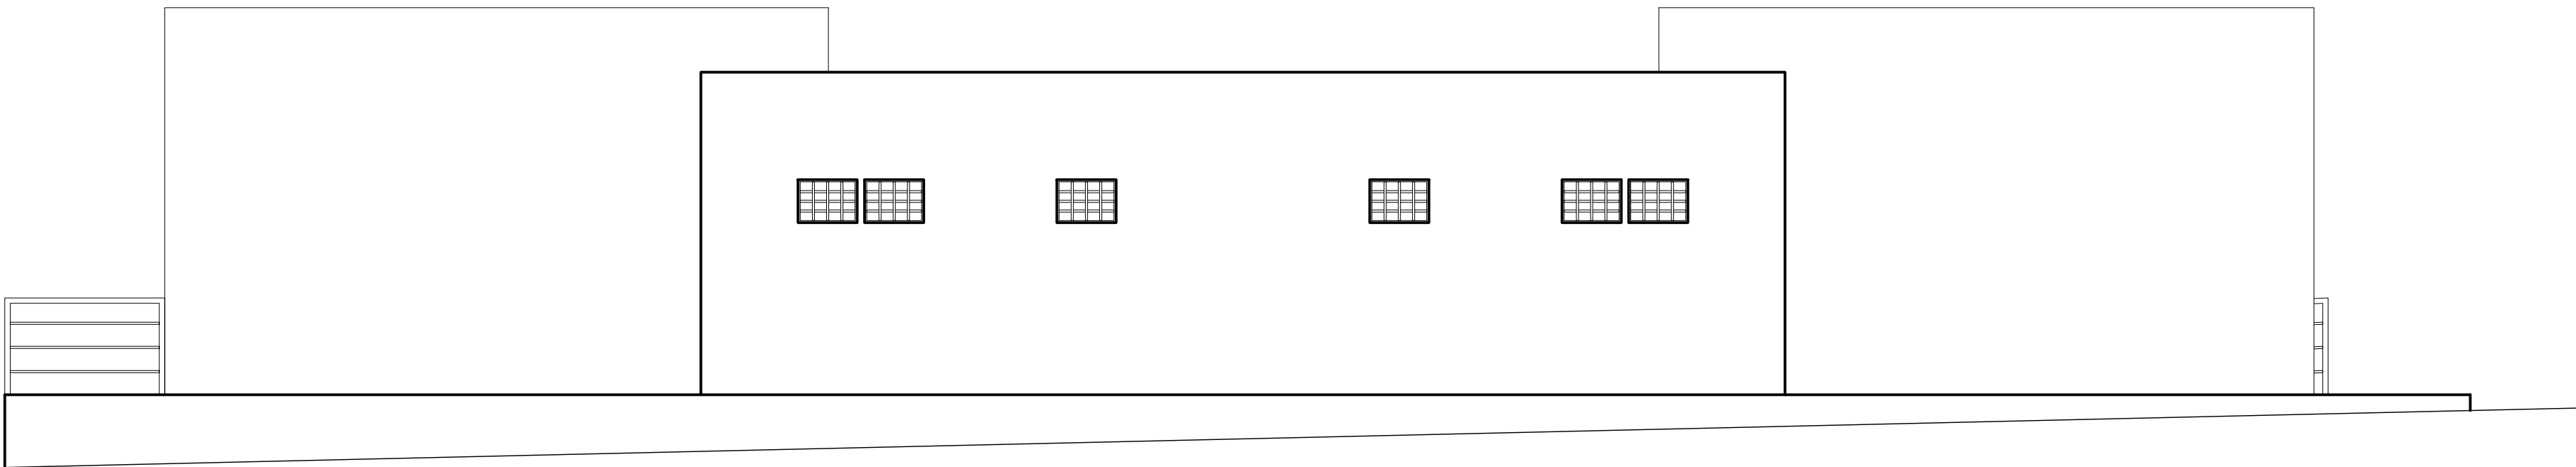

Camarines, Elevación Oriente
Esc. 1:500

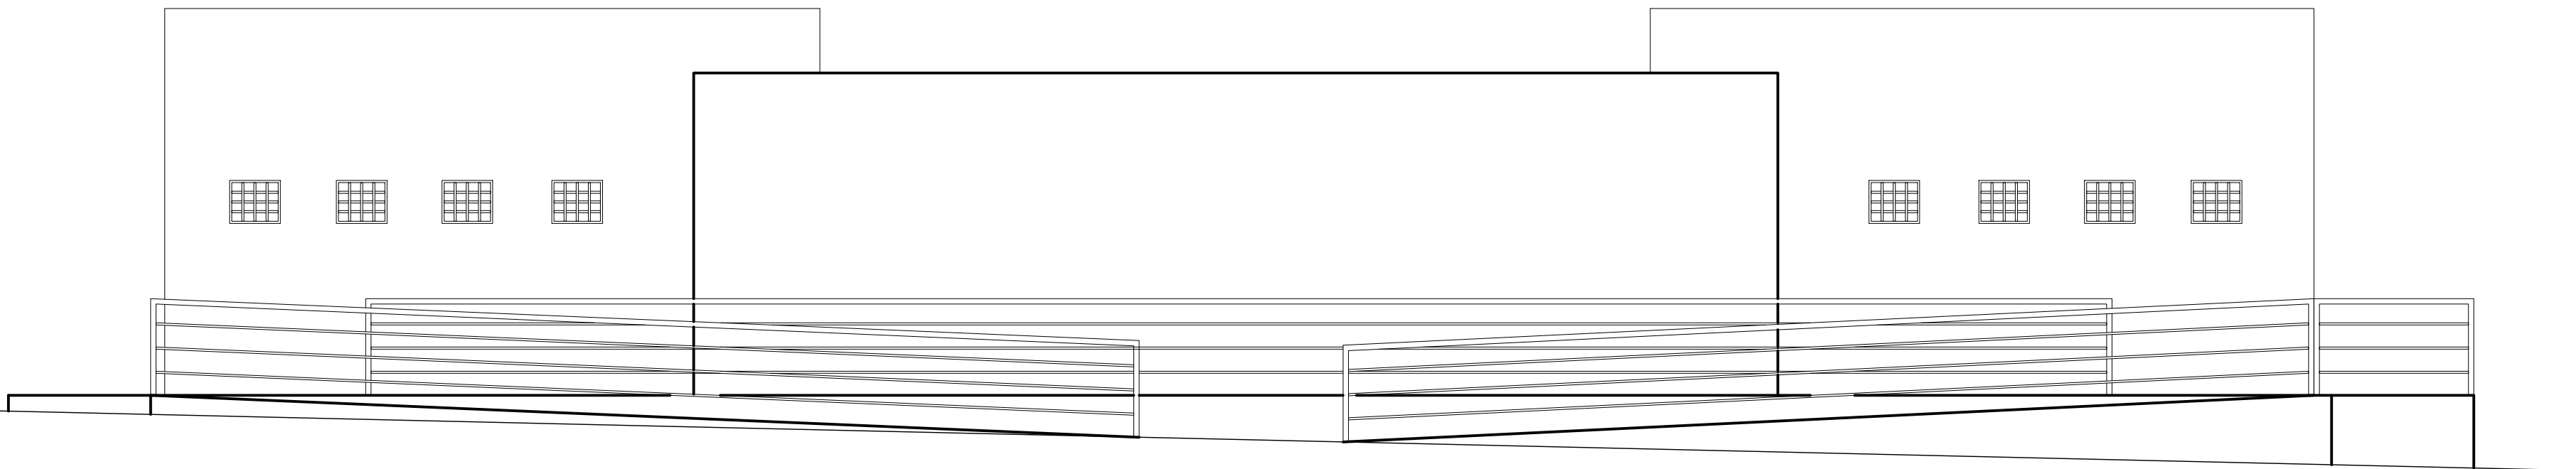

Camarines, Elevación Poniente
Esc. 1:500

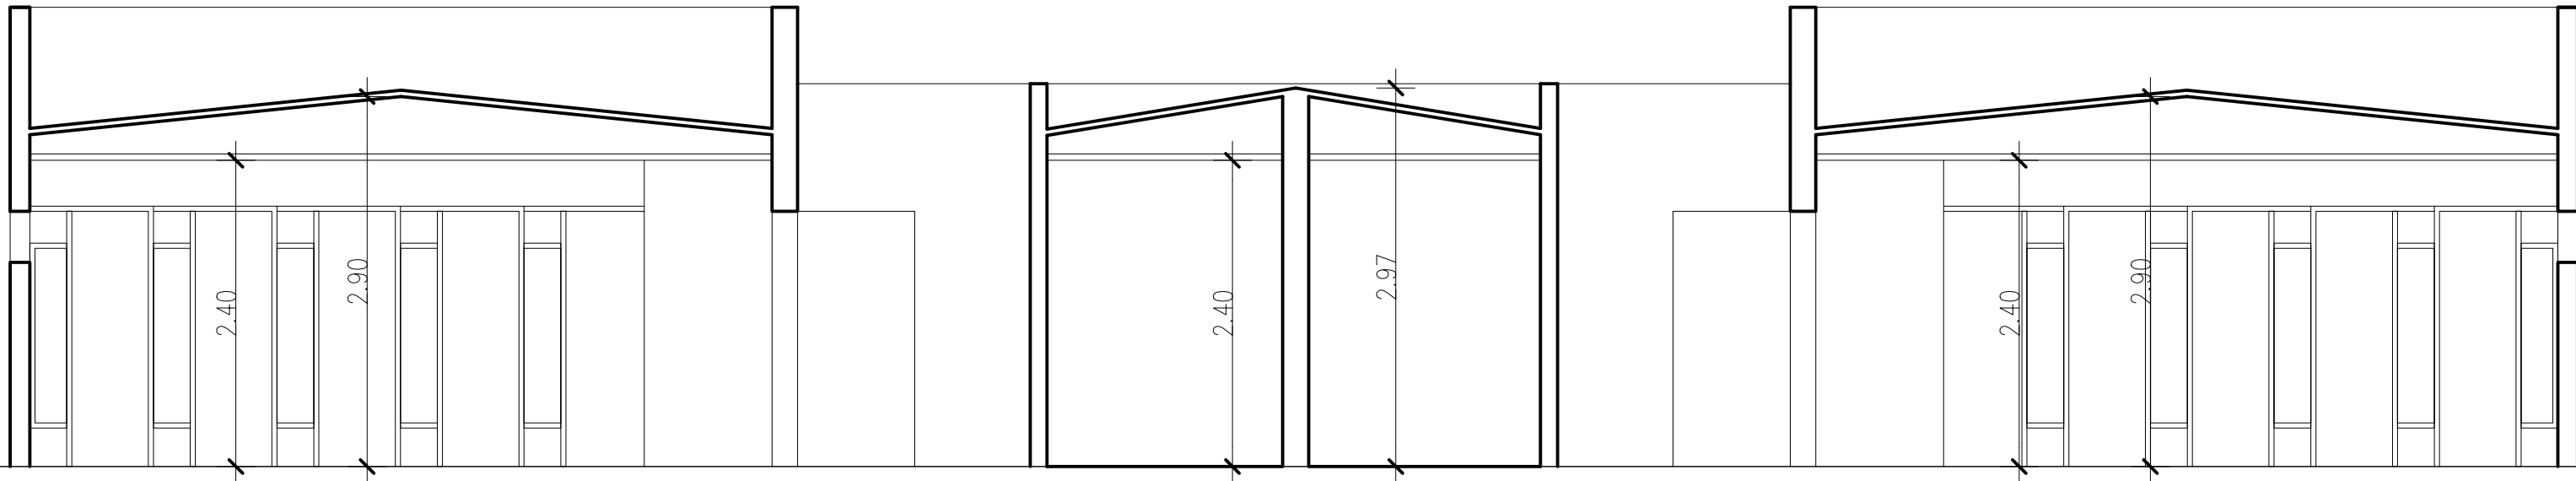

Camarines, Corte A-A
Esc. 1:500

FIRMA PROPIETARIO / REPRESENTANTE LEGAL

C.C.A.F. de Los Andes
FIRMA ARQUITECTO

Tomás Fajardo Cabello
Arquitecto PUC - I.C.A. 8373
tomASFajardo@cfajardo.cl

FIRMA REVISOR MUNICIPAL

D.O.M. Municipalidad

CODIGO:
CRB - 2022 - RCRB

VERSIONES			
	NOMBRE	FECHA	EDICION
DIB	JMA	18-08-22	1.0
EDI			
EDI			
EDI			
EDI			
EDI			
EDI			
EDI			
EDI			

OBRA:
CENTRO RECREACIONAL BEAUCHEFF
CAJA DE COMPENSACION LOS ANDES

DIRECCION : Beauceff n°3500
COMUNA : Pedro Aguirre Cerda
ROL : 2971 - 1

	NOMBRE	FECHA	Lamina: 06 de 08
DIB	JMA	18-08-22	A06
REV	TFC	08-22	
ESC	INDICADAS		

CONTENIDO LAMINA:
Plantas de Cubiertas

FIRMA PROPIETARIO / REPRESENTANTE LEGAL

C.C.A.F. de Los Andes
FIRMA ARQUITECTO

Tomás Fajardo Cabello
Arquitecto PUC - I.C.A. 8373
tomASFajardo@cfajardo.cl

FIRMA REVISOR MUNICIPAL

D.O.M. Municipalidad

CODIGO:
CRB - 2022 - RCRB


VERSIONES			
	NOMBRE	FECHA	EDICION
DIB	JMA	18-08-22	1.0
EDI			
EDI			
EDI			
EDI			
EDI			
EDI			
EDI			
EDI			

OBRA:
**CENTRO
RECREACIONAL
BEAUCHEFF**


CAJA DE COMPENSACION LOS ANDES

DIRECCION : Beaucheff n°3500
COMUNA : Pedro Aguirre Cerda
ROL : 2971 - 1


	NOMBRE	FECHA	Lamina: 07 de 08 A07
DIB	JMA	18-08-22	
REV	TFC	08-22	
ESC	INDICADAS		

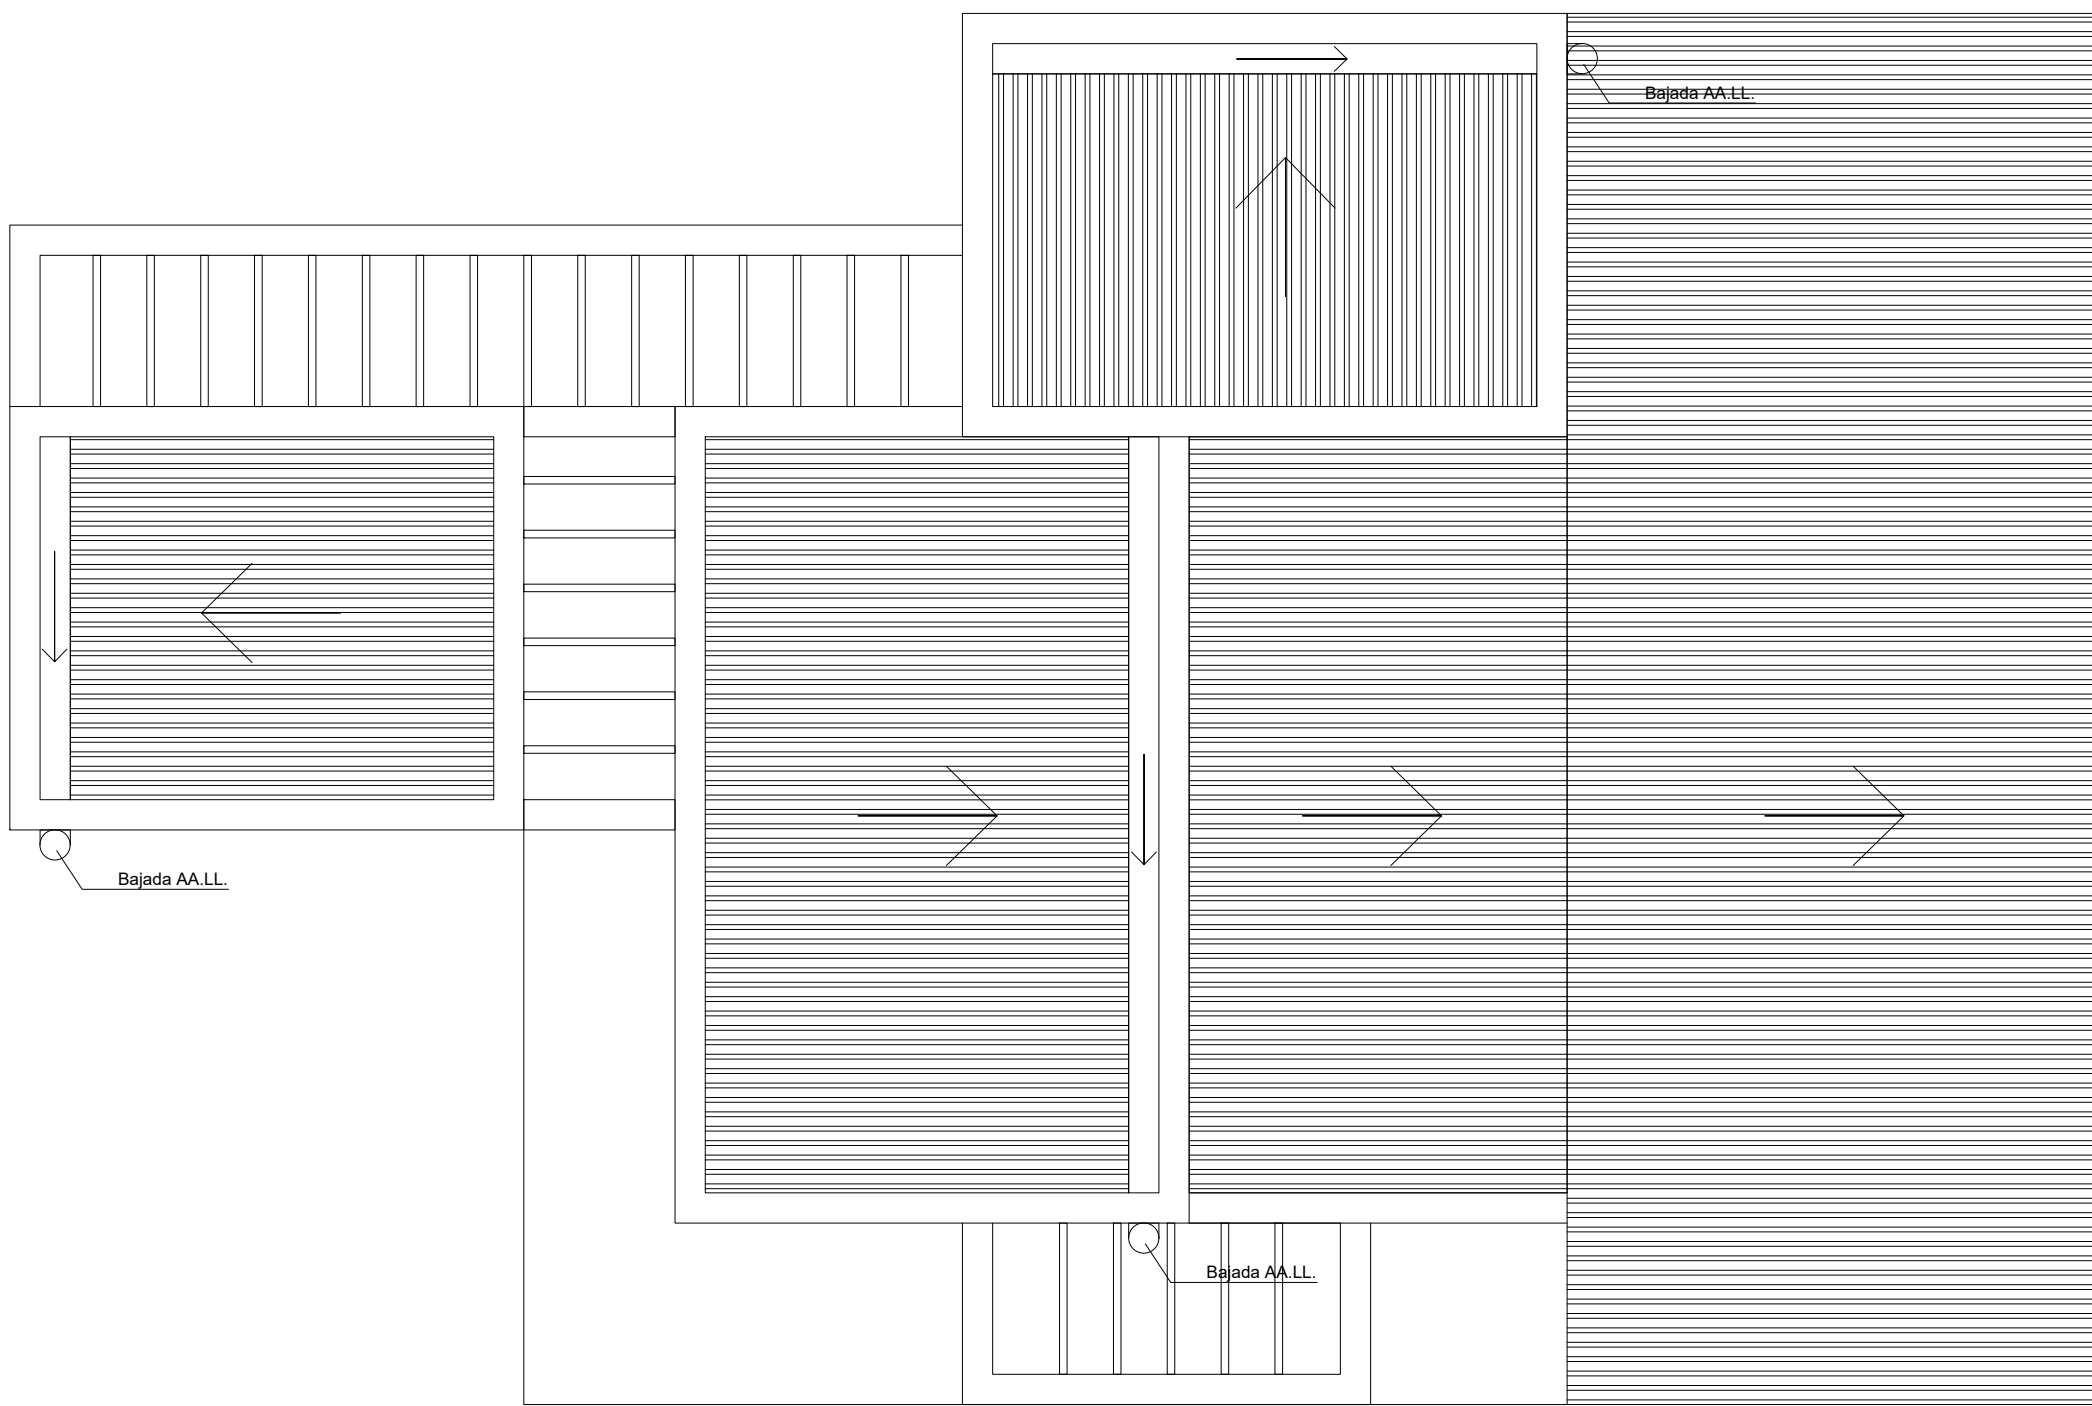


Planta de Cubiertas Acceso
Esc. 1:50

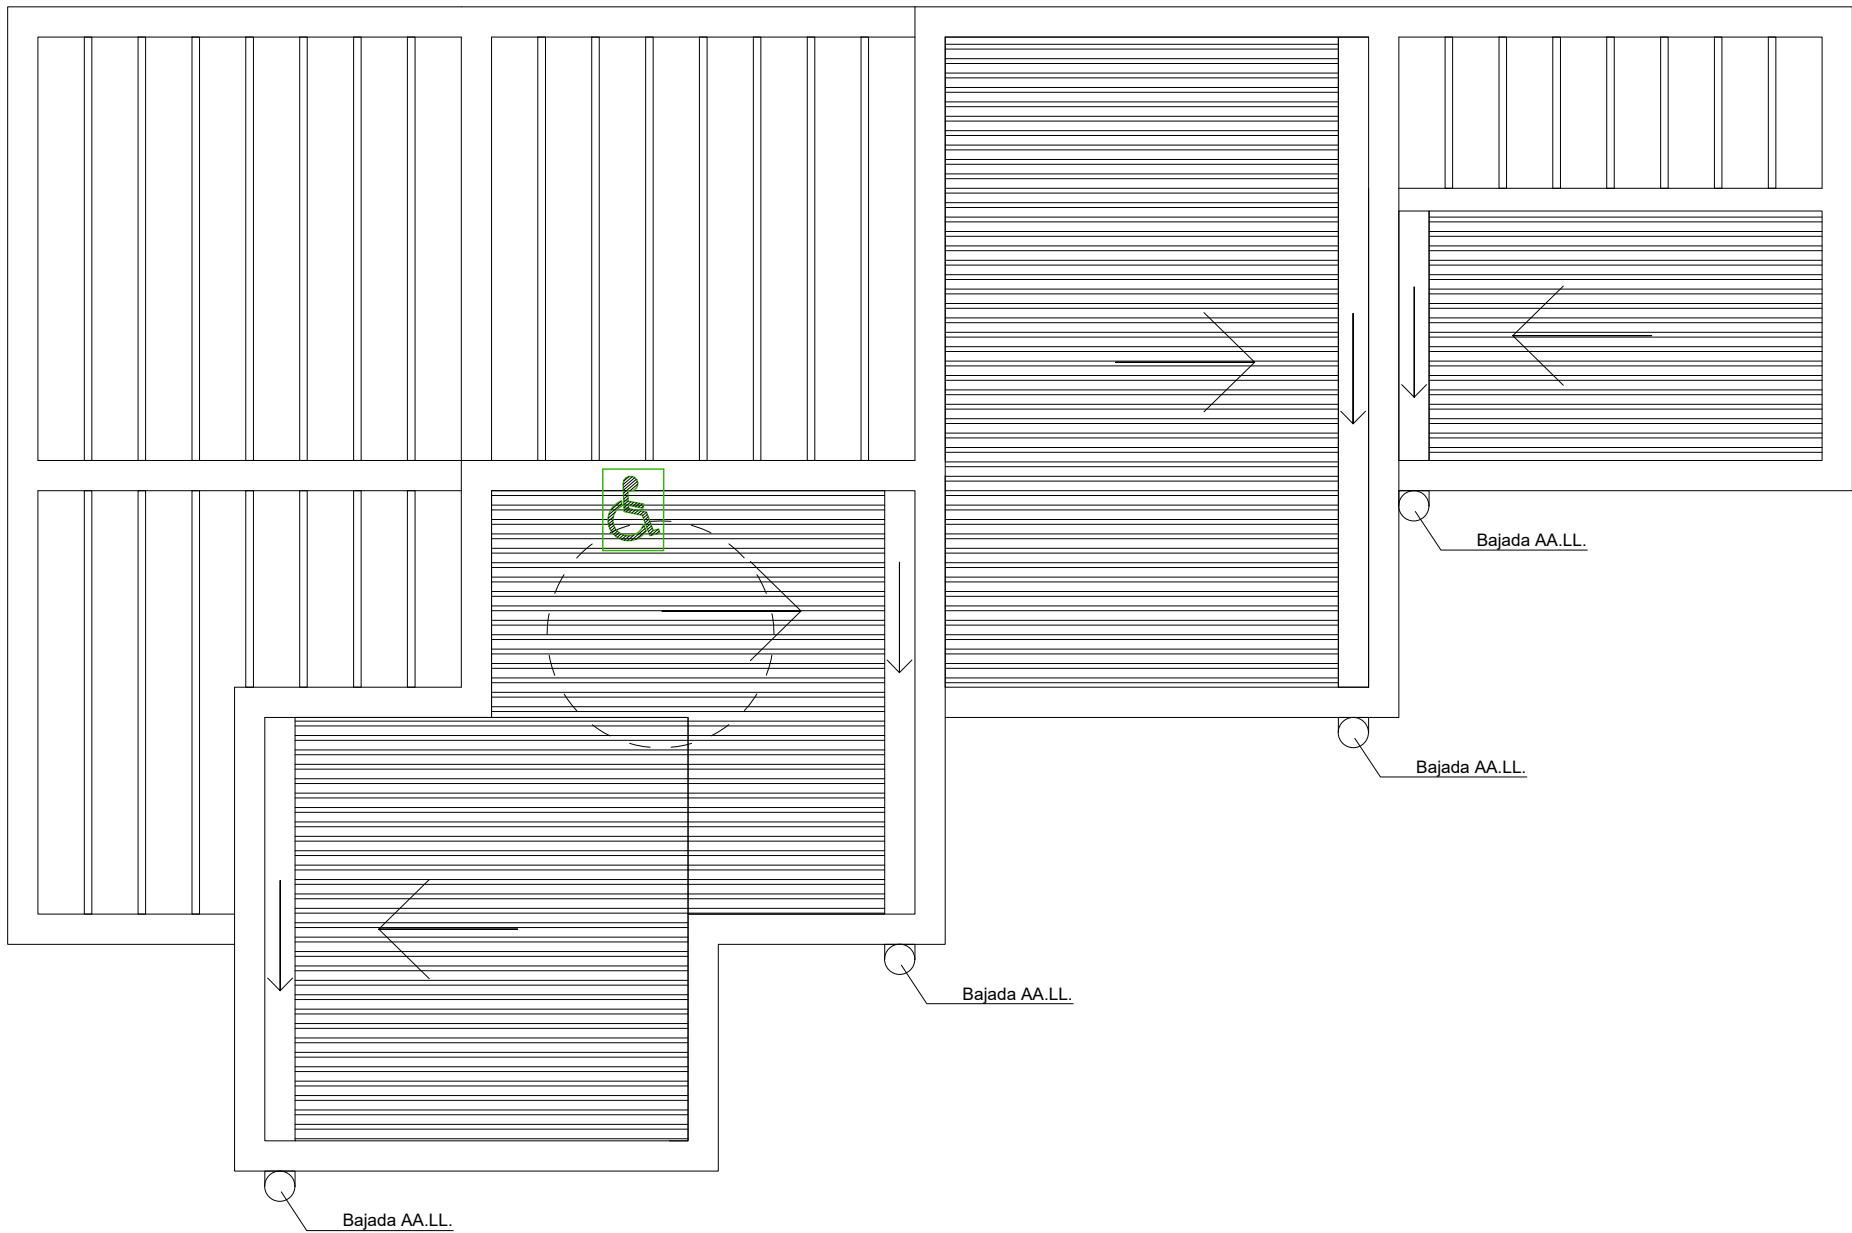

Planta de Cubiertas Kiosco / Enfermeria
Esc. 1:50

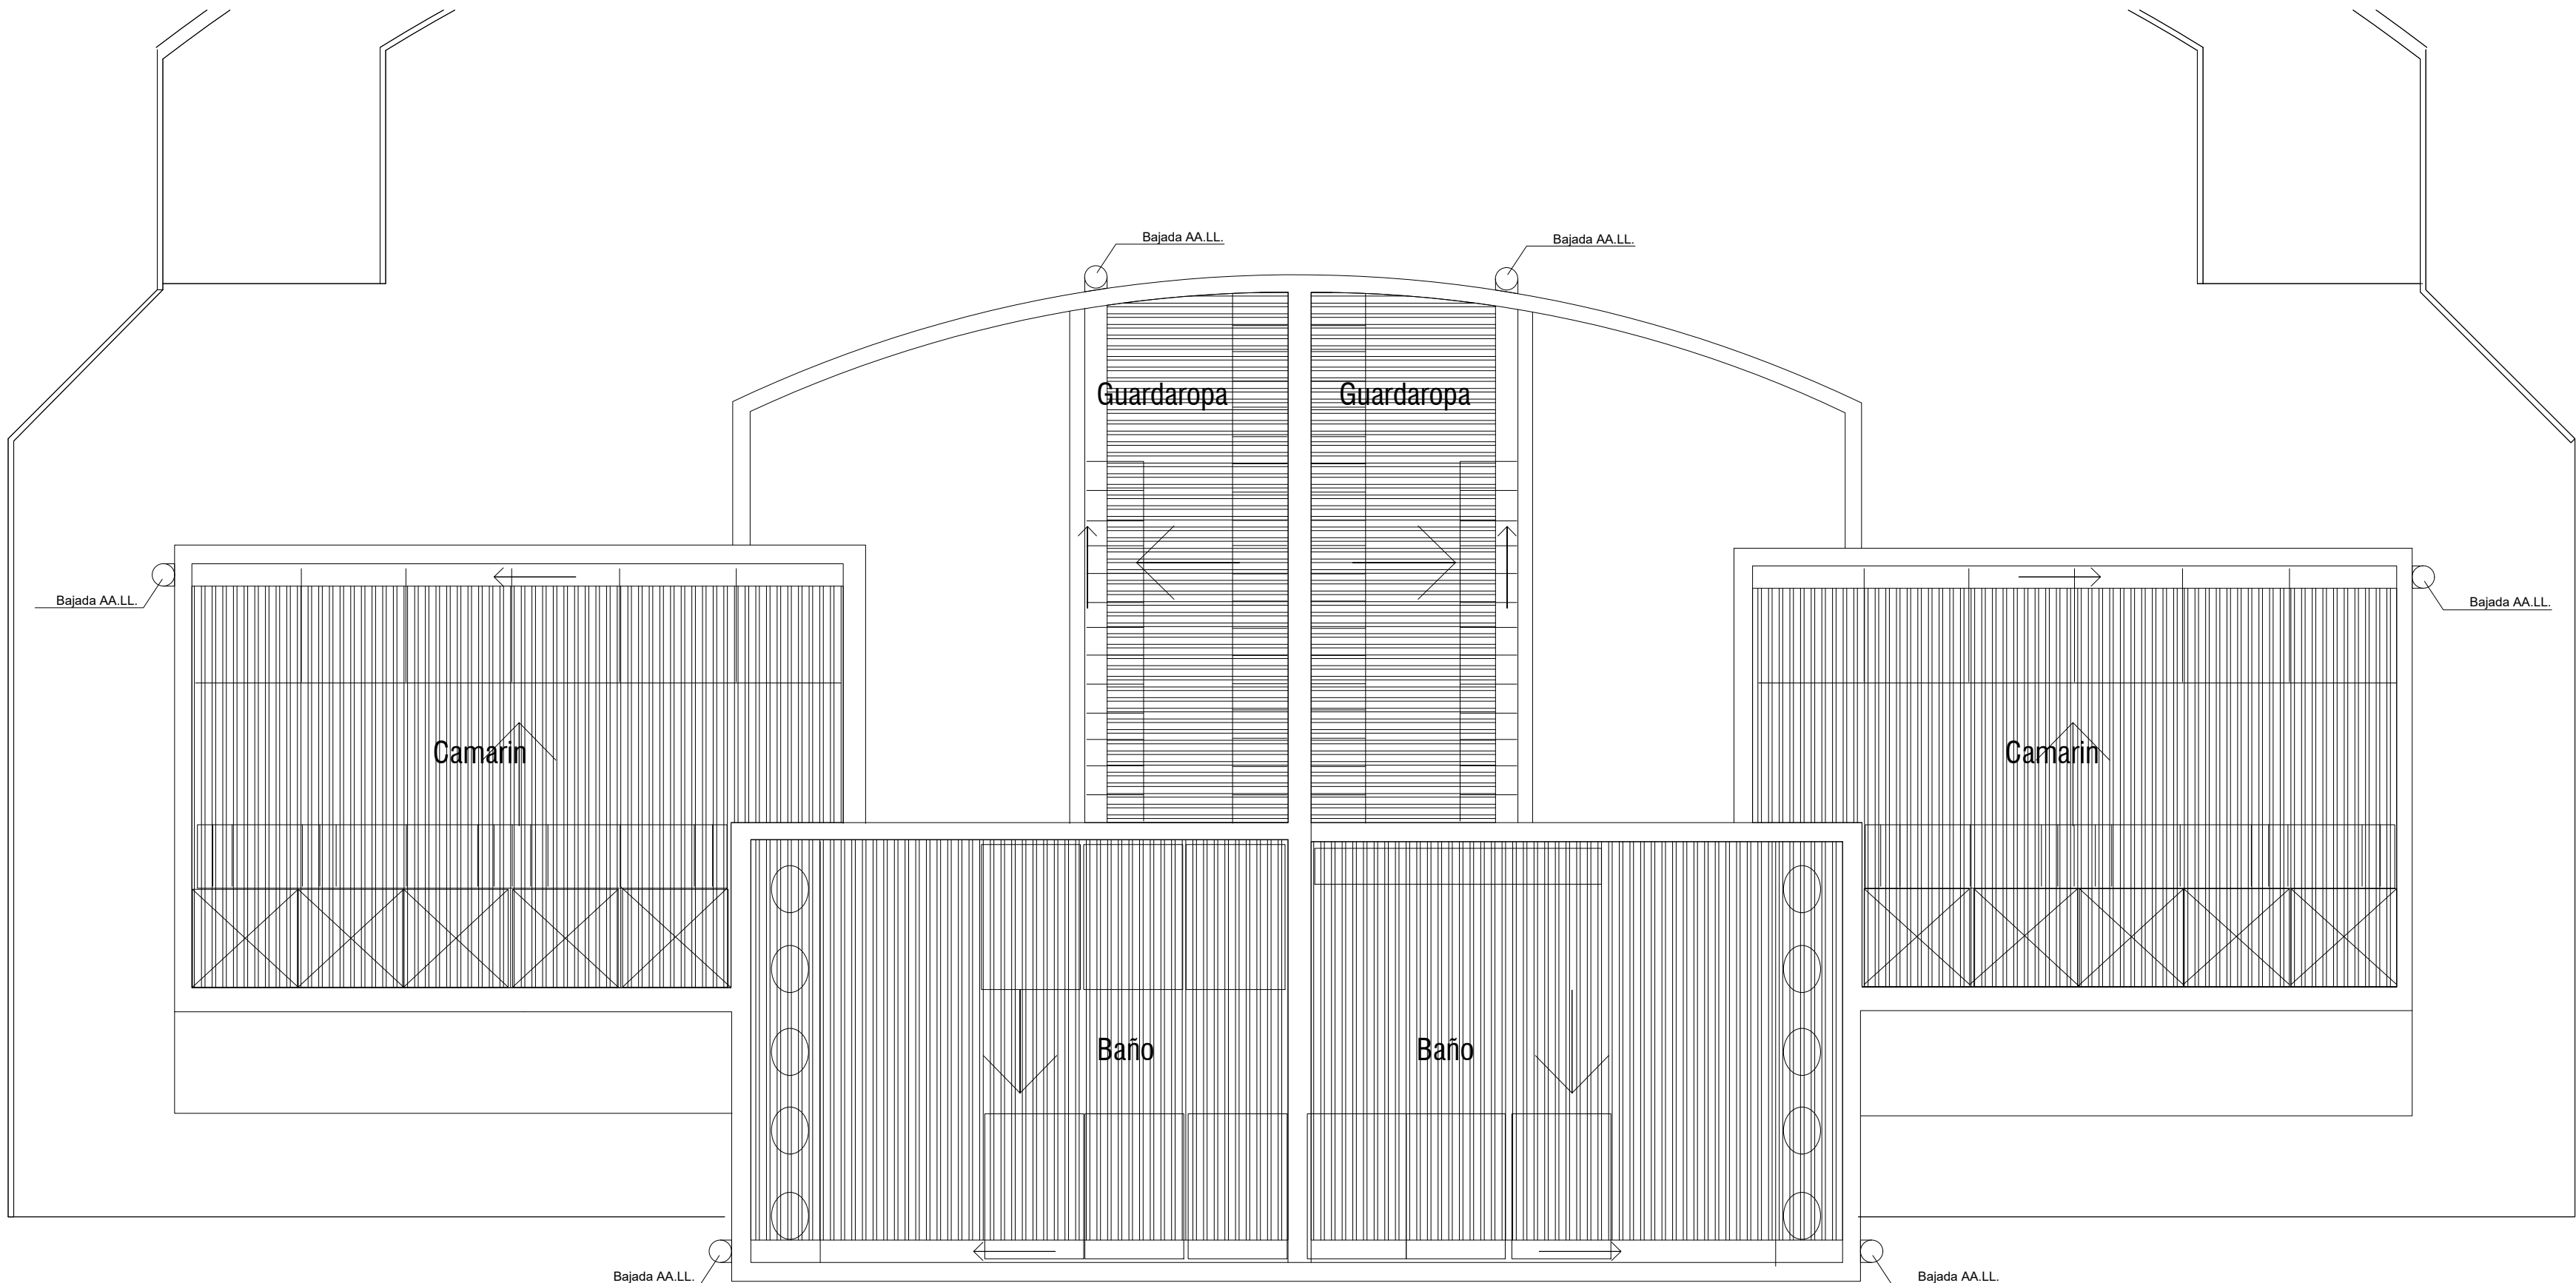


Planta de Cubiertas Camarines
Esc. 1:50

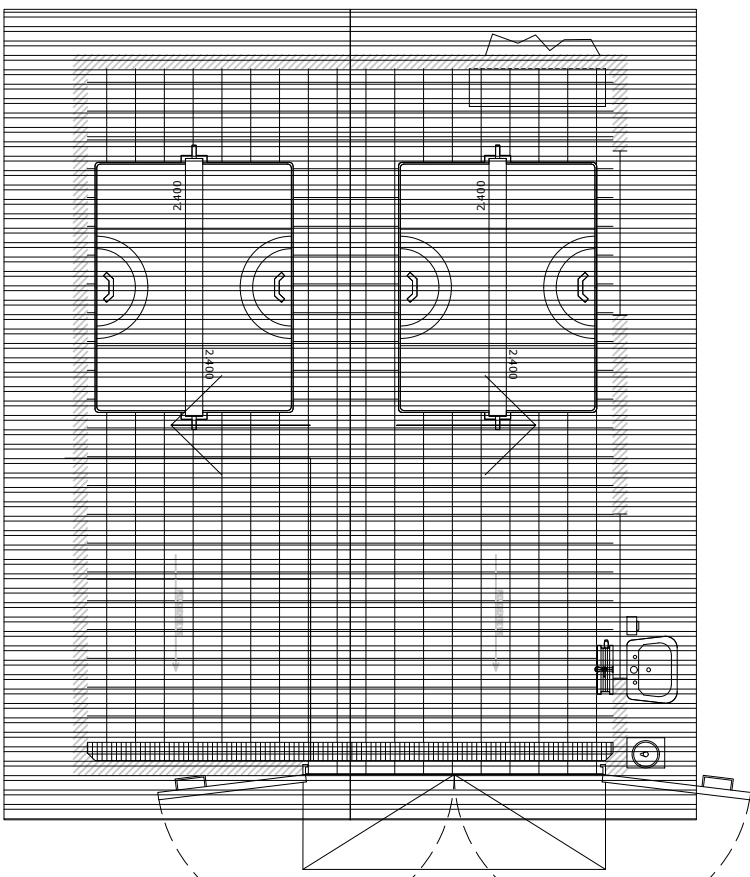


Planta de Cubiertas S. de Basura
Esc. 1:50


Superficies Acceso
Esc. 1:100

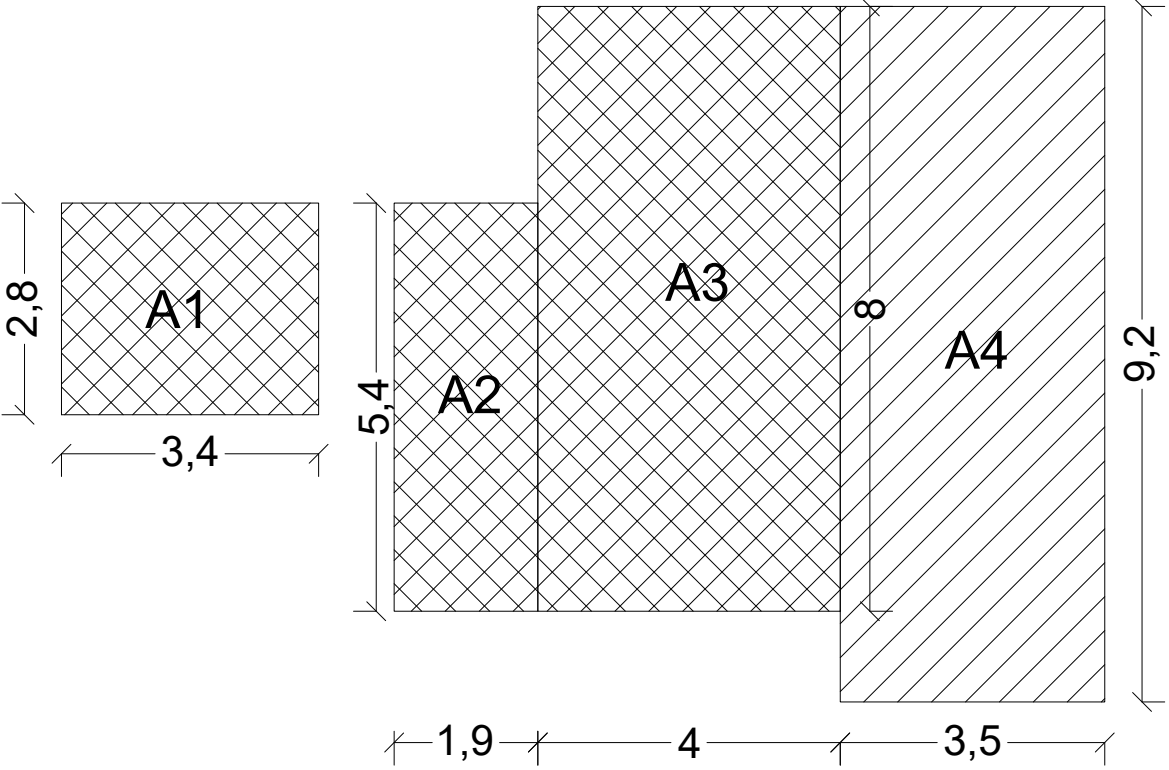


Superficies Kiosco / Enfermeria
Esc. 1:100

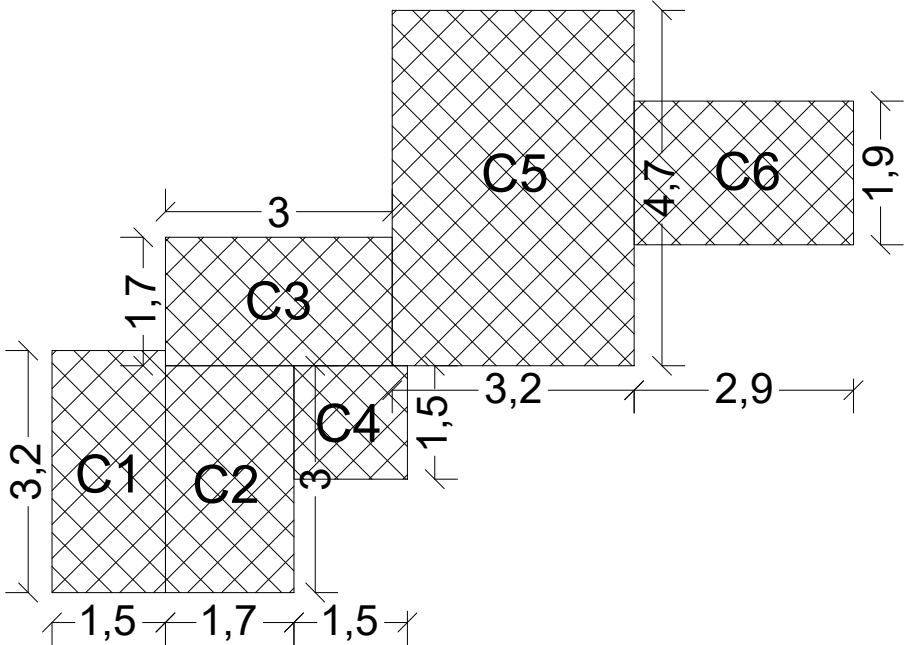

Superficies Camarines
Esc. 1:100

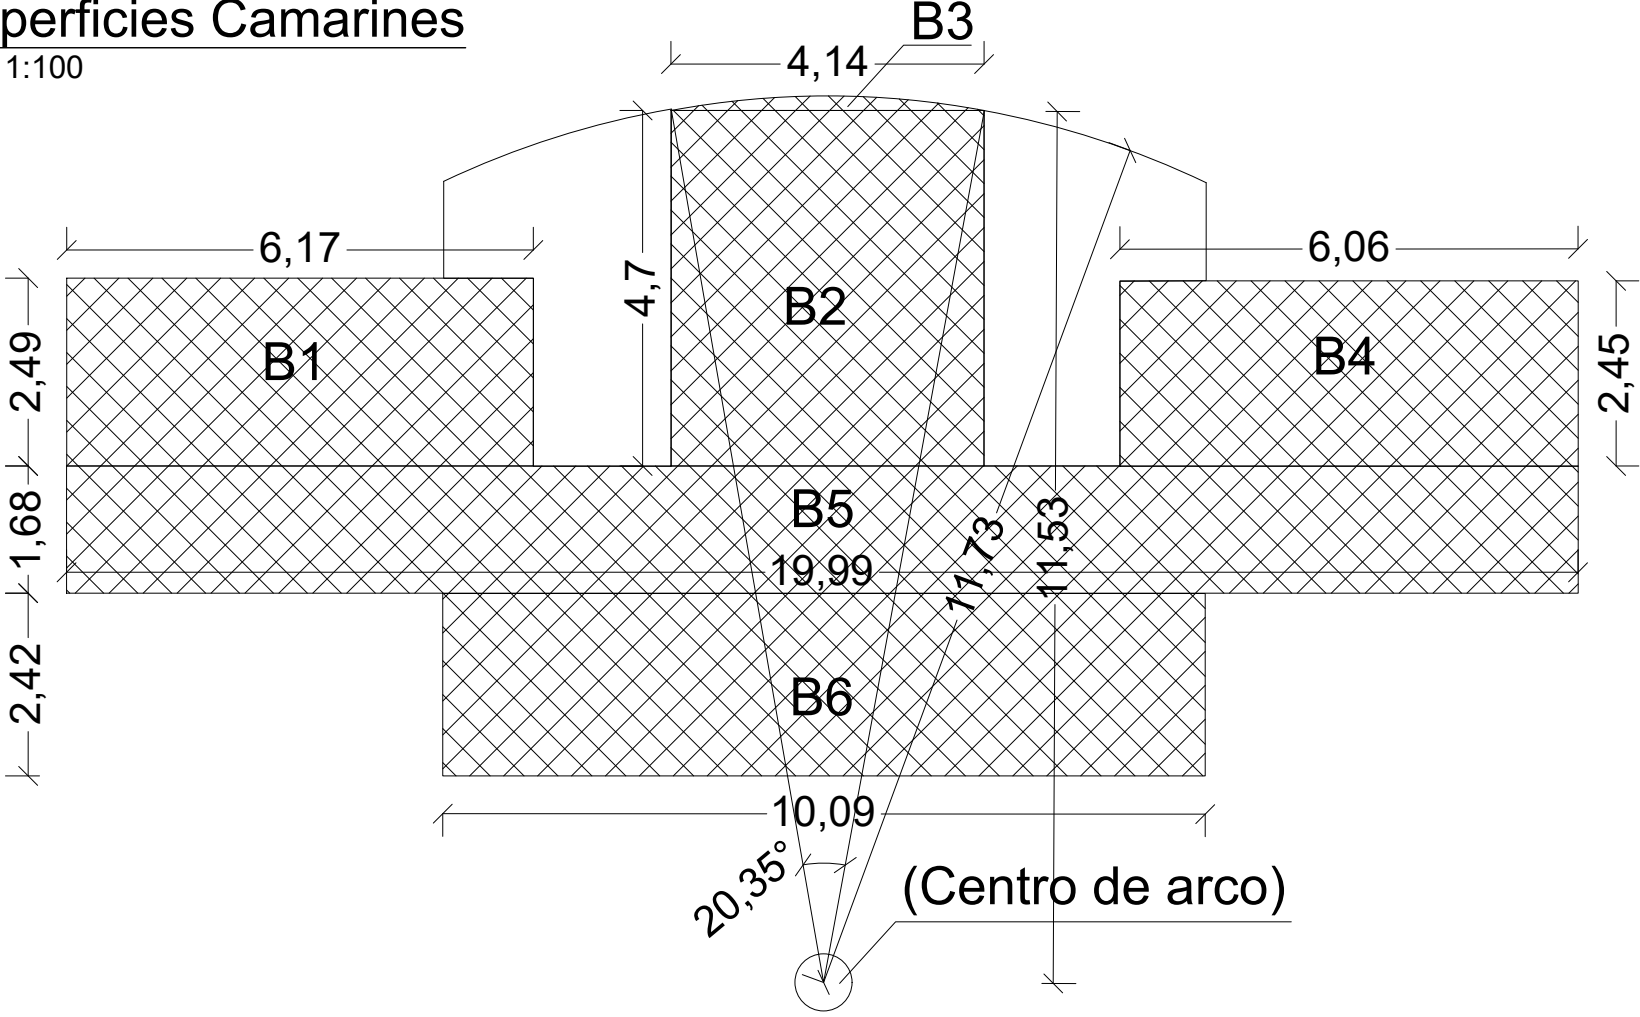

Superficies S.Basura
Esc. 1:100

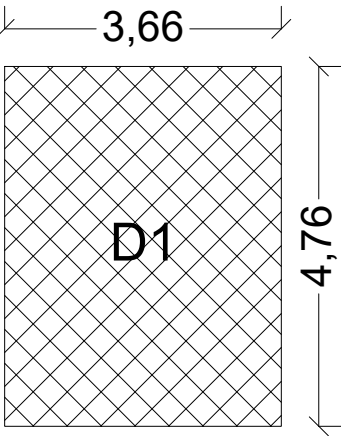

Resumen de Superficies			
Poligono	Lado	Lado	TOTAL
A1	3,40	x 2,80	6,20
A2	1,90	x 5,40	7,30
A3	4,00	x 8,00	12,00
A4	3,50	x 9,20	6,35
SubTotal			31,85
B1	6,17	x 2,49	8,66
B2	4,14	x 4,70	8,84
B3*	-	-	0,55
B4	6,06	x 2,45	8,51
B5	19,99	x 1,68	21,67
B6	10,09	x 2,42	12,51
SubTotal			60,74
C1	1,50	x 3,20	4,70
C2	1,70	x 3,00	4,70
C3	3,00	x 1,70	4,70
C4	1,50	x 1,50	3,00
C5	3,20	x 4,70	7,90
C6	2,90	x 1,90	4,80
SubTotal			29,80
D1	3,66	x 4,76	8,42
SubTotal			8,42
TOTAL			130,81

* A segm. Circ = A seccion Circ - A triangulo
A Secc Circ = (20,35 x 3,14/360) x 11,73²
= 24,42
A Triangulo = (4,14 x 11,53) / 2
= 23,87
A Segm. Circ.= 24,42 - 23,87 0,55

Estudio de Carga de Ocupación					
Poligono	Superf.	Dest.	C.Ocup.		Total
A1	6,20	Oficina	10,00	m ² x p	0,62
A2	7,30	Oficina	10,00	m ² x p	0,73
A3	12,00	Taller	5,00	m ² x p	2,40
A4	6,35	Taller	5,00	m ² x p	1,27
SubTotal	31,85				5,02
B1	8,66	Camarines	4,00	m ² x p	2,17
B2	8,84	Camarines	4,00	m ² x p	2,21
B3*	0,55	Camarines	4,00	m ² x p	0,14
B4	8,51	Camarines	4,00	m ² x p	2,13
B5	21,67	Camarines	4,00	m ² x p	5,42
B6	12,51	Camarines	4,00	m ² x p	3,13
SubTotal	60,74				15,19
C1	4,70	Cocina	15,00	m ² x p	0,31
C2	4,70	Cocina	15,00	m ² x p	0,31
C3	4,70	Cocina	15,00	m ² x p	0,31
C4	3,00	Cocina	15,00	m ² x p	0,20
C5	7,90	Cons.(Salud)	3,00	m ² x p	2,63
C6	4,80	Cons.(Salud)	3,00	m ² x p	1,60
SubTotal	29,80				5,37
D1	8,42	Bodega	40,00	m ² x p	0,21
SubTotal	8,42				0,21
TOTAL	130,81				26

Cuadro de Superficies Normativas				
Destino de la Edificación Equipamiento (Deporte)	Sup.Total Existente 0,00	Sup.Total Proyectada 130,81	N° Pisos sobre N.N.T. 1	
Superficie Total de Terreno	Coef. Constructibilidad		Coef. de Ocupación de Suelo	
17.009,50	Permitido	1,500	Permitido	0,600
	Existente	0,000	Existente	0,000
	Proyectado	0,008	Proyectado	0,008

CONTENIDO LAMINA:
Cuadros de Superficies

FIRMA PROPIETARIO / REPRESENTANTE LEGAL

C.C.A.F. de Los Andes
FIRMA ARQUITECTO

Tomás Fajardo Cabello
Arquitecto PUC - I.C.A. 8373
tomasfajardo@cfajardo.cl

FIRMA REVISOR MUNICIPAL

D.O.M. Municipalidad

CODIGO:

CRB - 2022 - RCRB

VERSIONES

	NOMBRE	FECHA	EDICION
DIB	JMA	18-08-22	1.0
EDI			
EDI			
EDI			
EDI			
EDI			
EDI			
EDI			
EDI			


OBRA:

**CENTRO
RECREACIONAL
BEAUCHEFF**

CAJA DE COMPENSACION LOS ANDES



DIRECCION : Beaucheff n°3500
COMUNA : Pedro Aguirre Cerda
ROL : 2971 - 1

	NOMBRE	FECHA	Lamina: 08 de 08 A08
DIB	FBE	18-08-22	
REV	TFC	08-22	
ESC	INDICADAS		

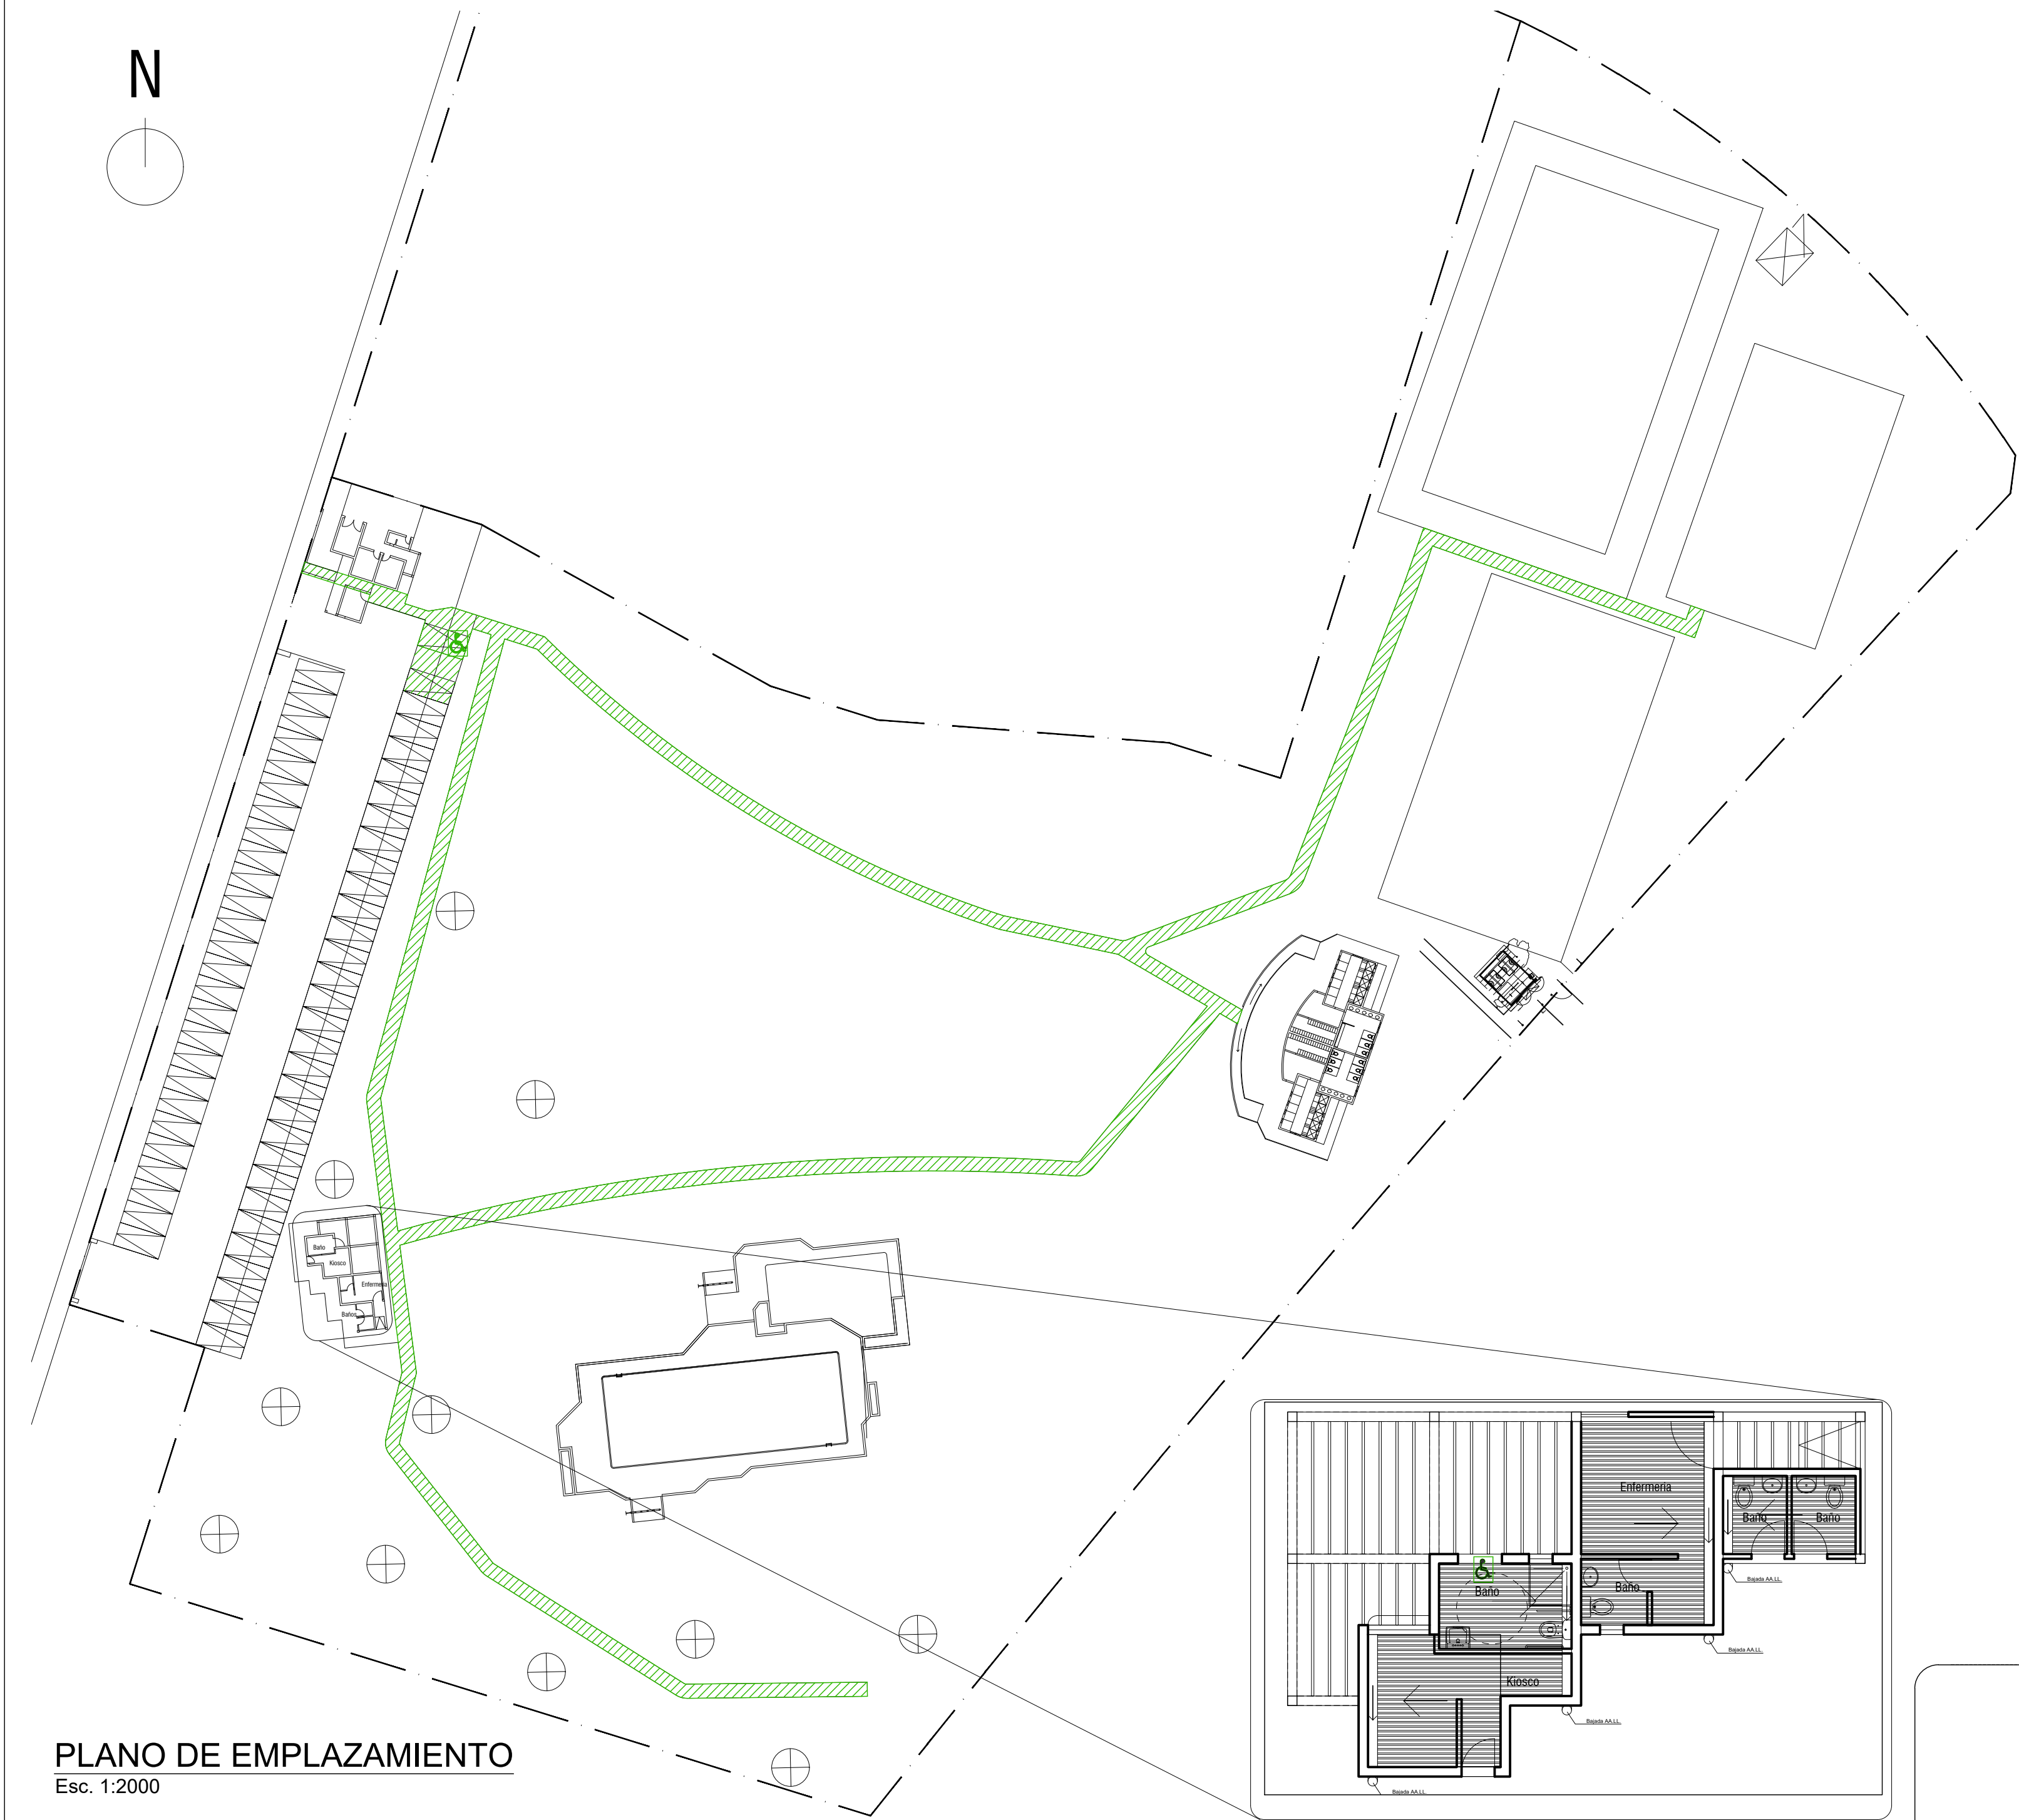

PLANO DE EMPLAZAMIENTO
Esc. 1:2000

Detalle de baño universal
Esc. 1:25

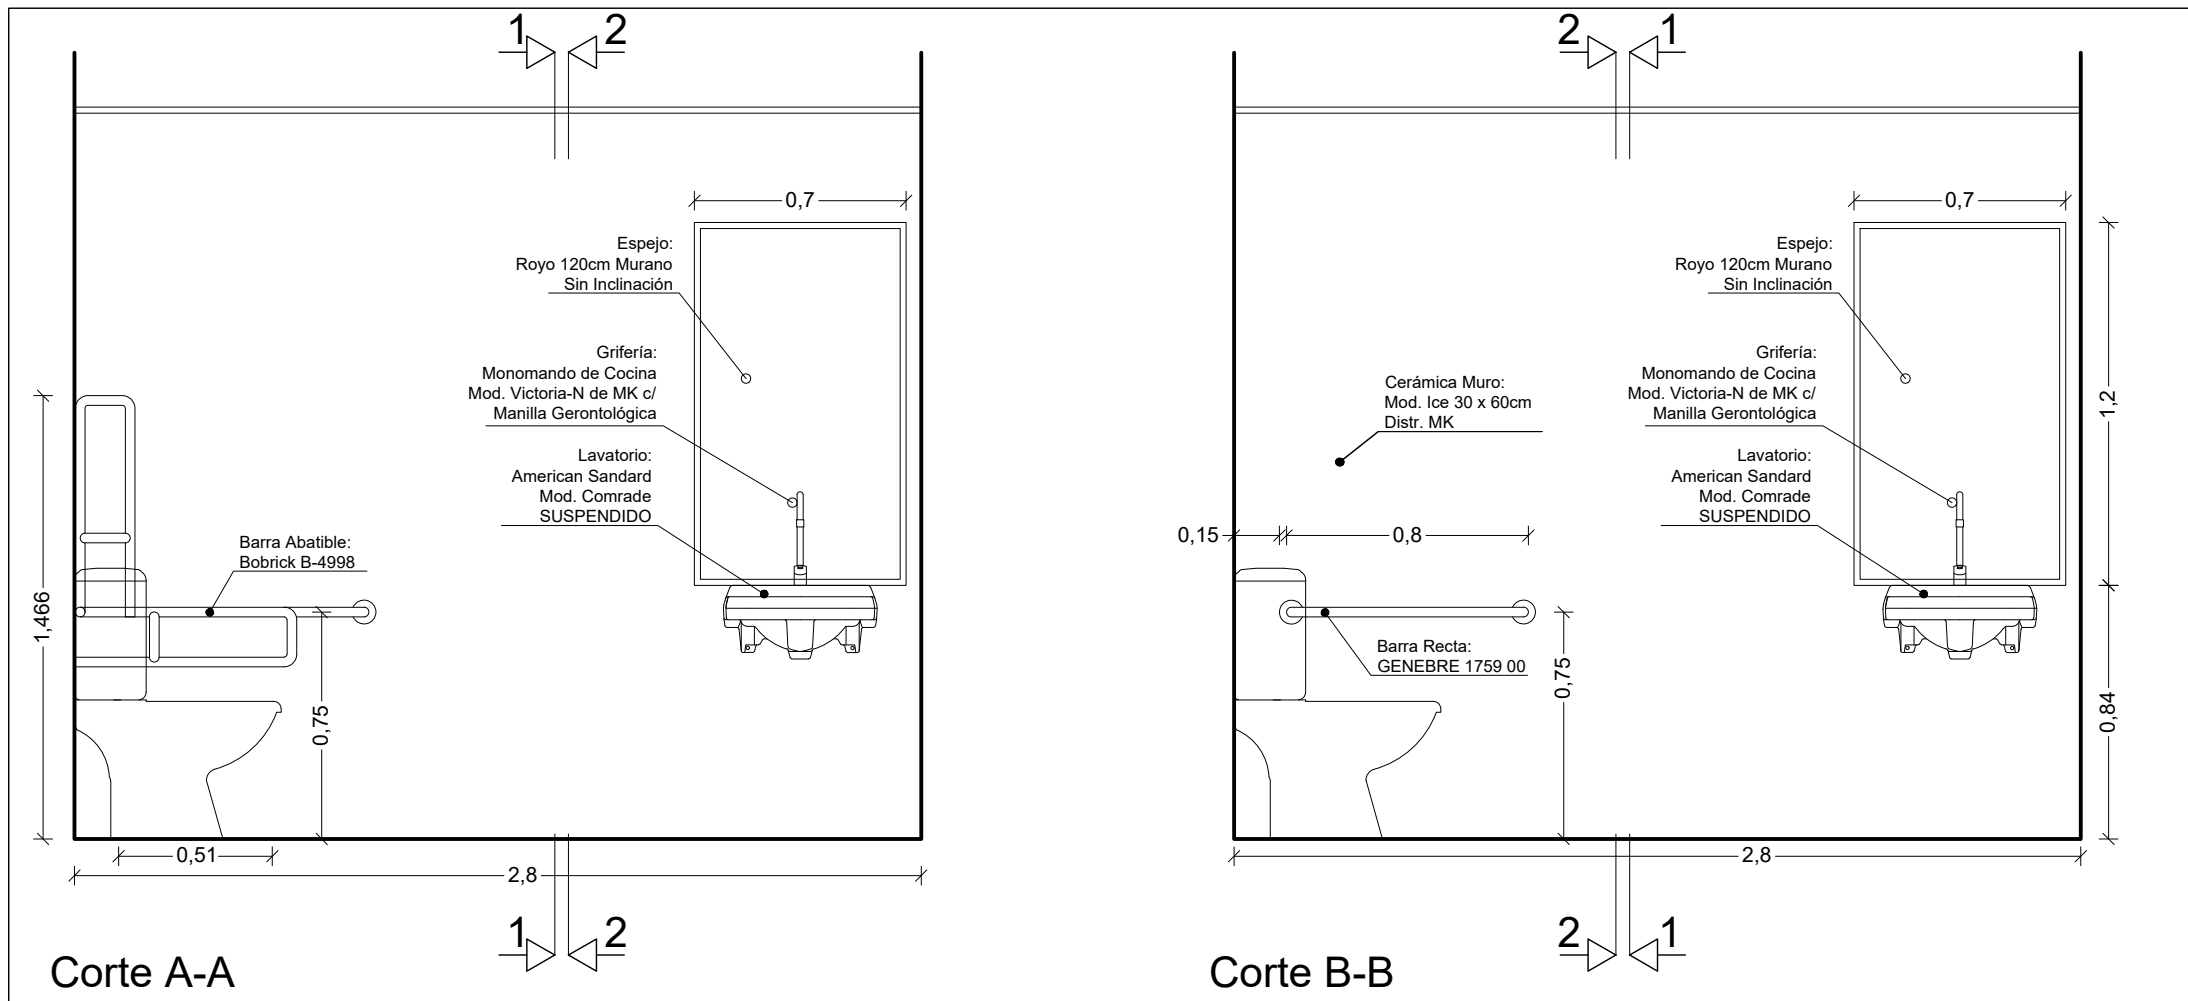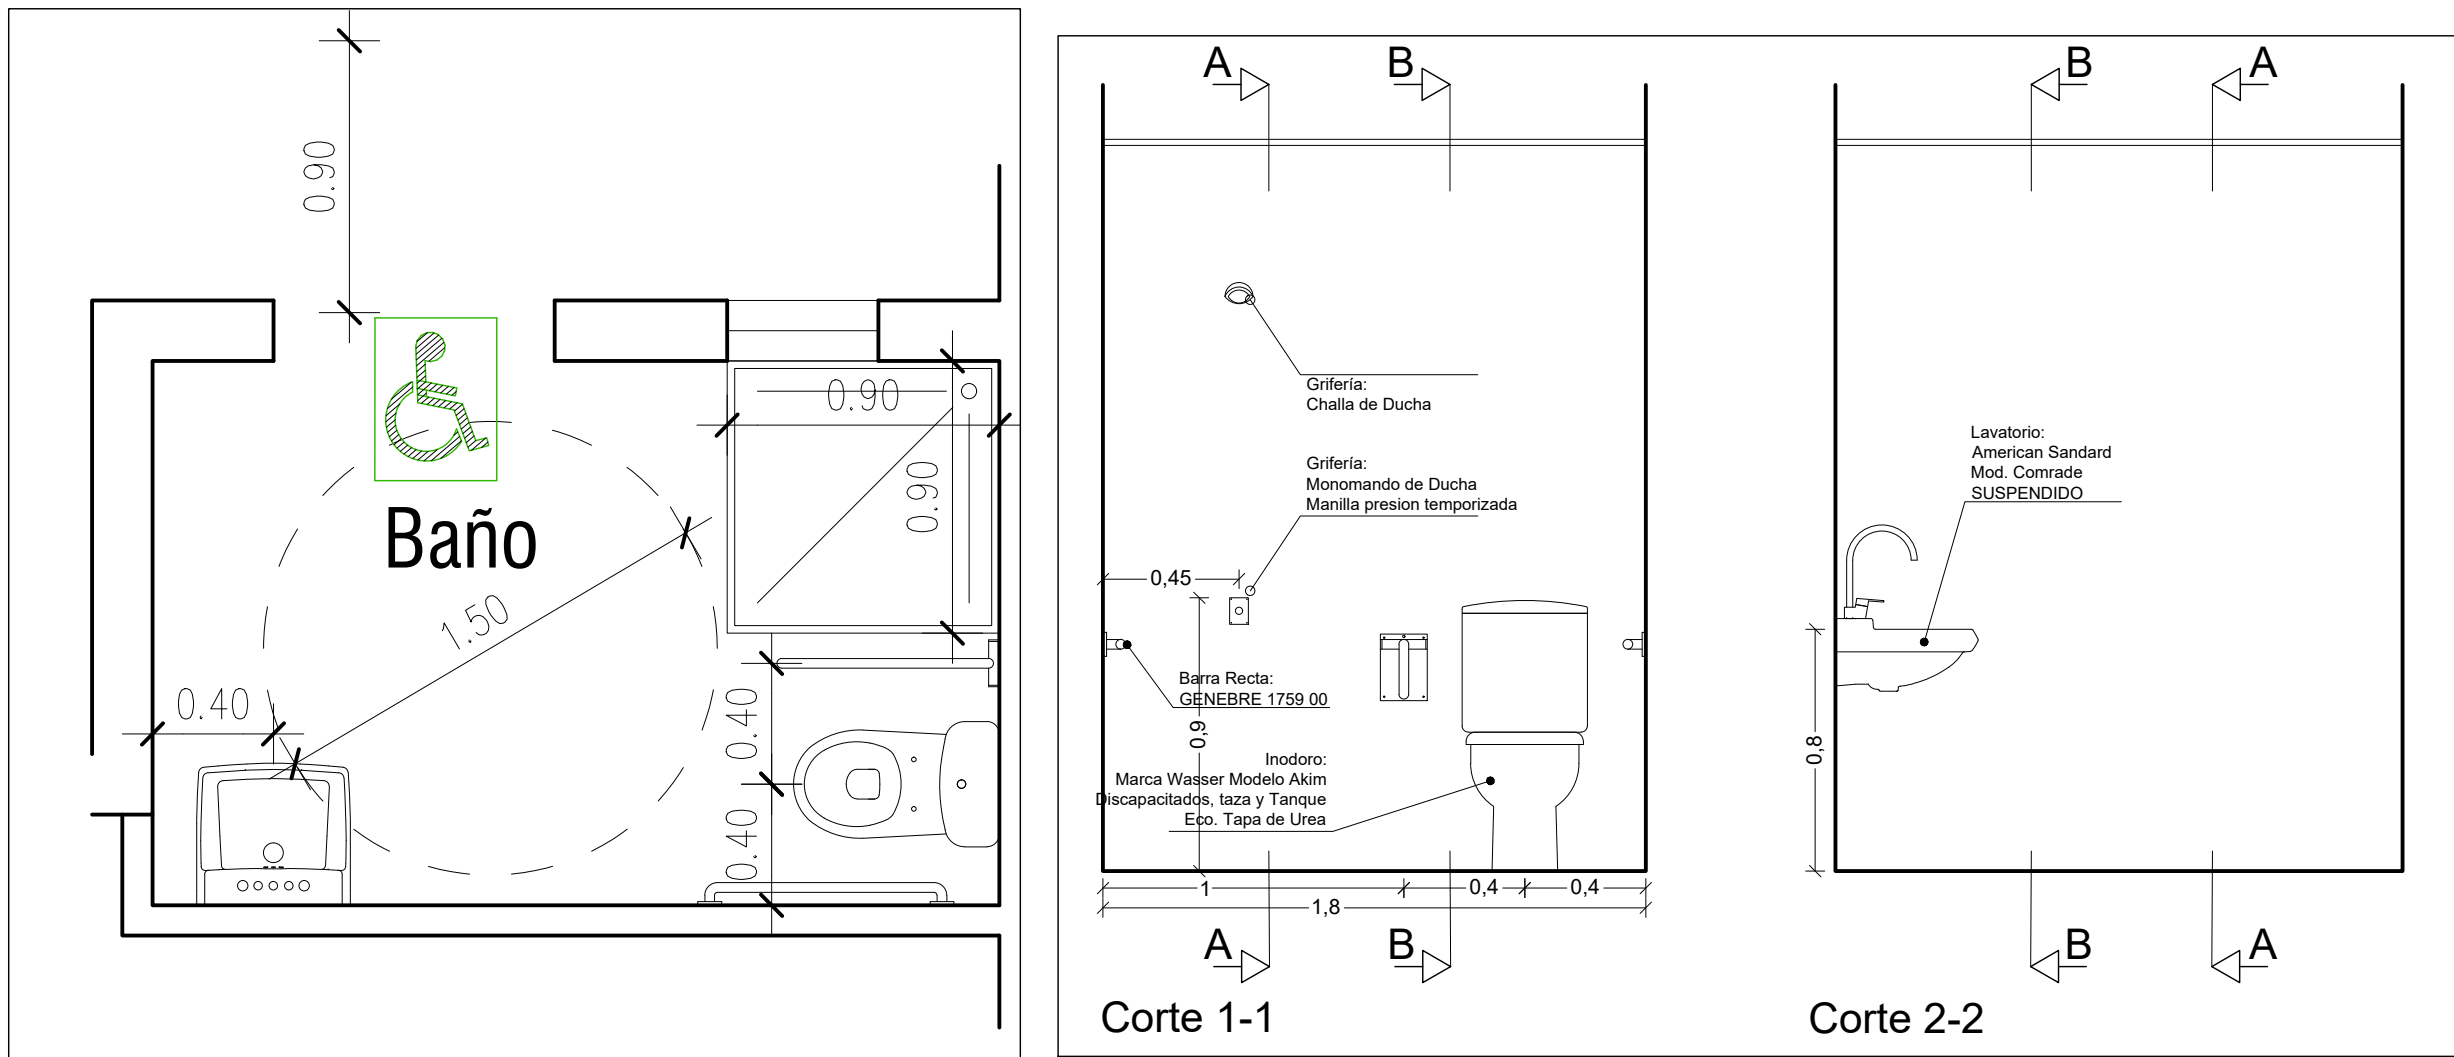

Informe de Accesibilidad
Centro Recreacional C.C.A.F. Los Andes Beaucheff

Santiago, 12 de Agosto de 2022

El presente informe se refiere a las medidas para dar accesibilidad universal al centro recreacional Beaucheff de la C.C.A.F Los Andes, las que han sido consideradas ya que las áreas verdes del recinto corresponden con espacio de uso público.

El centro ha sido diseñado de manera que cualquier persona pueda tener acceso a las instalaciones existentes en el de manera independiente, sin asistencia de otra persona. Esto ha sido considerado proyectando las circulaciones y accesos, de acuerdo a lo indicado en el artículo 4.1.7 de la O.G.U.C.

La circulación se resuelve con senderos que conducen a todas las instalaciones, los que cumplen con las condiciones requeridas para ser accesibles. En el centro no existen desniveles que requieran rampas. Se remodelan baños existentes en los niveles con uso público así como cajas para permitir su uso universal.

- 1: ACCESO:
Acceso sin desniveles, con dimensiones y superficies de acuerdo a lo indicado en la normativa.
- 2: RUTA ACCESIBLE:
La ruta accesible cuenta con un ancho libre mínimo de 1.5 m, permitiendo la circulación y el giro de personas con movilidad reducida. El pavimentos es antideslizante y de color claro para permitir su adecuada visibilidad.
La ruta conduce de manera ininterrumpida a todas las instalaciones

3: BAÑO UNIVERSAL
El centro dispone de 1 baño universal en el sector piscinas, el que cuenta con los artefactos y grifería adecuada para uso universal. Este baño considera ducha a nivel, de manera de permitir su uso sin asistencia por personas en situación de discapacidad..

El centro no considera otras edificaciones que requieran acceso universal

Tomas Fajardo C.
Arquitecto

ARCHIVO: ARCHIVO:

VERSIONES	CONTENIDO LAMINA:		
	Memoria y Plano de Accesibilidad		
	NOMBRE	FECHA	EDICION
	DIB JMA	12-08-22	1.0
	EDI		
	EDI		
	EDI		
	EDI		
	EDI		
	EDI		
	EDI		
	EDI		

CONTENIDO LAMINA:
Memoria y Plano de Accesibilidad



Av. Providencia 2653 of. 1307, Santiago
+562 2244 4544 - +562 2946 1389
info@ccciudad.cl

CODIGO: CRB - 2022 - IA

FIRMA PROPIETARIO / REPRESENTANTE LEGAL

C.C.A.F. de Los Andes
FIRMA ARQUITECTO

Tomás Fajardo Cabello - Arquitecto PUC - I.C.A. 8373
tomasfajardo@cfcjardo.cl
FIRMA REVISOR MUNICIPAL

D.O.M. Municipalidad

OBRA:

INFORME
ACCESIBILIDAD
CR BEAUCHEFF

CAJA DE COMPENSACION LOS ANDES

DIRECCION : Beaucheff n°3500
COMUNA : Pedro Aguirre Cerda
ROL : 2971 - 1

NOMBRE	FECHA	Lamina: 01 de 01
DIB JMA	18-08-22	
REV TFC	08-22	
ESC	INDICADAS	

A01